



PRISCILA

EXECUTIVO - COZINHA



CLIENTE: **PRISCILA**

AMBIENTE: **Cozinha**

PROJETISTA TÉCNICO: **JOÃO FELIPE SANTOS**

ARQUITETA: **FERNANDA**

ATENÇÃO:

DECLARO ESTAR DE ACORDO COM ESTE PROJETO E COM AS MEDIDAS NELE DESCRITAS E CIENTE DE QUE NELE CONSTAM APENAS PEÇAS E MÓDULOS DA EMPRESA, SENDO QUE OS DEMAIS ITENS SÃO MERAMENTE ILUSTRATIVOS (TAIS COMO ELETROS, COLCHÕES, GRANITOS E DECORAÇÕES NO GERAL).

ASS: _____

**PRANCHA
02**

CONTRATO

LEIA COM ATENÇÃO

1- CLIENTE ESTÁ RECEBENDO UMA CÓPIA DOS PROJETOS ADQUIRIDOS E ESTÁ DE ACORDO COM AS INFORMAÇÕES APONTADAS SOBRE MODELO, COR, ACABAMENTO, ESTRUTURAS, ACESSÓRIOS E CONDIÇÕES QUE FAZEM PARTE DESTES PROJETOS EXECUTIVOS.

2- O MESMO FOI ELABORADO CONSIDERANDO AS MEDIDAS REAIS DESTES AMBIENTES, SE HOUVER ALGUMA ALTERAÇÃO NO PÉ DIREITO OU NAS PAREDES, REFERENTE À INSTALAÇÃO DE MOLDURAS DE GESSO, RODAPÉS, MODIFICAÇÃO EM INSTALAÇÃO DA MODULAÇÃO NO DIA DA MONTAGEM, A EMPRESA NÃO SE RESPONSABILIZA QUANTO A FUTUROS CONTRATEMPOS DEVIDOS ÀS ALTERAÇÕES. CABE AO CLIENTE AVISAR O PROJETISTA ANTES DA MEDIÇÃO FINAL PARA ADEQUAÇÃO DA MODULAÇÃO.

3- SE HOUVER GRANITO NOS AMBIENTES, A MEDIÇÃO FINAL SE DARÁ APÓS A CONCLUSÃO DA INSTALAÇÃO DOS MESMOS, OU INSTALAR APÓS A MONTAGEM DOS MÓVEIS.

4- SE HOUVER REDUÇÃO OU RECORTES NOS MÓDULOS, O CLIENTE TOMA CIÊNCIA QUE OS AJUSTES SERÃO EXECUTADOS NO LOCAL, QUE DEVE ESTAR LIVRE DE OBJETOS E PESSOAS QUE POSSAM SOFRER DE ALGUMA MANEIRA COM O PÓ DECORRENTE DESSES AJUSTES E QUALQUER OBJETO QUE NÃO POSSA SER RETIRADO DEVE ESTAR DEVIDAMENTE COBERTO. POR NÃO POSSUIR PROFISSIONÁIS ESPECIALIZADOS EM INSTALAÇÕES DE ELETROS, INSTALAÇÕES HIDRÁULICAS, A EMPRESA NÃO EFETUARÁ ESSE TIPO DE SERVIÇO. É NECESSÁRIO FORNECER AS PLANTAS DE INSTALAÇÃO ELÉTRICA E HIDRÁULICA DOS AMBIENTES NO DIA DA MONTAGEM, É NECESSÁRIO O ACOMPANHAMENTO DO CLIENTE OU UM RESPONSÁVEL PELA OBRA, MAIOR QUE 18 ANOS PARA TIRAR EVENTUAIS DÚVIDAS DOS MONTADORES REFERENTE AOS LOCAIS ONDE É POSSÍVEL FAZER FURAÇÕES. A ASSINATURA DESSE PROJETO SUBSTITUI QUALQUER PROJETO ANTERIOR.

5- O CLIENTE DECLARA ESTAR CIENTE QUE CASO O PROJETO ENVOLVA ELETROS, OS MESMOS DEVERÃO ESTAR NO LOCAL NO DIA DA MONTAGEM PARA ADEQUAÇÃO DOS NICHOS NECESSÁRIOS, E SE NÃO COMPROU OS ELETROS, SE RESPONSABILIZA EM ADQUIRIR OS MESMOS DENTRO DAS MEDIDAS ESPECIFICADAS NESTE PROJETO.

6- DECLARO ESTAR DE ACORDO COM ESTE PROJETO E COM AS MEDIDAS NELE DESCRITAS E CIENTE DE QUE NELE CONSTAM APENAS PEÇAS E MÓDULOS DA EMPRESA DUO PLANEJADOS, SENDO QUE OS DEMAIS ITENS SÃO MERAMENTE ILUSTRATIVOS (TAIS COMO ELETROS, COLCHÕES, GRANITOS E DECORAÇÕES EM GERAL).



CLIENTE: **PRISCILA**

AMBIENTE: **Cozinha**

PROJETISTA TÉCNICO: **JOÃO FELIPE SANTOS**

ARQUITETA: **FERNANDA**

ATENÇÃO:

DECLARO ESTAR DE ACORDO COM ESTE PROJETO E COM AS MEDIDAS NELE DESCRITAS E CIENTE DE QUE NELE CONSTAM APENAS PEÇAS E MÓDULOS DA EMPRESA, SENDO QUE OS DEMAIS ITENS SÃO MERAMENTE ILUSTRATIVOS (TAIS COMO ELETROS, COLCHÕES, GRANITOS E DECORAÇÕES NO GERAL).

ASS.: _____

**PRANCHA
03**

PLANTA - ESPECIFICAÇÕES DO PROJETO

ESPECIFICAÇÕES DO PROJETO

CORES E ACABAMENTOS:

Caixa Módulos (Interno): **Branco, Nude, Freijo Puro**

Portas e Frentes: **Nude, Freijo Puro**

Tamponamentos: **Freijo Puro, Nude, Branco**

Painéis e Tapos: **Freijo Puro, Nude, Branco**

Puxadores: **Champagne**

Portas de Vidro: **Vidro Reflecta Bronze .. (Posição 1)**

FERRAGENS E ACESSÓRIOS:

Dobradiças:

Dobradiça Reta c/ Amortecedor, Dobradiça Super Curva c/ Amortecedor

Corrediças: **Gaveta Corrediça Telescópica**

Puxadores:

Puxador Alumínio Cava Bronze - 196x55x18mm, Puxador Alumínio Cava Bronze - 236.499x55x18mm, Puxador Alumínio Cava Bronze - 386x55x18mm, Puxador Alumínio Cava Bronze - 387x55x18mm, Puxador Alumínio Cava Bronze - 461.5x55x18mm, Puxador Alumínio Cava Bronze - 496.5x55x18mm, Puxador Alumínio Cava Bronze - 834x55x18mm, Puxador Curvo Champagne · (Posição 4), Puxador Linear (15, 18 e 20mm) Pino Champagne - 200mm

Ferragens especiais:

ESPESSURAS:


Caixa Módulos (Interno): **18mm e 25mm (fundo 6mm)**

Prateleiras internas: **18mm**

Portas e Frentes: **18mm**

Tamponamentos: **15mm e 18mm**

Painéis e Tapos e perfil: **6mm e 15mm e 18mm e 25mm**

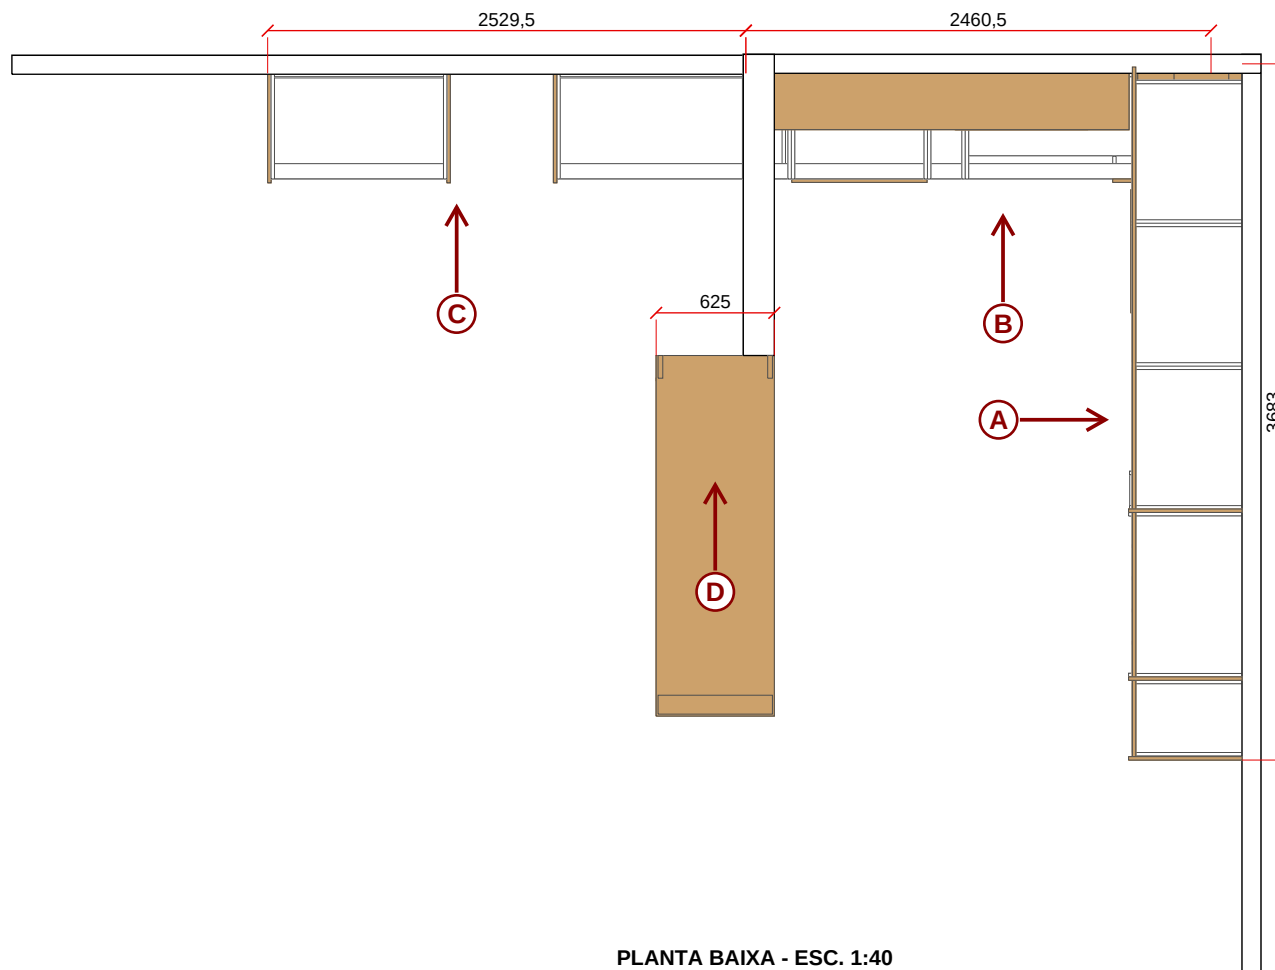

PLANTA BAIXA - ESC. 1:40



CLIENTE: **PRISCILA**

AMBIENTE: **Cozinha**

PROJETISTA TÉCNICO: **JOÃO FELIPE SANTOS**

ARQUITETA: **FERNANDA**

ATENÇÃO:

DECLARO ESTAR DE ACORDO COM ESTE PROJETO E COM AS MEDIDAS NELE DESCRITAS E CIENTE DE QUE NELE CONSTAM APENAS PEÇAS E MÓDULOS DA EMPRESA, SENDO QUE OS DEMAIS ITENS SÃO MERAMENTE ILUSTRATIVOS (TAIS COMO ELETROS, COLCHÕES, GRANITOS E DECORAÇÕES NO GERAL).

ASS.: _____

**PRANCHA
04**

VISÃO GERAL DOS MÓVEIS


VISTA A




VISTA B



VISTA C

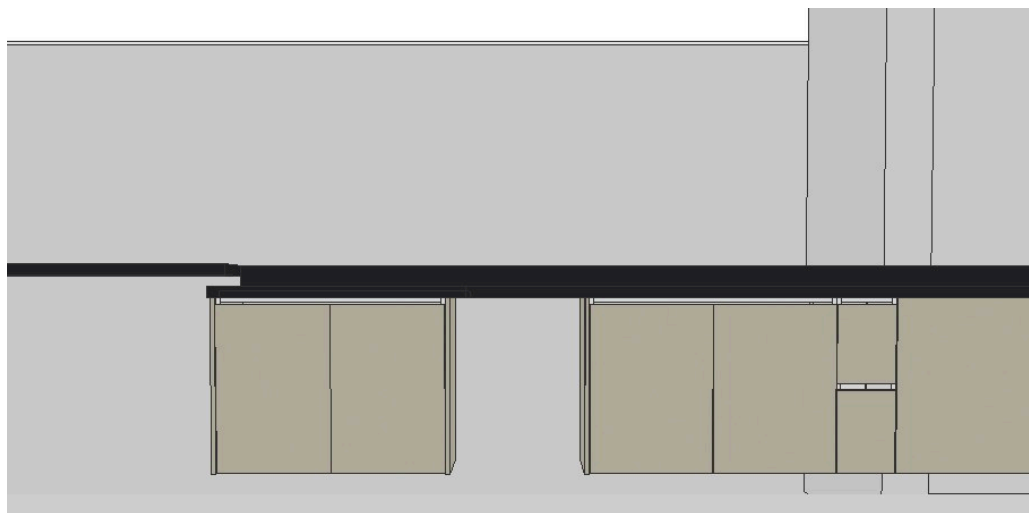

PAINEL COM NICHOS

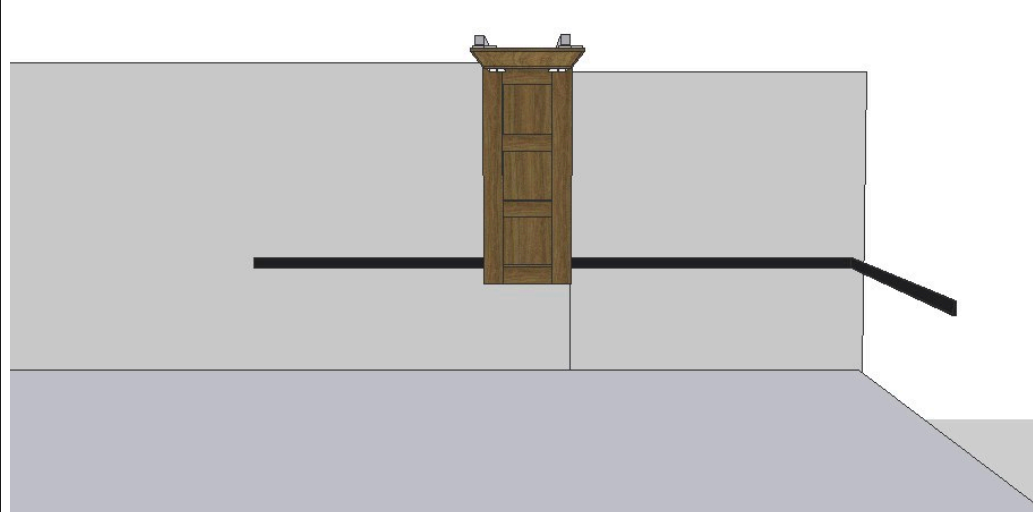



CLIENTE: **PRISCILA**

AMBIENTE: **Cozinha**

PROJETISTA TÉCNICO: **JOÃO FELIPE SANTOS**

ARQUITETA: **FERNANDA**

ATENÇÃO:

DECLARO ESTAR DE ACORDO COM ESTE PROJETO E COM AS MEDIDAS NELE DESCRITAS E CIENTE DE QUE NELE CONSTAM APENAS PEÇAS E MÓDULOS DA EMPRESA, SENDO QUE OS DEMAIS ITENS SÃO MERAMENTE ILUSTRATIVOS (TAIS COMO ELETROS, COLCHÕES, GRANITOS E DECORAÇÕES NO GERAL).

ASS.: _____



**PRANCHA
05**

MÓDULOS E PAINÉIS - VISTA A - SUPERIORES

Item	Descrição	Dimensão
1	Armário Despenseiro	400x2390x580
2	Armário Superior	756x586x580
3	Armário Superior	870x490x580
4	Armário Superior	950x400x430
5	Armário Adega/Nicho	150x870x600
6	Painel Branco MDF	100x15x266
7	Painel Branco MDF	266x15x150
8	Painel Freijo Puro MDF	320x15x120
9	Painel Freijo Puro MDF	320x15x200
10	Painel Freijo Puro MDF	1286x15x400
11	Painel Freijo Puro MDF	404x18x97
12	Painel Freijo Puro MDF	400x18x70
13	Painel Freijo Puro MDF	436x18x450
14	Painel Freijo Puro MDF	2337x18x450
15	Painel Freijo Puro MDF	400x18x450
16	Painel Nude MDP	2487x18x600
17	Painel Nude MDP	870x18x97
18	Painel Nude MDP	2338x18x97
19	Painel Nude MDP	586x18x70
20	Tamponamento Inferior	2305x18x70
21	Tamponamento Inferior	2355x18x220
22*	QUADRO EM C SUPERIOR 20 X 20 X	20x1024x318
23*	SUPORTE FIXAÇÃO METALON 36 X 18 P	36x2x18

* não localizado no DXF - conferir

DETALHE - NICHOS

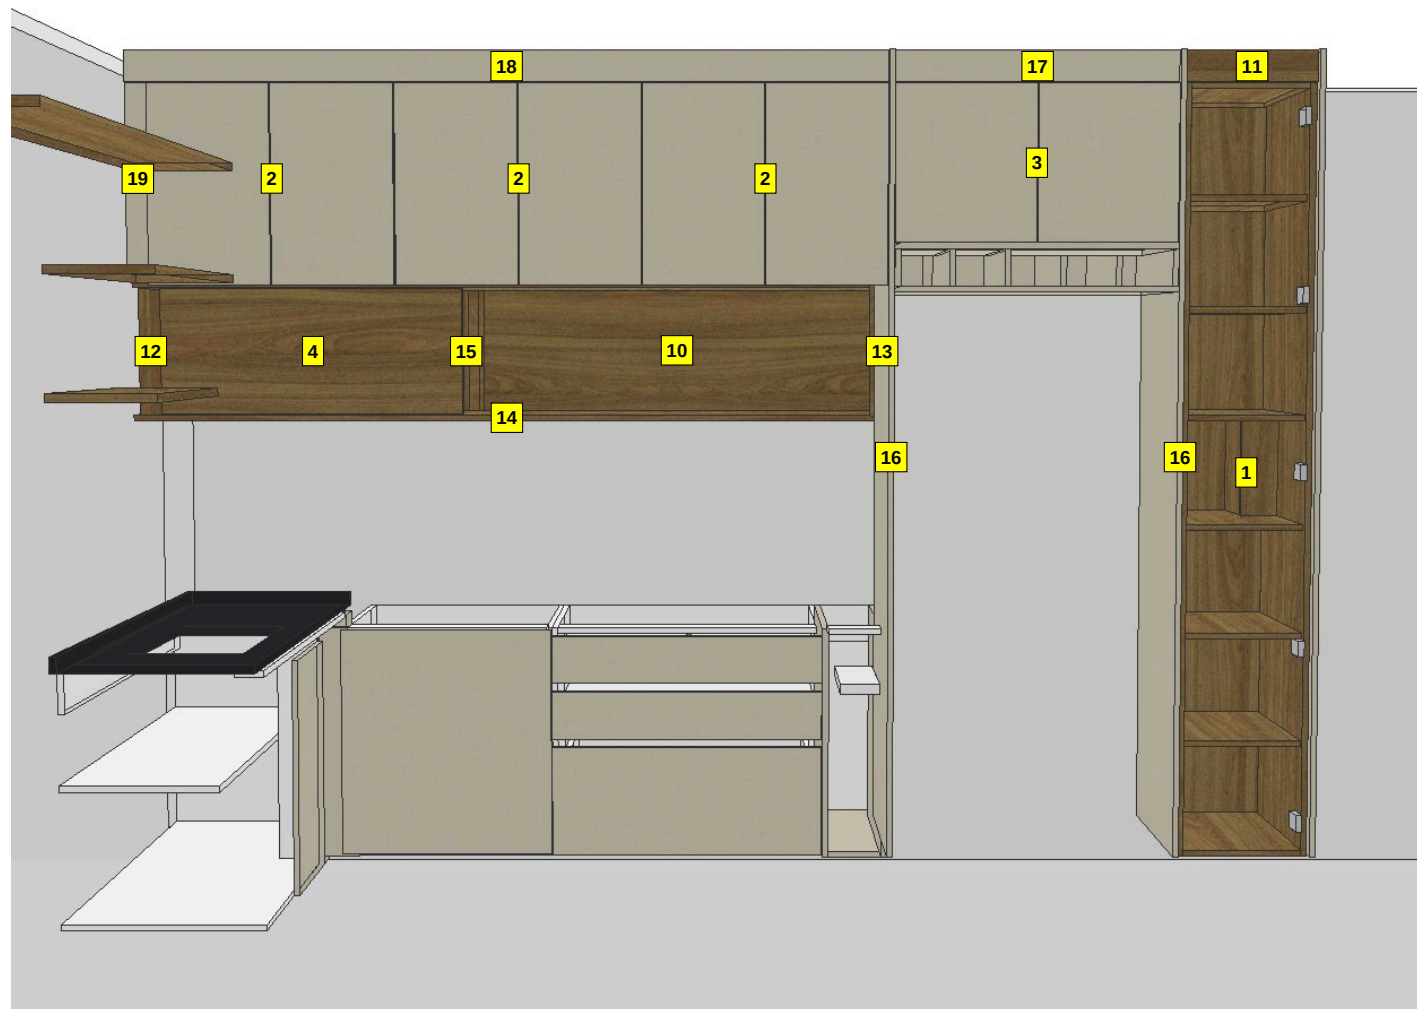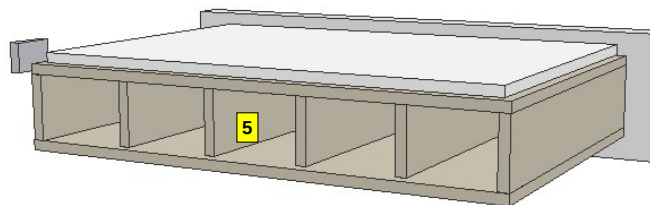



CLIENTE: **PRISCILA**

AMBIENTE: **Cozinha**

PROJETISTA TÉCNICO: **JOÃO FELIPE SANTOS**

ARQUITETA: **FERNANDA**

ATENÇÃO:

DECLARO ESTAR DE ACORDO COM ESTE PROJETO E COM AS MEDIDAS NELE DESCRITAS E CIENTE DE QUE NELE CONSTAM APENAS PEÇAS E MÓDULOS DA EMPRESA, SENDO QUE OS DEMAIS ITENS SÃO MERAMENTE ILUSTRATIVOS (TAIS COMO ELETROS, COLCHÕES, GRANITOS E DECORAÇÕES NO GERAL).



ASS.: _____

**PRANCHA
06**

MÓDULOS E PAINÉIS - VISTA A - SUPERIORES - DETALHE 1

Item	Descrição	Dimensão
6	Painel Branco MDF	100x15x266
7	Painel Branco MDF	266x15x150
14	Painel Freijo Puro MDF	2337x18x450
20	Tamponamento Inferior	2305x18x70

COMO FICA MONTADO

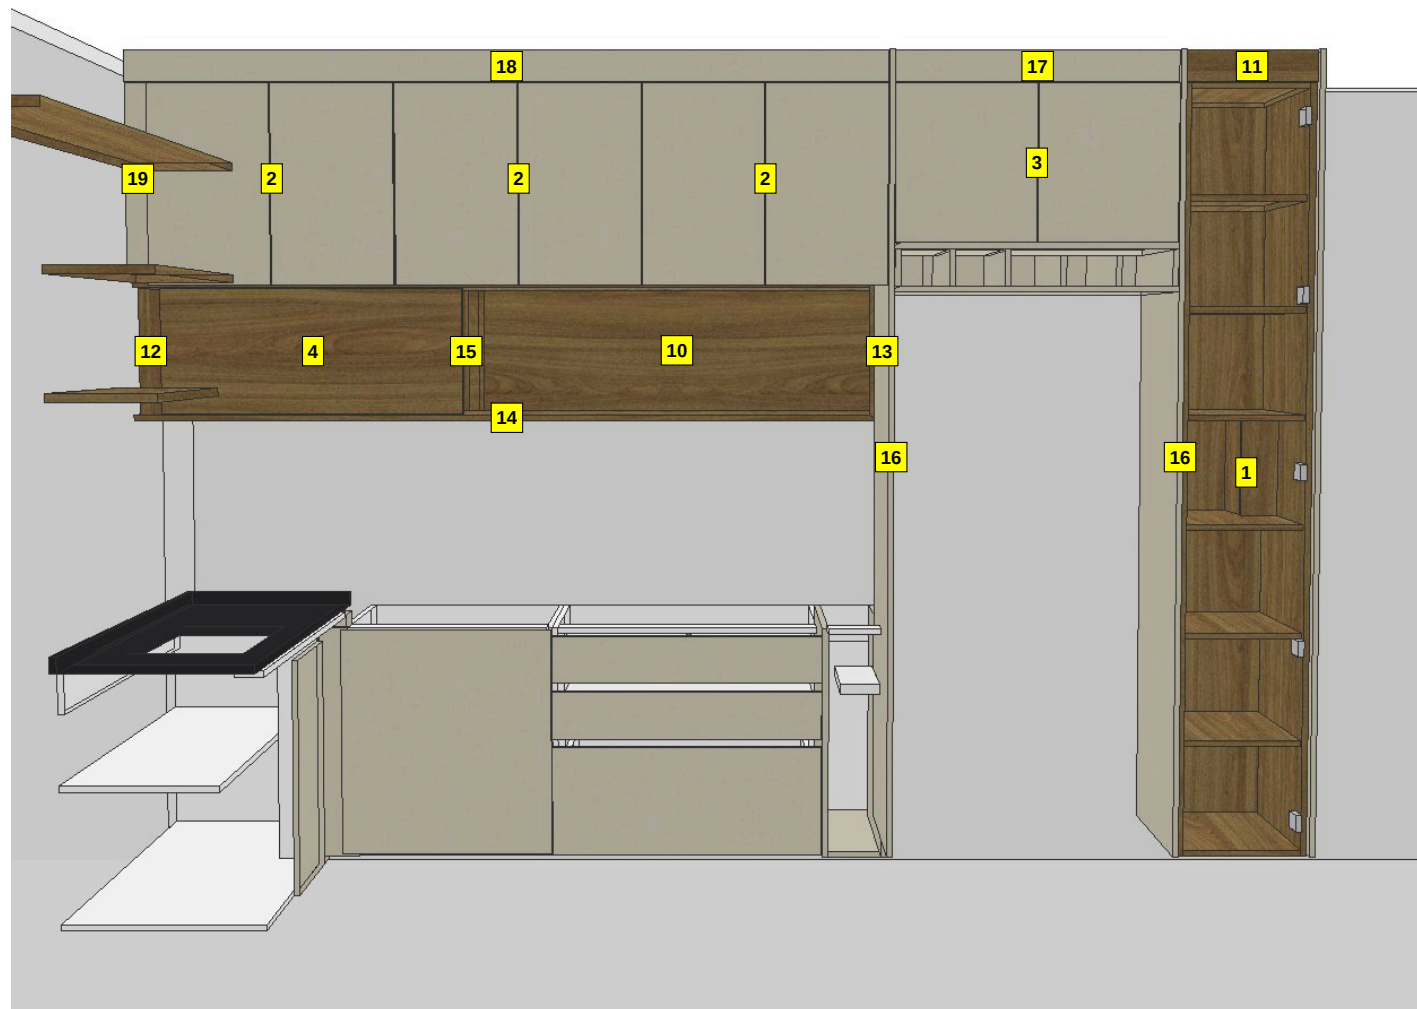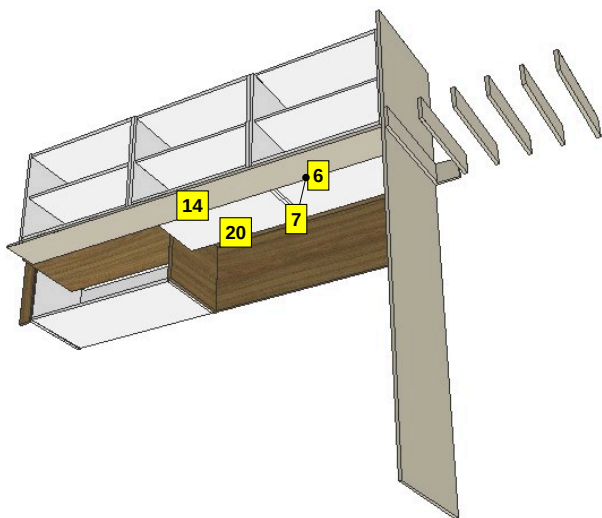



CLIENTE: **PRISCILA**

AMBIENTE: **Cozinha**

PROJETISTA TÉCNICO: **JOÃO FELIPE SANTOS**

ARQUITETA: **FERNANDA**

ATENÇÃO:

DECLARO ESTAR DE ACORDO COM ESTE PROJETO E COM AS MEDIDAS NELE DESCRITAS E CIENTE DE QUE NELE CONSTAM APENAS PEÇAS E MÓDULOS DA EMPRESA, SENDO QUE OS DEMAIS ITENS SÃO MERAMENTE ILUSTRATIVOS (TAIS COMO ELETROS, COLCHÕES, GRANITOS E DECORAÇÕES NO GERAL).



ASS.: _____

**PRANCHA
07**

MÓDULOS E PAINÉIS - VISTA A - SUPERIORES - DETALHE 2

Item	Descrição	Dimensão
8	Painel Freijo Puro MDF	320x15x120
9	Painel Freijo Puro MDF	320x15x200
16	Painel Nude MDP	2487x18x600

COMO FICA MONTADO

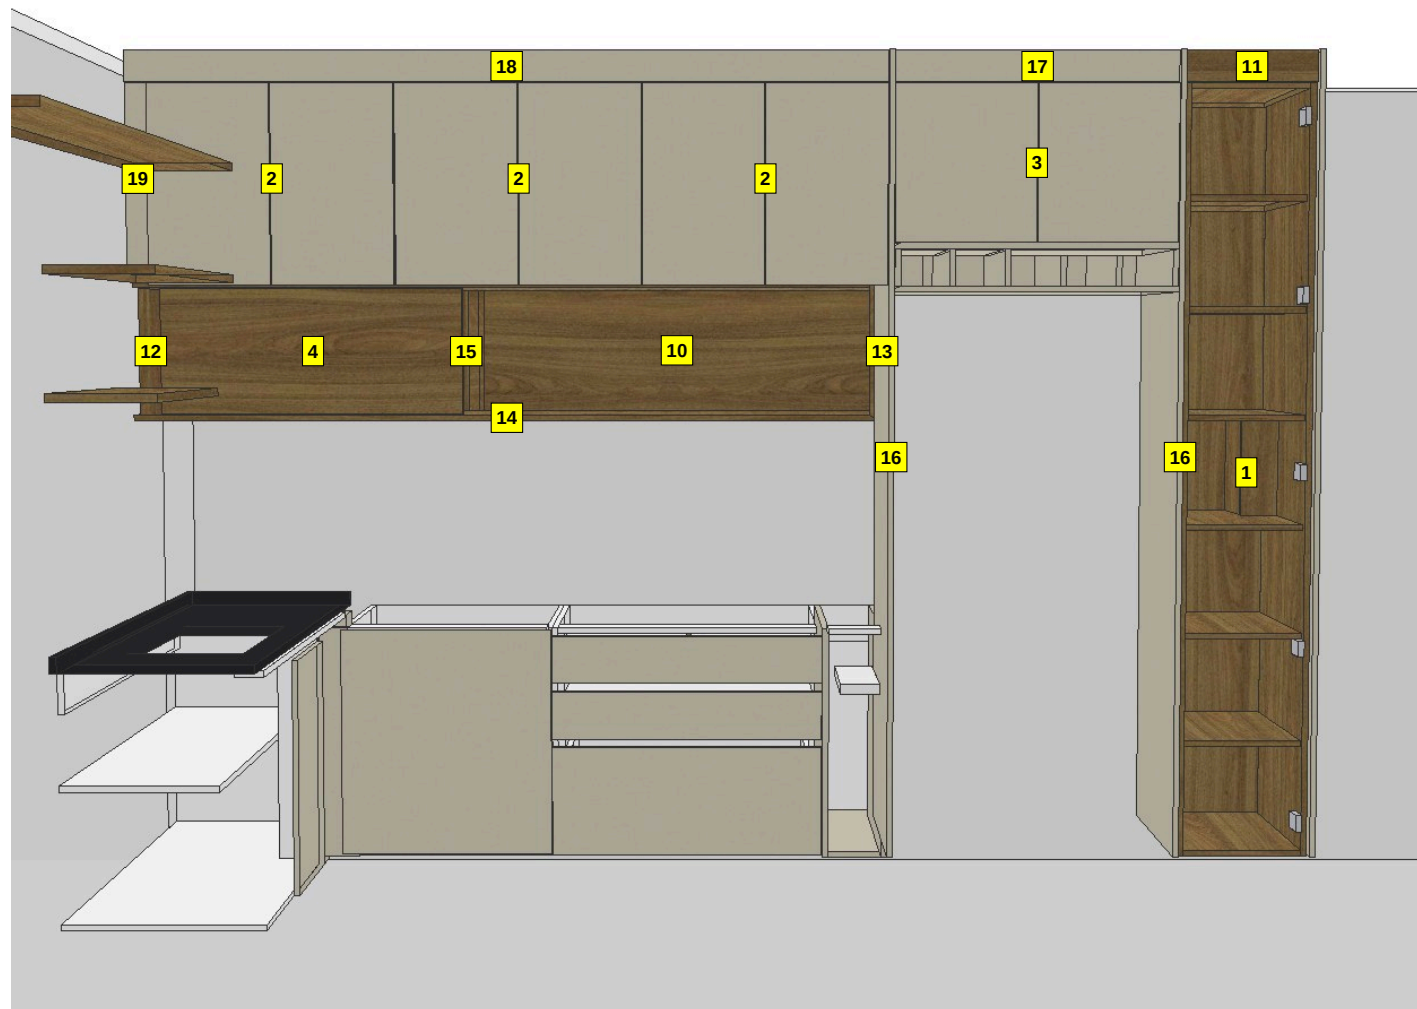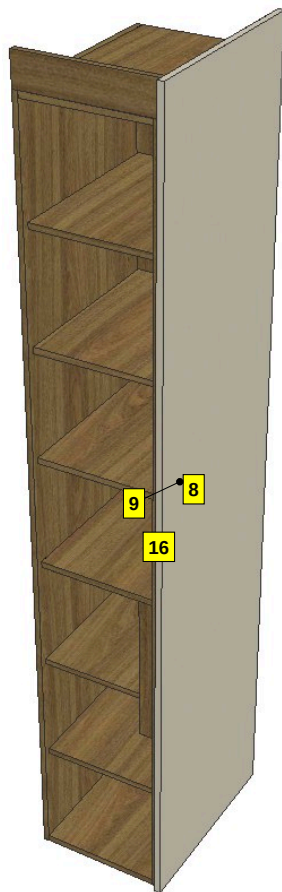



CLIENTE: **PRISCILA**

AMBIENTE: **Cozinha**

PROJETISTA TÉCNICO: **JOÃO FELIPE SANTOS**

ARQUITETA: **FERNANDA**

ATENÇÃO:

DECLARO ESTAR DE ACORDO COM ESTE PROJETO E COM AS MEDIDAS NELE DESCRITAS E CIENTE DE QUE NELE CONSTAM APENAS PEÇAS E MÓDULOS DA EMPRESA, SENDO QUE OS DEMAIS ITENS SÃO MERAMENTE ILUSTRATIVOS (TAIS COMO ELETROS, COLCHÕES, GRANITOS E DECORAÇÕES NO GERAL).


ASS.: _____

**PRANCHA
08**

MÓDULOS E PAINÉIS - VISTA A - SUPERIORES - DETALHE 3

Item	Descrição	Dimensão
21	Tamponamento Inferior	2355x18x220

COMO FICA MONTADO

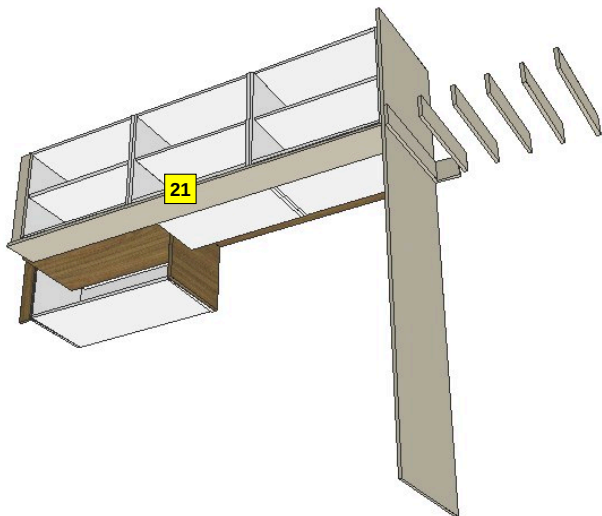



CLIENTE: **PRISCILA**

AMBIENTE: **Cozinha**

PROJETISTA TÉCNICO: **JOÃO FELIPE SANTOS**

ARQUITETA: **FERNANDA**

ATENÇÃO:

DECLARO ESTAR DE ACORDO COM ESTE PROJETO E COM AS MEDIDAS NELE DESCRITAS E CIENTE DE QUE NELE CONSTAM APENAS PEÇAS E MÓDULOS DA EMPRESA, SENDO QUE OS DEMAIS ITENS SÃO MERAMENTE ILUSTRATIVOS (TAIS COMO ELETROS, COLCHÕES, GRANITOS E DECORAÇÕES NO GERAL).



ASS.: _____

**PRANCHA
09**

MÓDULOS E PAINÉIS - VISTA A - INFERIORES

Item	Descrição	Dimensão
1	Balcão Inferior	200x714x595
2	Balcão Inferior	838x714x570
3	Balcão 2 Portas	650x714x570
4	Painel Nude MDP	700x18x650

DETALHE - NICHOS

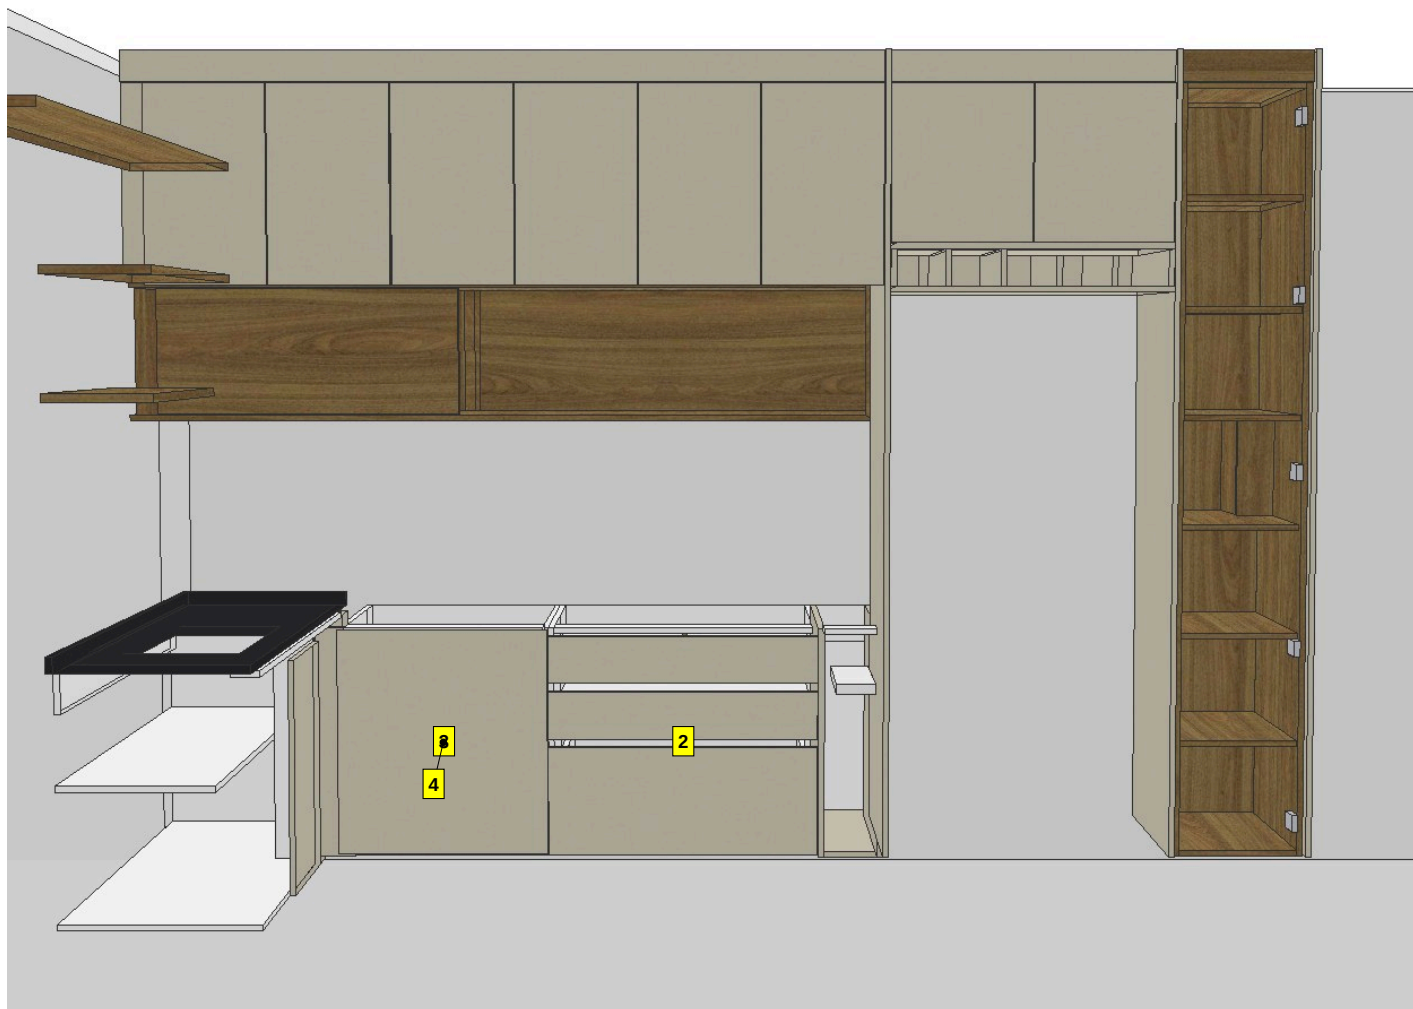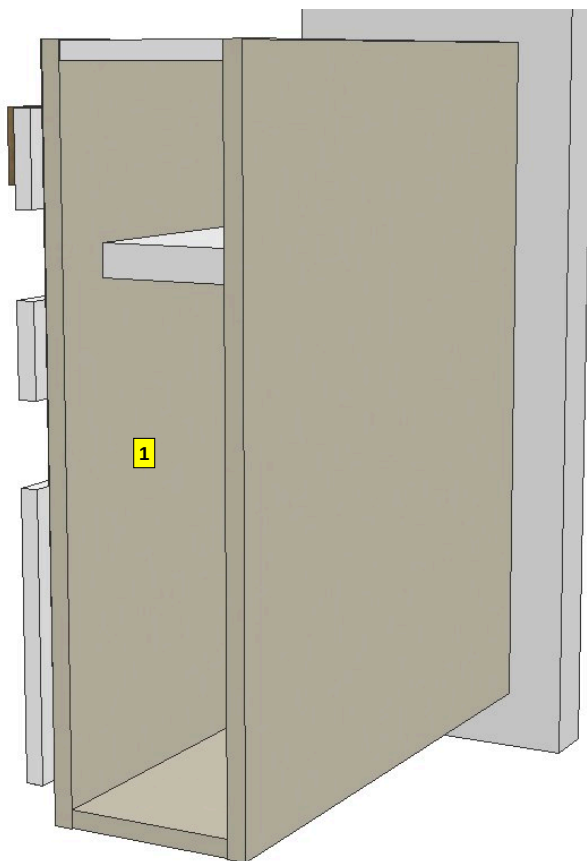



CLIENTE: **PRISCILA**

AMBIENTE: **Cozinha**

PROJETISTA TÉCNICO: **JOÃO FELIPE SANTOS**

ARQUITETA: **FERNANDA**

ATENÇÃO:


DECLARO ESTAR DE ACORDO COM ESTE PROJETO E COM AS MEDIDAS NELE DESCRITAS E CIENTE DE QUE NELE CONSTAM APENAS PEÇAS E MÓDULOS DA EMPRESA, SENDO QUE OS DEMAIS ITENS SÃO MERAMENTE ILUSTRATIVOS (TAIS COMO ELETROS, COLCHÕES, GRANITOS E DECORAÇÕES NO GERAL).

ASS.: _____

PRANCHA 10

MÓDULOS E PAINÉIS - VISTA B

Item	Descrição	Dimensão
1	Balcão Inferior	1300x714x559
2	Balcão Inferior	200x714x559
3	Balcão Inferior	240,5x714x559
4	Balcão Inferior	720x714x559
5	Painel Branco MDP	677,5x18x120
6	Painel Branco MDP	1264x18x436
7	Painel Freijo Puro MDF	700x25x298
8	Painel Freijo Puro MDF	919x25x298
9	Painel Freijo Puro MDF	1876x25x298
10	Painel Nude MDP	714x18x520
11	Painel Nude MDP	709x18x715
12	Painel Nude MDP	714x18x120

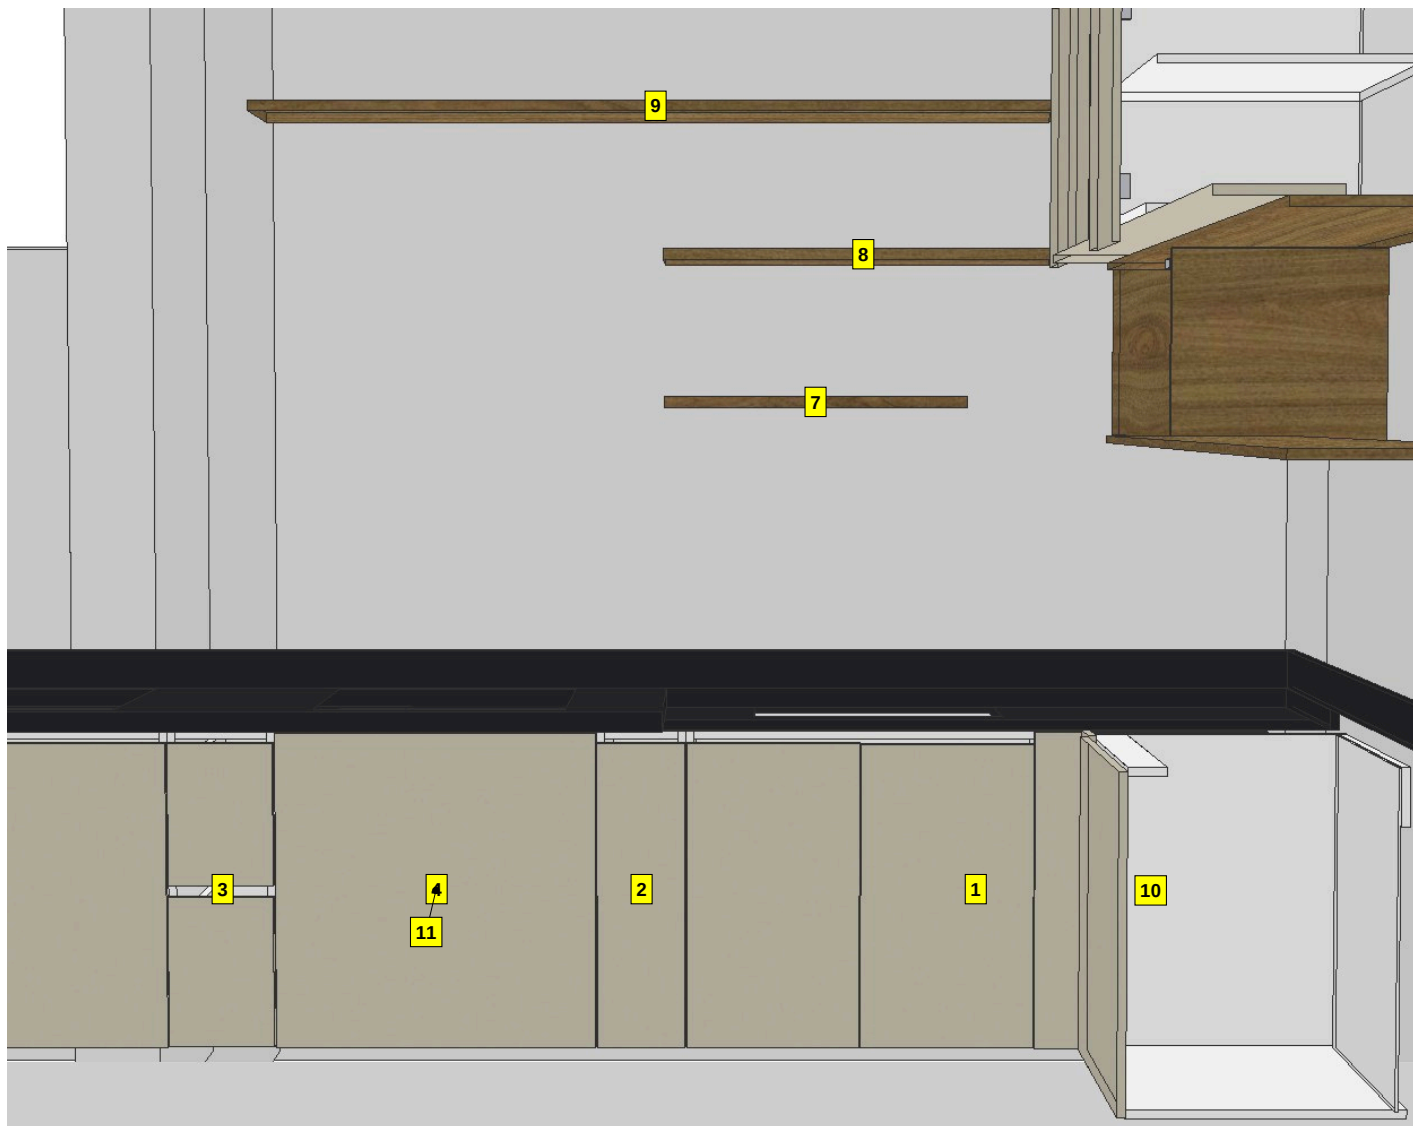



CLIENTE: **PRISCILA**

AMBIENTE: **Cozinha**

PROJETISTA TÉCNICO: **JOÃO FELIPE SANTOS**

ARQUITETA: **FERNANDA**

ATENÇÃO:

DECLARO ESTAR DE ACORDO COM ESTE PROJETO E COM AS MEDIDAS NELE DESCRITAS E CIENTE DE QUE NELE CONSTAM APENAS PEÇAS E MÓDULOS DA EMPRESA, SENDO QUE OS DEMAIS ITENS SÃO MERAMENTE ILUSTRATIVOS (TAIS COMO ELETROS, COLCHÕES, GRANITOS E DECORAÇÕES NO GERAL).



ASS.: _____

PRANCHA 11

MÓDULOS E PAINÉIS - VISTA B - DETALHE 1

Item	Descrição	Dimensão
5	Painel Branco MDP	677,5x18x120
6	Painel Branco MDP	1264x18x436
12	Painel Nude MDP	714x18x120

COMO FICA MONTADO

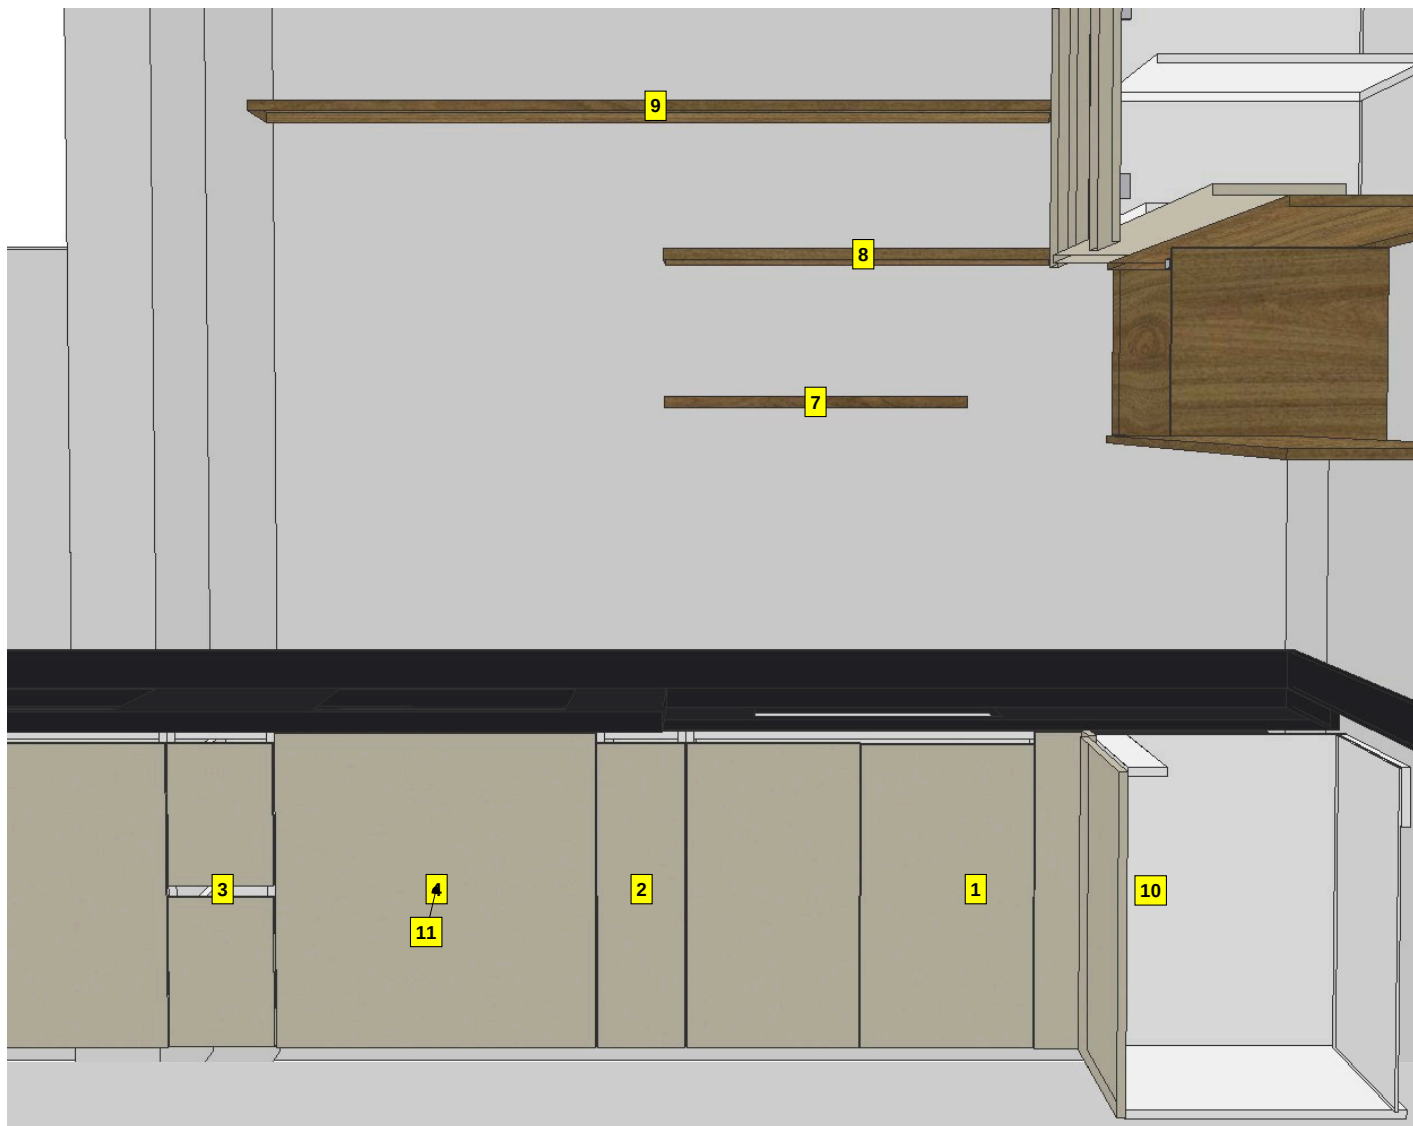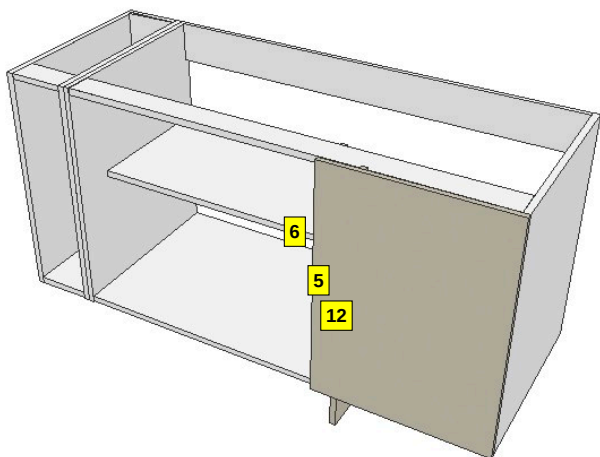

VISTA B - ESC. 1:40



CLIENTE: **PRISCILA**

AMBIENTE: **Cozinha**

PROJETISTA TÉCNICO: **JOÃO FELIPE SANTOS**

ARQUITETA: **FERNANDA**

ATENÇÃO:


DECLARO ESTAR DE ACORDO COM ESTE PROJETO E COM AS MEDIDAS NELE DESCRITAS E CIENTE DE QUE NELE CONSTAM APENAS PEÇAS E MÓDULOS DA EMPRESA, SENDO QUE OS DE MAIS ITENS SÃO MERAMENTE ILUSTRATIVOS (TAIS COMO ELETROS, COLCHÕES, GRANITOS E DECORAÇÕES NO GERAL).

ASS.: _____

PRANCHA 13

MÓDULOS E PAINÉIS - VISTA C

Item	Descrição	Dimensão
1	Balcão Inferior	1000x714x559
2	Balcão Inferior	930x714x559
3	Tamponamento Inferior	714x18x579

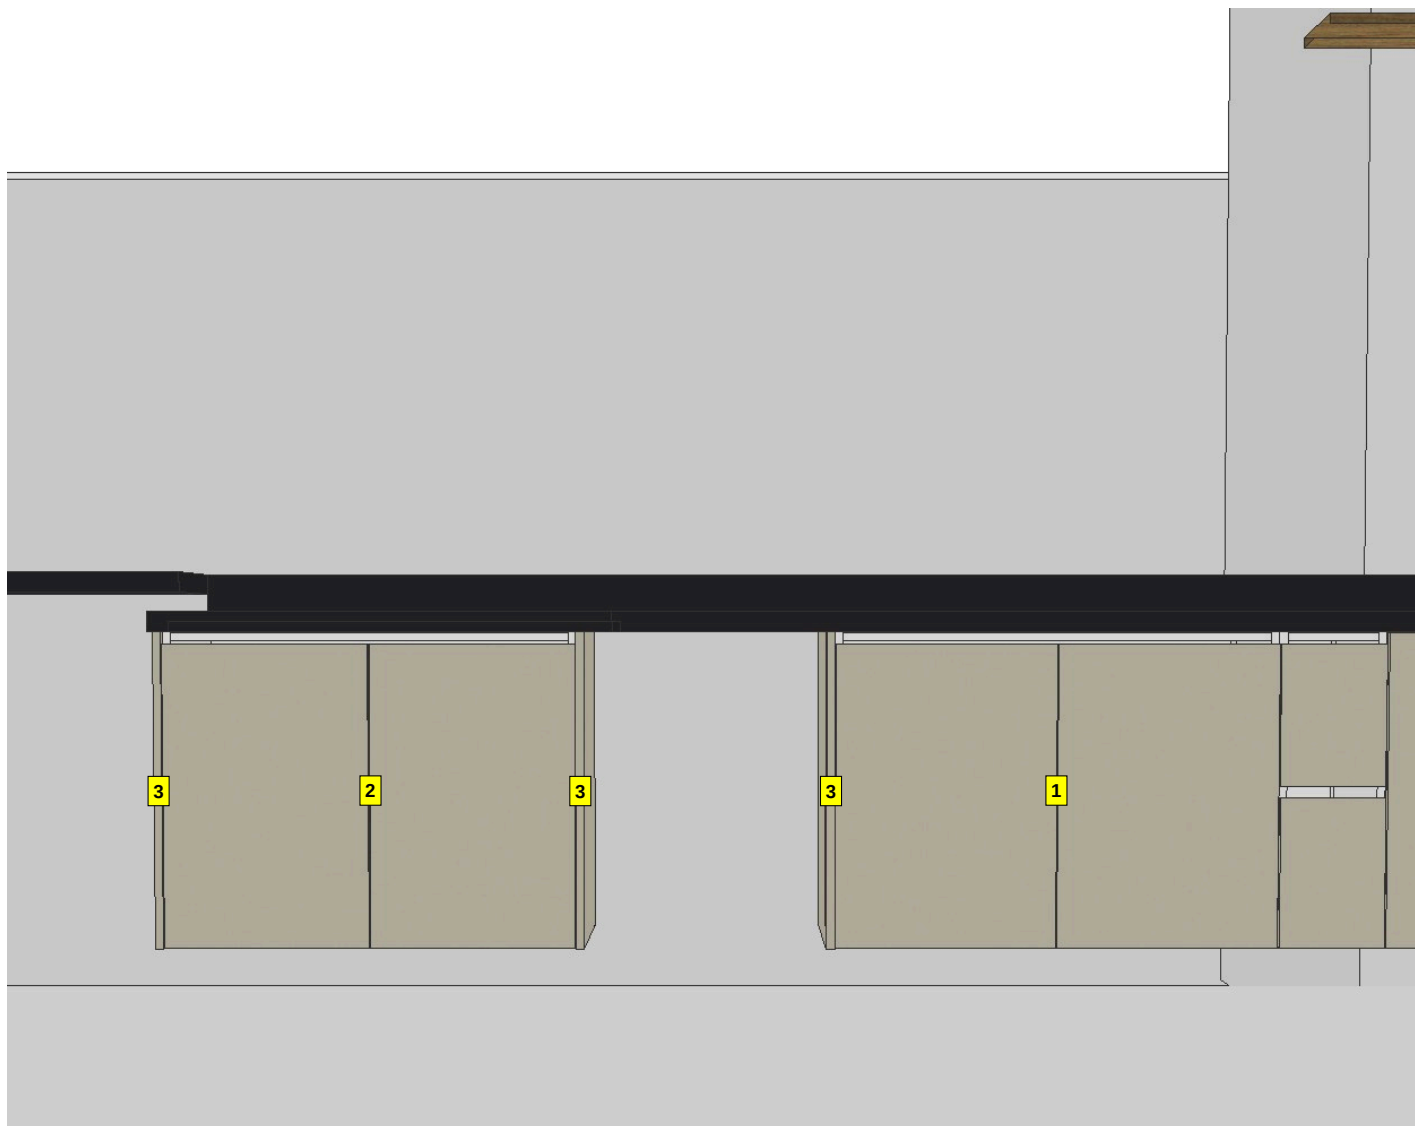



CLIENTE: **PRISCILA**

AMBIENTE: **Cozinha**

PROJETISTA TÉCNICO: **JOÃO FELIPE SANTOS**

ARQUITETA: **FERNANDA**


ATENÇÃO:

DECLARO ESTAR DE ACORDO COM ESTE PROJETO E COM AS MEDIDAS NELE DESCRITAS E CIENTE DE QUE NELE CONSTAM APENAS PEÇAS E MÓDULOS DA EMPRESA, SENDO QUE OS DE MAIS ITENS SÃO MERAMENTE ILUSTRATIVOS (TAIS COMO ELETROS, COLCHÕES, GRANITOS E DECORAÇÕES NO GERAL).

ASS.: _____

PRANCHA
14

MEDIDAS E ALTURAS - VISTA C

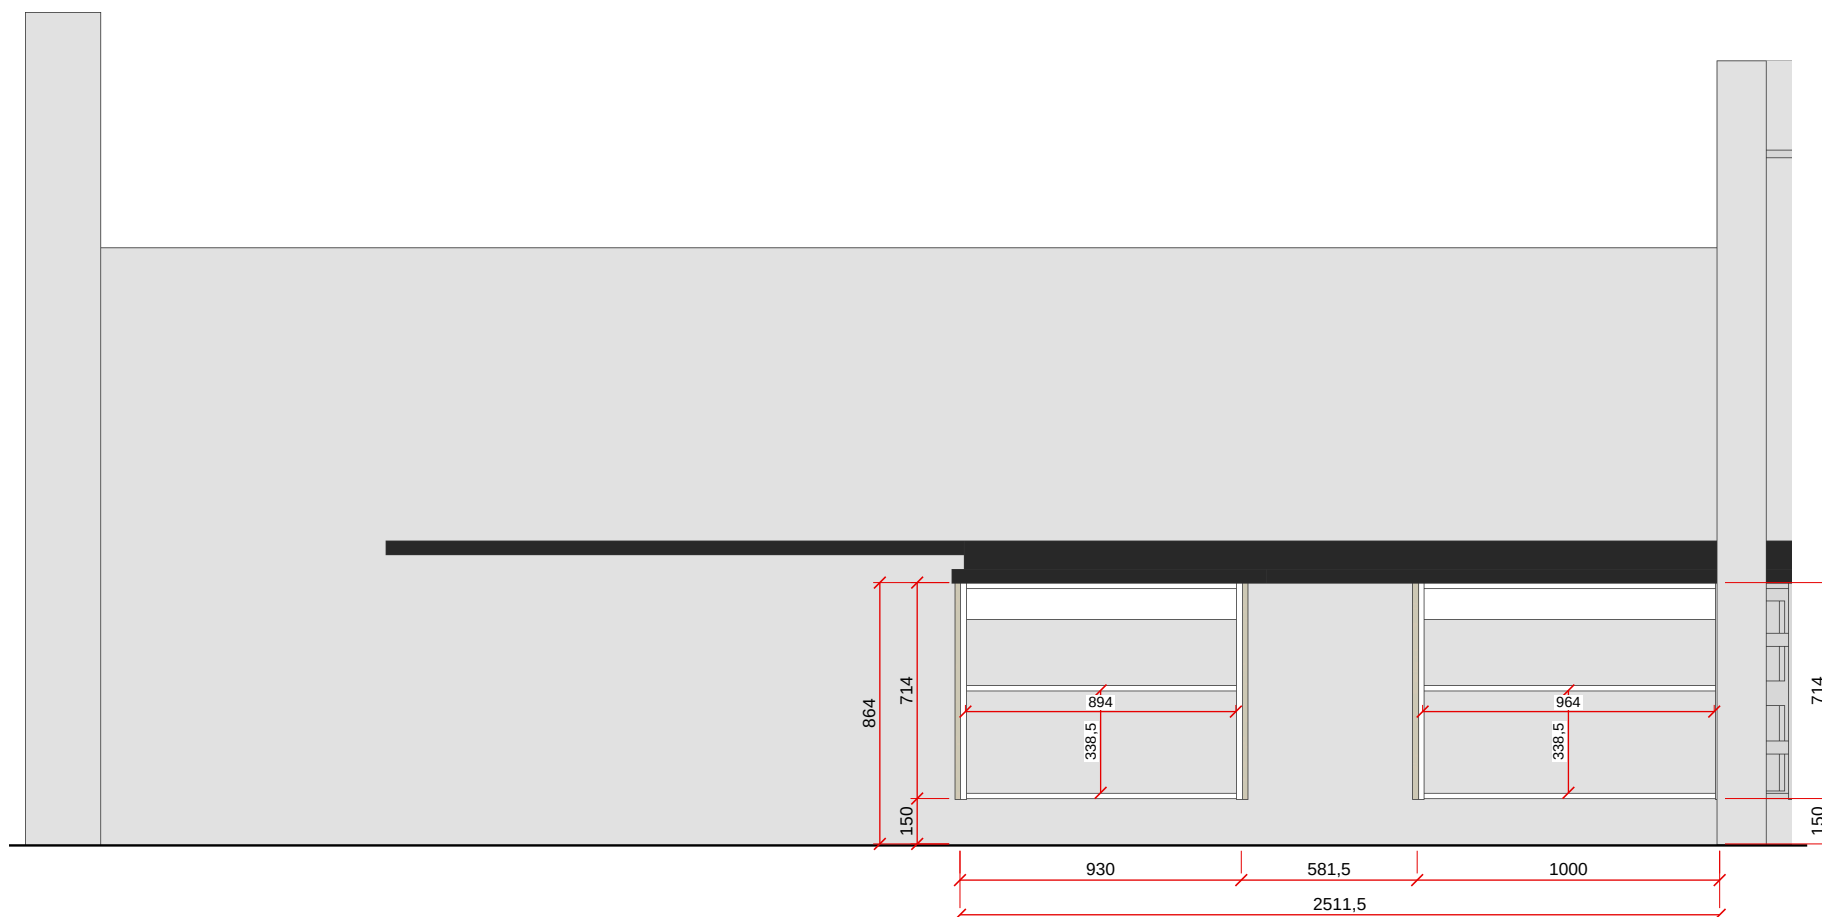

VISTA C - ESC. 1:25



CLIENTE: **PRISCILA**

AMBIENTE: **Cozinha**

PROJETISTA TÉCNICO: **JOÃO FELIPE SANTOS**

ARQUITETA: **FERNANDA**

ATENÇÃO:

DECLARO ESTAR DE ACORDO COM ESTE PROJETO E COM AS MEDIDAS NELE DESCRITAS E CIENTE DE QUE NELE CONSTAM APENAS PEÇAS E MÓDULOS DA EMPRESA, SENDO QUE OS DEMAIS ITENS SÃO MERAMENTE ILUSTRATIVOS (TAIS COMO ELETROS, COLCHÕES, GRANITOS E DECORAÇÕES NO GERAL).

ASS.: _____

**PRANCHA
15**

MÓDULOS E PAINÉIS - PAINEL COM NICHOS

Item	Descrição	Dimensão
1	Painel Freijo Puro MDF	1320x6x380
2	Painel Freijo Puro MDF	1530x15x625
3	Painel Freijo Puro MDF	1580x25x120
4	Painel Freijo Puro MDF	1907x15x625
5	Painel Freijo Puro MDF	605x25x100
6	Tamponamento Inferior	350x15x90
7	Tamponamento Inferior	1320x15x90





CLIENTE: **PRISCILA**

AMBIENTE: **Cozinha**

PROJETISTA TÉCNICO: **JOÃO FELIPE SANTOS**

ARQUITETA: **FERNANDA**

ATENÇÃO:


DECLARO ESTAR DE ACORDO COM ESTE PROJETO E COM AS MEDIDAS NELE DESCRITAS E CIENTE DE QUE NELE CONSTAM APENAS PEÇAS E MÓDULOS DA EMPRESA, SENDO QUE OS DEMAIS ITENS SÃO MERAMENTE ILUSTRATIVOS (TAIS COMO ELETROS, COLCHÕES, GRANITOS E DECORAÇÕES NO GERAL).

ASS.: _____

**PRANCHA
16**

MÓDULOS E PAINÉIS - PAINEL COM NICHOS

Item	Descrição	Dimensão
1	Painel Freijo Puro MDF	1530x15x625
2	Painel Freijo Puro MDF	1580x25x120
3	Painel Freijo Puro MDF	1907x15x625
4	Painel Freijo Puro MDF	605x25x100
5	Tamponamento Inferior	1320x15x90

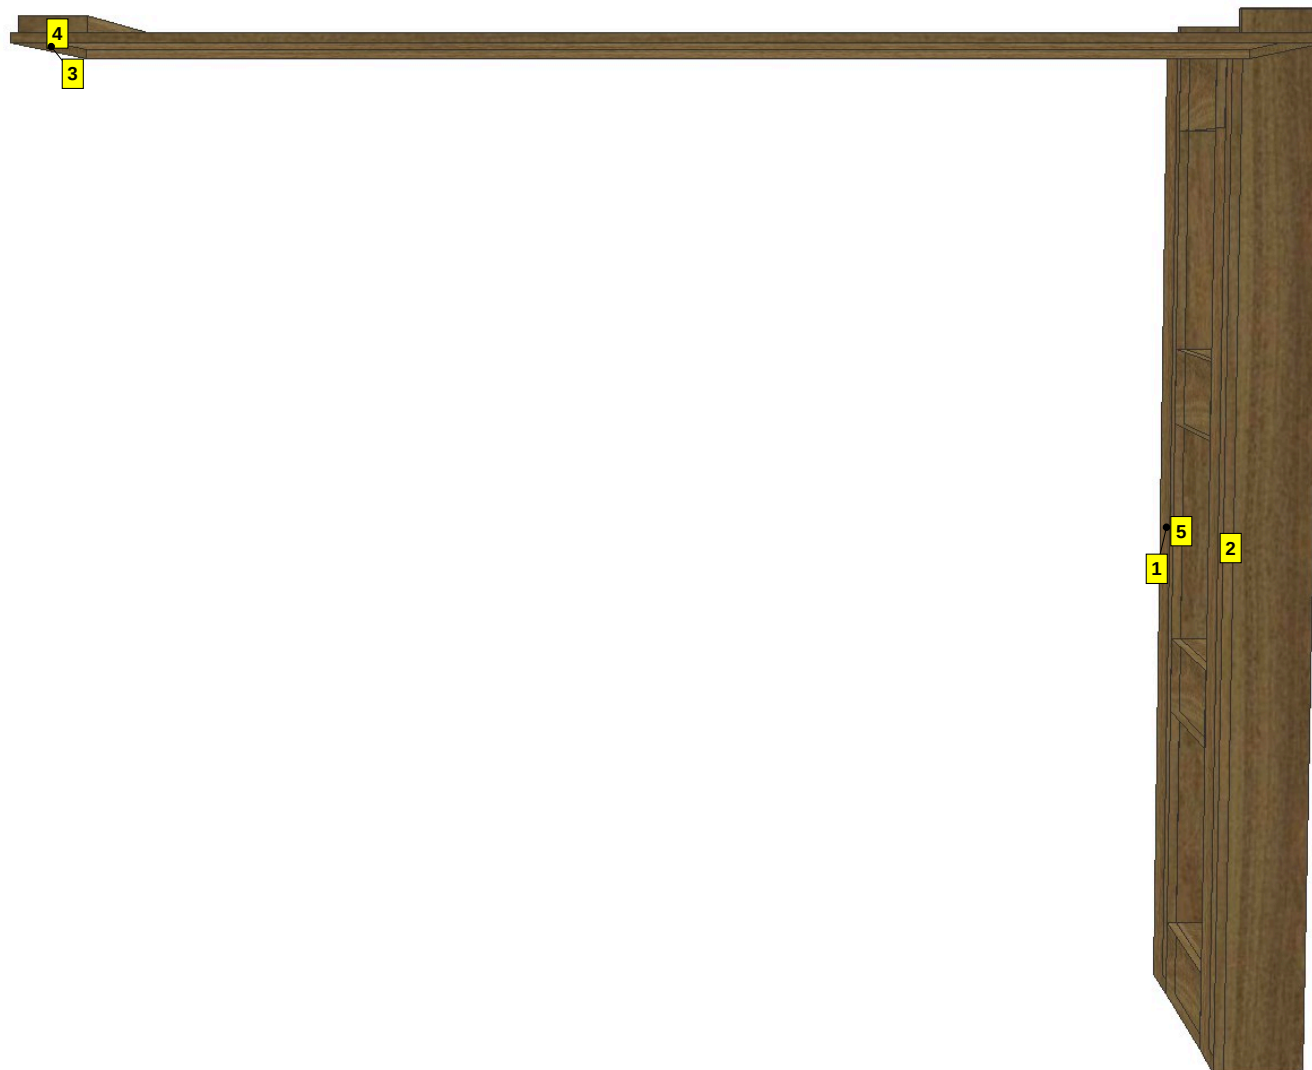



CLIENTE: **PRISCILA**

AMBIENTE: **Cozinha**

PROJETISTA TÉCNICO: **JOÃO FELIPE SANTOS**

ARQUITETA: **FERNANDA**

ATENÇÃO:

DECLARO ESTAR DE ACORDO COM ESTE PROJETO E COM AS MEDIDAS NELE DESCRITAS E CIENTE DE QUE NELE CONSTAM APENAS PEÇAS E MÓDULOS DA EMPRESA, SENDO QUE OS DEMAIS ITENS SÃO MERAMENTE ILUSTRATIVOS (TAIS COMO ELETROS, COLCHÕES, GRANITOS E DECORAÇÕES NO GERAL).

ASS.: _____

**PRANCHA
17**

MEDIDAS E ALTURAS - PAINEL COM NICHOS



PAINEL COM NICHOS - ESC. 1:25



CLIENTE: **PRISCILA**

AMBIENTE: **Cozinha**

PROJETISTA TÉCNICO: **JOÃO FELIPE SANTOS**

ARQUITETA: **FERNANDA**



ATENÇÃO:
DECLARO ESTAR DE ACORDO COM ESTE PROJETO E COM AS MEDIDAS NELE DESCRITAS E CIENTE DE QUE NELE CONSTAM APENAS PEÇAS E MÓDULOS DA EMPRESA , SENDO QUE OS DEMAIS ITENS SÃO MERAMENTE ILUSTRATIVOS (TAIS COMO ELETROS, COLCHÕES, GRANITOS E DECORAÇÕES NO GERAL).

ASS.: _____

PRANCHA
18

DIVISOR DE GAVETA

Item	Descrição	Dimensão
1	Painel Freijo Puro MDF	708x15x70
2	Painel Freijo Puro MDF	297x15x70
3	Painel Freijo Puro MDF	462x15x70

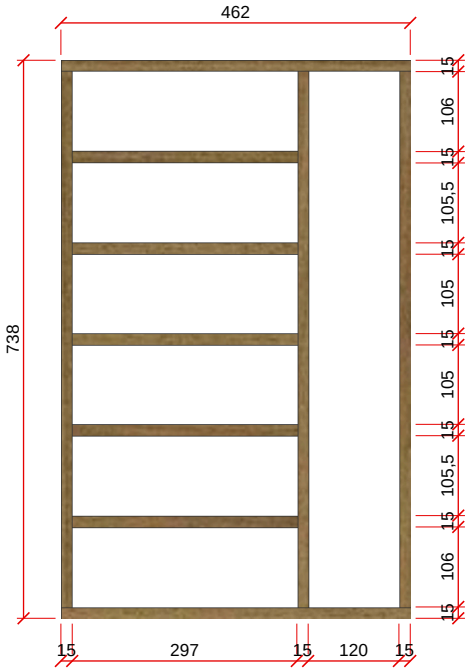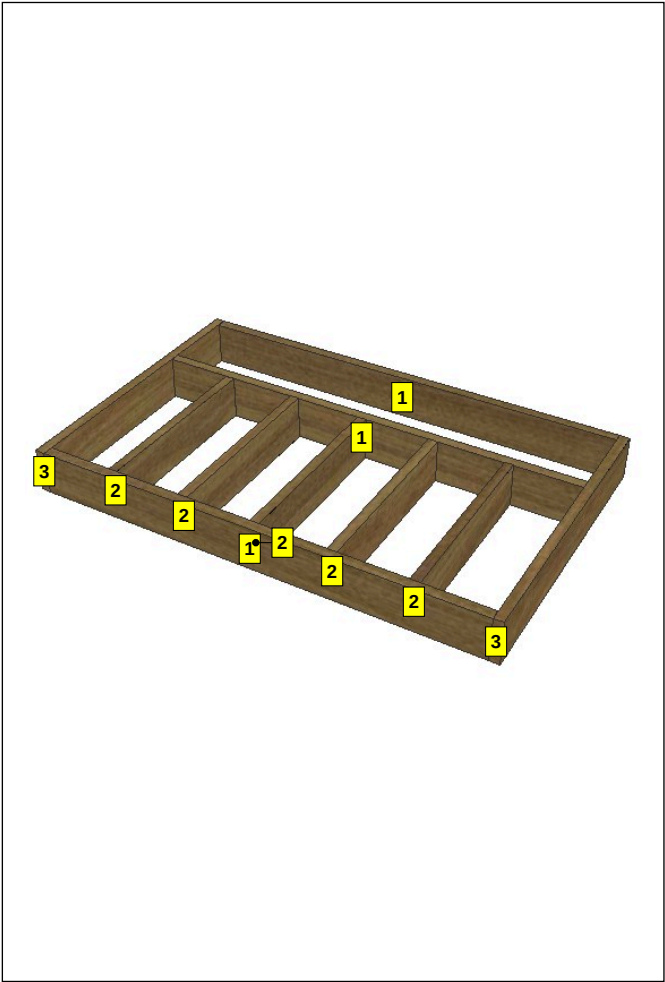

DIVISOR - VISTA DE CIMA - ESC. 1:10 | ALTURA: 70 mm