



RAFAEL CLARET

EXECUTIVO - COZINHA 2



CLIENTE: **RAFAEL CLARET**

AMBIENTE: **Cozinha 2**

PROJETISTA TÉCNICO: **JOÃO FELIPE SANTOS**

ARQUITETA: **FERNANDA**

ATENÇÃO:

DECLARO ESTAR DE ACORDO COM ESTE PROJETO E COM AS MEDIDAS NELE DESCRITAS E CIENTE DE QUE NELE CONSTAM APENAS PEÇAS E MÓDULOS DA EMPRESA, SENDO QUE OS DEMAIS ITENS SÃO MERAMENTE ILUSTRATIVOS (TAIS COMO ELETROS, COLCHÕES, GRANITOS E DECORAÇÕES NO GERAL).

ASS: _____

**PRANCHA
02**

CONTRATO

LEIA COM ATENÇÃO

1- CLIENTE ESTÁ RECEBENDO UMA CÓPIA DOS PROJETOS ADQUIRIDOS E ESTÁ DE ACORDO COM AS INFORMAÇÕES APONTADAS SOBRE MODELO, COR, ACABAMENTO, ESTRUTURAS, ACESSÓRIOS E CONDIÇÕES QUE FAZEM PARTE DESTES PROJETOS EXECUTIVOS.

2- O MESMO FOI ELABORADO CONSIDERANDO AS MEDIDAS REAIS DESTES AMBIENTES, SE HOUVER ALGUMA ALTERAÇÃO NO PÉ DIREITO OU NAS PAREDES, REFERENTE À INSTALAÇÃO DE MOLDURAS DE GESSO, RODAPÉS, MODIFICAÇÃO EM INSTALAÇÃO DA MODULAÇÃO NO DIA DA MONTAGEM, A EMPRESA NÃO SE RESPONSABILIZA QUANTO A FUTUROS CONTRATEMPOS DEVIDOS ÀS ALTERAÇÕES. CABE AO CLIENTE AVISAR O PROJETISTA ANTES DA MEDIÇÃO FINAL PARA ADEQUAÇÃO DA MODULAÇÃO.

3- SE HOUVER GRANITO NOS AMBIENTES, A MEDIÇÃO FINAL SE DARÁ APÓS A CONCLUSÃO DA INSTALAÇÃO DOS MESMOS, OU INSTALAR APÓS A MONTAGEM DOS MÓVEIS.

4- SE HOUVER REDUÇÃO OU RECORTES NOS MÓDULOS, O CLIENTE TOMA CIÊNCIA QUE OS AJUSTES SERÃO EXECUTADOS NO LOCAL, QUE DEVE ESTAR LIVRE DE OBJETOS E PESSOAS QUE POSSAM SOFRER DE ALGUMA MANEIRA COM O PÓ DECORRENTE DESSES AJUSTES E QUALQUER OBJETO QUE NÃO POSSA SER RETIRADO DEVE ESTAR DEVIDAMENTE COBERTO. POR NÃO POSSUIR PROFISSIONÁIS ESPECIALIZADOS EM INSTALAÇÕES DE ELETROS, INSTALAÇÕES HIDRÁULICAS, A EMPRESA NÃO EFETUARÁ ESSE TIPO DE SERVIÇO. É NECESSÁRIO FORNECER AS PLANTAS DE INSTALAÇÃO ELÉTRICA E HIDRÁULICA DOS AMBIENTES NO DIA DA MONTAGEM, É NECESSÁRIO O ACOMPANHAMENTO DO CLIENTE OU UM RESPONSÁVEL PELA OBRA, MAIOR QUE 18 ANOS PARA TIRAR EVENTUAIS DÚVIDAS DOS MONTADORES REFERENTE AOS LOCAIS ONDE É POSSÍVEL FAZER FURAÇÕES. A ASSINATURA DESSE PROJETO SUBSTITUI QUALQUER PROJETO ANTERIOR.

5- O CLIENTE DECLARA ESTAR CIENTE QUE CASO O PROJETO ENVOLVA ELETROS, OS MESMOS DEVERÃO ESTAR NO LOCAL NO DIA DA MONTAGEM PARA ADEQUAÇÃO DOS NICHOS NECESSÁRIOS, E SE NÃO COMPROU OS ELETROS, SE RESPONSABILIZA EM ADQUIRIR OS MESMOS DENTRO DAS MEDIDAS ESPECIFICADAS NESTE PROJETO.

6- DECLARO ESTAR DE ACORDO COM ESTE PROJETO E COM AS MEDIDAS NELE DESCRITAS E CIENTE DE QUE NELE CONSTAM APENAS PEÇAS E MÓDULOS DA EMPRESA DUO PLANEJADOS, SENDO QUE OS DEMAIS ITENS SÃO MERAMENTE ILUSTRATIVOS (TAIS COMO ELETROS, COLCHÕES, GRANITOS E DECORAÇÕES EM GERAL).



CLIENTE: **RAFAEL CLARET**

AMBIENTE: **Cozinha 2**

PROJETISTA TÉCNICO: **JOÃO FELIPE SANTOS**

ARQUITETA: **FERNANDA**

ATENÇÃO:

DECLARO ESTAR DE ACORDO COM ESTE PROJETO E COM AS MEDIDAS NELE DESCRITAS E CIENTE DE QUE NELE CONSTAM APENAS PEÇAS E MÓDULOS DA EMPRESA, SENDO QUE OS DEMAIS ITENS SÃO MERAMENTE ILUSTRATIVOS (TAIS COMO ELETROS, COLCHÕES, GRANITOS E DECORAÇÕES NO GERAL).

ASS: _____

**PRANCHA
03**

PLANTA - ESPECIFICAÇÕES DO PROJETO

ESPECIFICAÇÕES DO PROJETO

CORES E ACABAMENTOS:

Caixa Módulos (Interno): **Branco, Pecan, Freijo Puro**

Portas e Frentes: **Pecan**

Tamponamentos: **Freijo Puro, Pecan**

Painéis e Tampos: **Freijo Puro, Pecan**

Puxadores: **Fosco**

Portas de Vidro:

FERRAGENS E ACESSÓRIOS:

Dobradiças:

Dobradiça Reta c/ Amortecedor, Dobradiça p/ Canto L c/ Amortecedor, Dobradiça Super Curva c/ Amortecedor

Corrediças:

Gaveta Corrediça Invisível, Kit Corrediça Invisível 500mm

Puxadores:

Puxador Linear (15, 18 e 20mm) Pino Fosco - 150mm

Ferragens especiais:

ESPESSURAS:


Caixa Módulos (Interno): **18mm (fundo 6mm)**

Prateleiras internas: **18mm**

Portas e Frentes: **18mm**

Tamponamentos: **18mm**

Painéis e Tampos e perfil: **18mm**

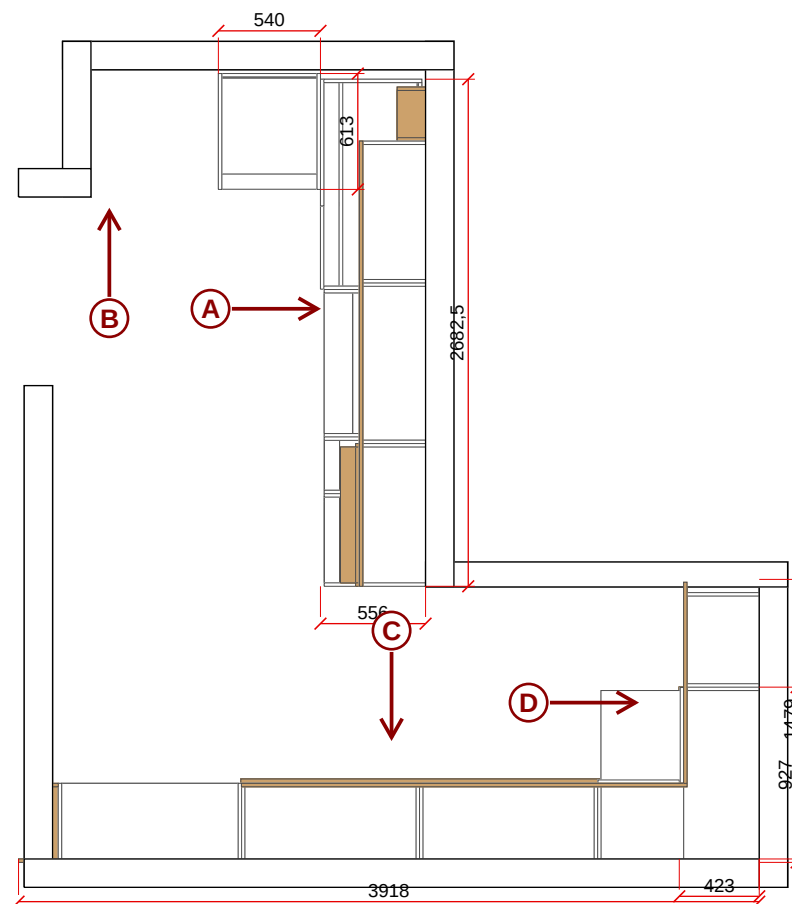

PLANTA BAIXA - ESC. 1:40



CLIENTE: **RAFAEL CLARET**

AMBIENTE: **Cozinha 2**

PROJETISTA TÉCNICO: **JOÃO FELIPE SANTOS**

ARQUITETA: **FERNANDA**

ATENÇÃO:

DECLARO ESTAR DE ACORDO COM ESTE PROJETO E COM AS MEDIDAS NELE DESCRITAS E CIENTE DE QUE NELE CONSTAM APENAS PEÇAS E MÓDULOS DA EMPRESA, SENDO QUE OS DEMAIS ITENS SÃO MERAMENTE ILUSTRATIVOS (TAIS COMO ELETROS, COLCHÕES, GRANITOS E DECORAÇÕES NO GERAL).

ASS.: _____

**PRANCHA
04**

VISÃO GERAL DOS MÓVEIS


VISTA A



VISTA B



VISTA C

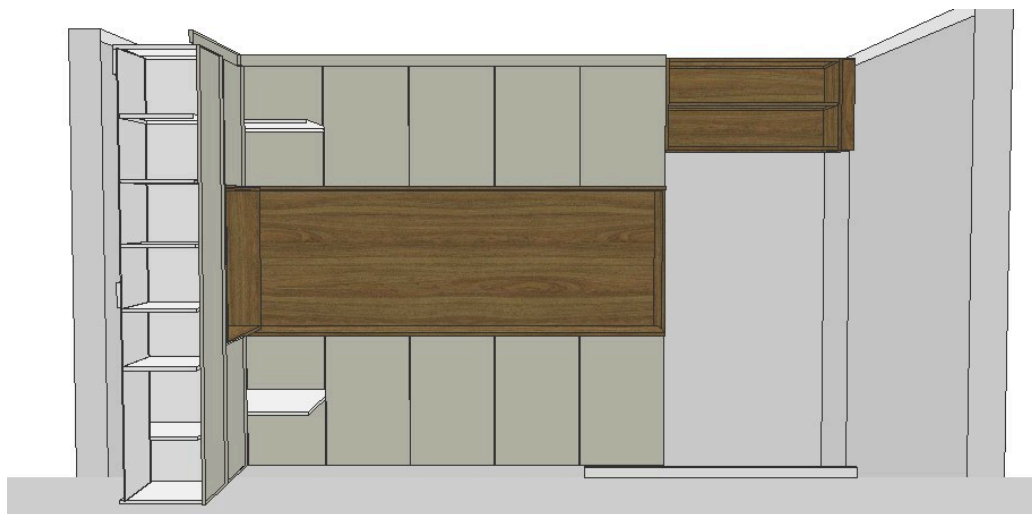

VISTA D





CLIENTE: **RAFAEL CLARET**

AMBIENTE: **Cozinha 2**

PROJETISTA TÉCNICO: **JOÃO FELIPE SANTOS**

ARQUITETA: **FERNANDA**

ATENÇÃO:

DECLARO ESTAR DE ACORDO COM ESTE PROJETO E COM AS MEDIDAS NELE DESCRITAS E CIENTE DE QUE NELE CONSTAM APENAS PEÇAS E MÓDULOS DA EMPRESA, SENDO QUE OS DEMAIS ITENS SÃO MERAMENTE ILUSTRATIVOS (TAIS COMO ELETROS, COLCHÕES, GRANITOS E DECORAÇÕES NO GERAL).



ASS.: _____

**PRANCHA
05**

MÓDULOS E PAINÉIS - VISTA A - SUPERIORES

Item	Descrição	Dimensão
1	Armário 1 Portas Basculantes	755x460x350
2	Armário 2 Portas	750x660x350
3	Armário 2 Portas	850x660x350
4	Painel Freijo Puro MDF	250x18x568
5	Painel Freijo Puro MDF	1000x18x178
6	Painel Freijo Puro MDF	400x18x370
7	Painel Freijo Puro MDF	719x18x364
8	Painel Freijo Puro MDF	719x18x450
9	Painel Freijo Puro MDF	719x18x370
10	Painel Freijo Puro MDF	250x18x132
11	Painel Freijo Puro MDF	586x18x150
12	Painel Freijo Puro MDF	800x18x150
13	Painel Freijo Puro MDF	250x18x150
14	Painel Freijo Puro MDF	1000x18x150
15	Painel Freijo Puro MDF	214x18x150
16	Vista	2355x18x60

DETALHE - NICHOS

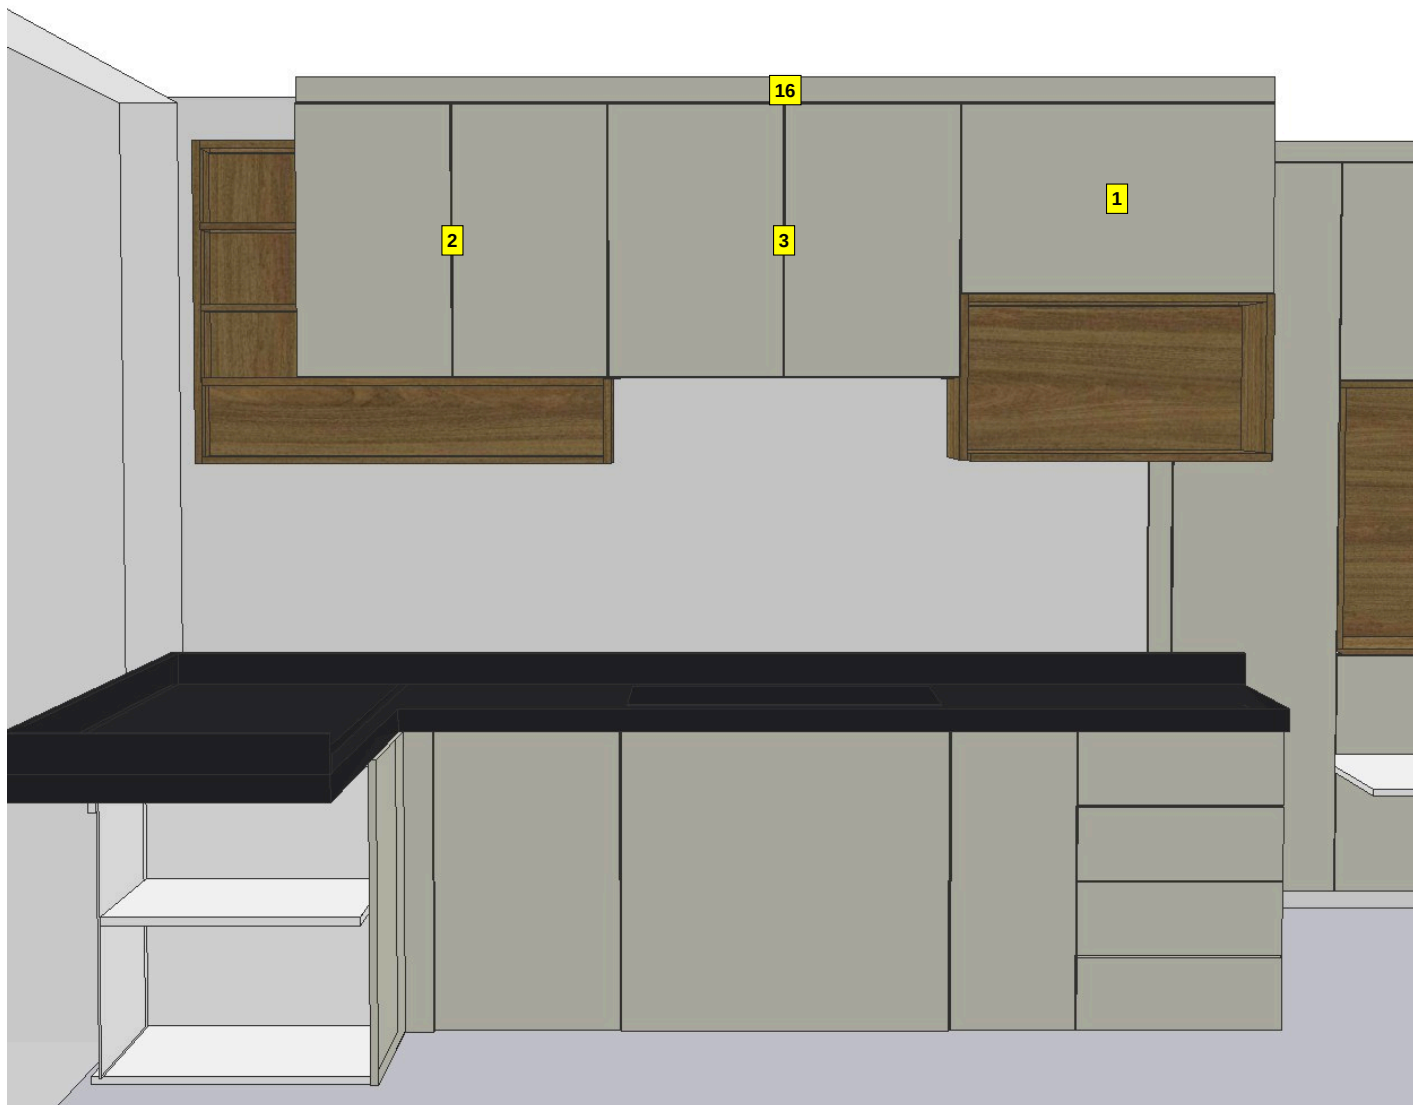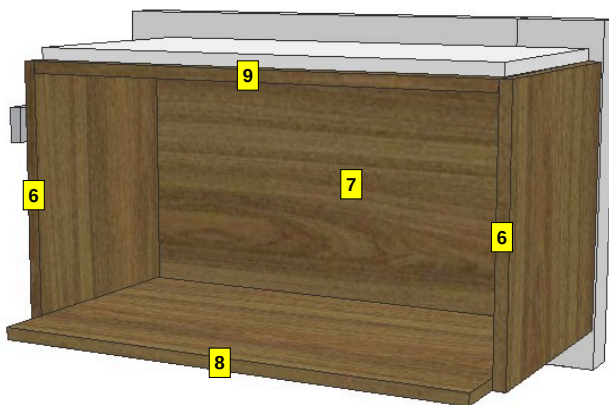



CLIENTE: **RAFAEL CLARET**

AMBIENTE: **Cozinha 2**

PROJETISTA TÉCNICO: **JOÃO FELIPE SANTOS**

ARQUITETA: **FERNANDA**

ATENÇÃO:

DECLARO ESTAR DE ACORDO COM ESTE PROJETO E COM AS MEDIDAS NELE DESCRITAS E CIENTE DE QUE NELE CONSTAM APENAS PEÇAS E MÓDULOS DA EMPRESA, SENDO QUE OS DE MAIS ITENS SÃO MERAMENTE ILUSTRATIVOS (TAIS COMO ELETROS, COLCHÕES, GRANITOS E DECORAÇÕES NO GERAL).



ASS.: _____

**PRANCHA
06**

MÓDULOS E PAINÉIS - VISTA A - SUPERIORES - DETALHE 1

Item	Descrição	Dimensão
4	Painel Freijo Puro MDF	250x18x568
5	Painel Freijo Puro MDF	1000x18x178
10	Painel Freijo Puro MDF	250x18x132
11	Painel Freijo Puro MDF	586x18x150
12	Painel Freijo Puro MDF	800x18x150
13	Painel Freijo Puro MDF	250x18x150
14	Painel Freijo Puro MDF	1000x18x150
15	Painel Freijo Puro MDF	214x18x150

DETALHE - NICHOS

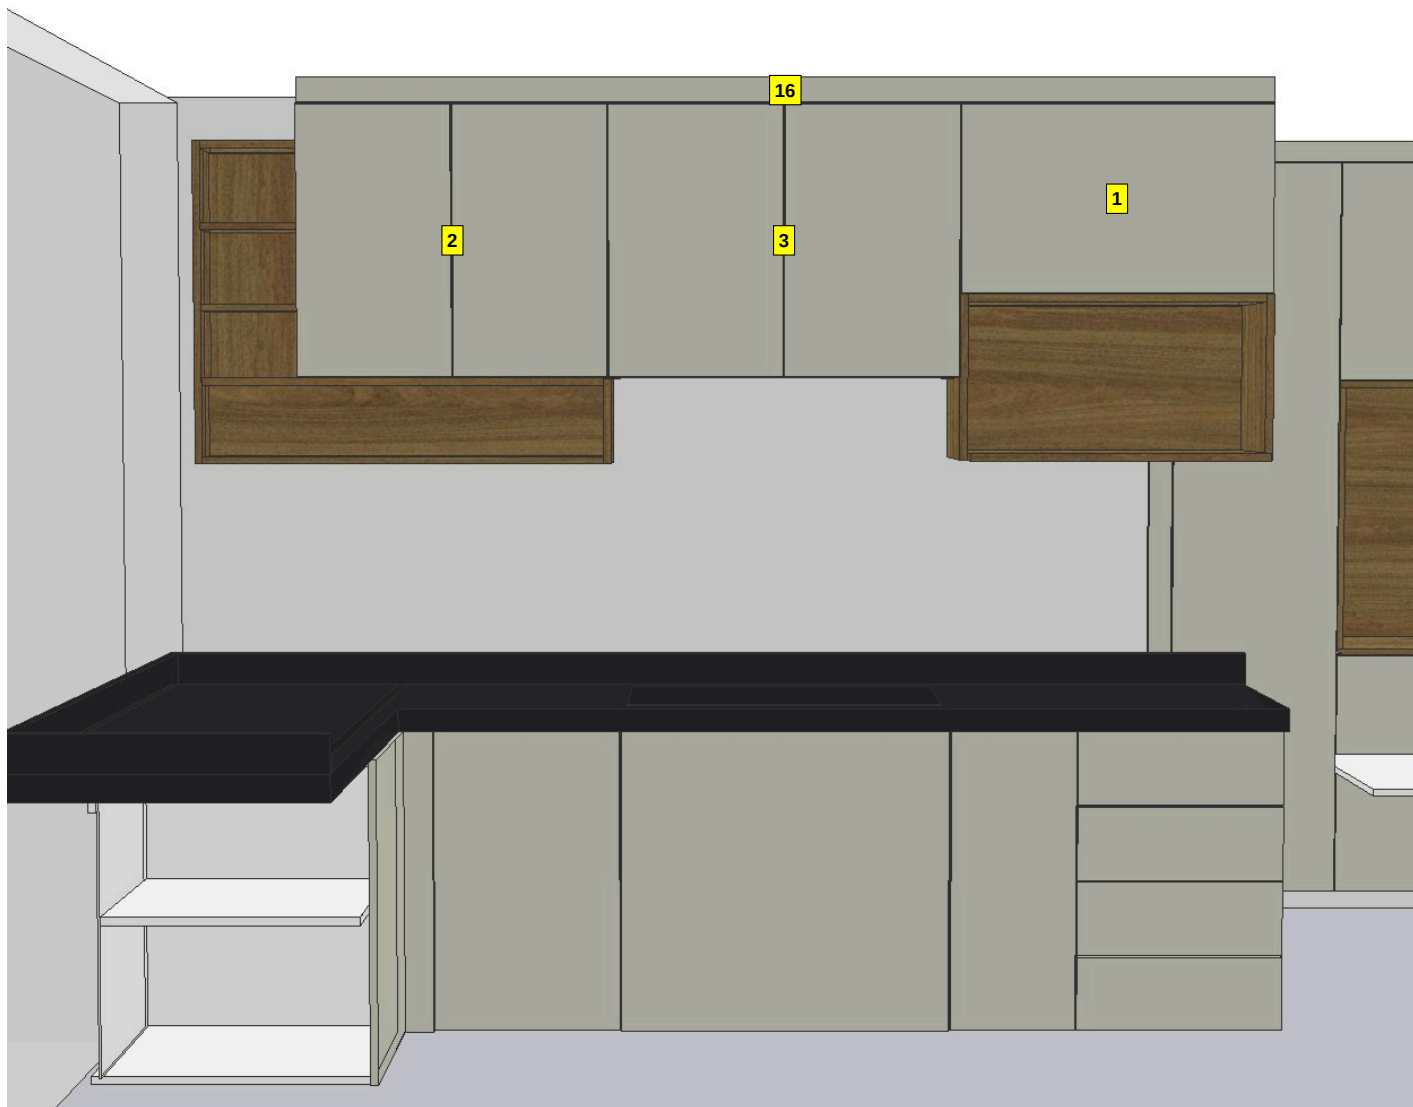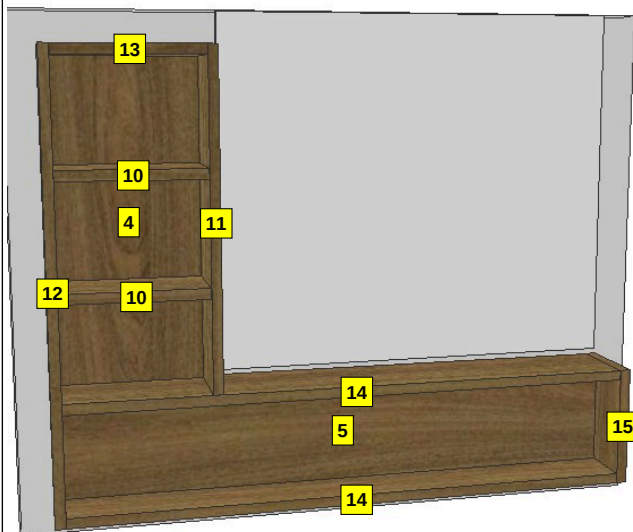



CLIENTE: **RAFAEL CLARET**

AMBIENTE: **Cozinha 2**

PROJETISTA TÉCNICO: **JOÃO FELIPE SANTOS**

ARQUITETA: **FERNANDA**

ATENÇÃO:


DECLARO ESTAR DE ACORDO COM ESTE PROJETO E COM AS MEDIDAS NELE DESCRITAS E CIENTE DE QUE NELE CONSTAM APENAS PEÇAS E MÓDULOS DA EMPRESA, SENDO QUE OS DEMAIS ITENS SÃO MERAMENTE ILUSTRATIVOS (TAIS COMO ELETROS, COLCHÕES, GRANITOS E DECORAÇÕES NO GERAL).

ASS.: _____

**PRANCHA
07**

MÓDULOS E PAINÉIS - VISTA A - INFERIORES

Item	Descrição	Dimensão
1	Balcão 1 Porta	300x720x536
2	Balcão 4 Gavetas	490x720x536
3	Balcão Canto Reto Esquerdo	1142,5x720x606
4	Balcão p/ Forno	780x720x536

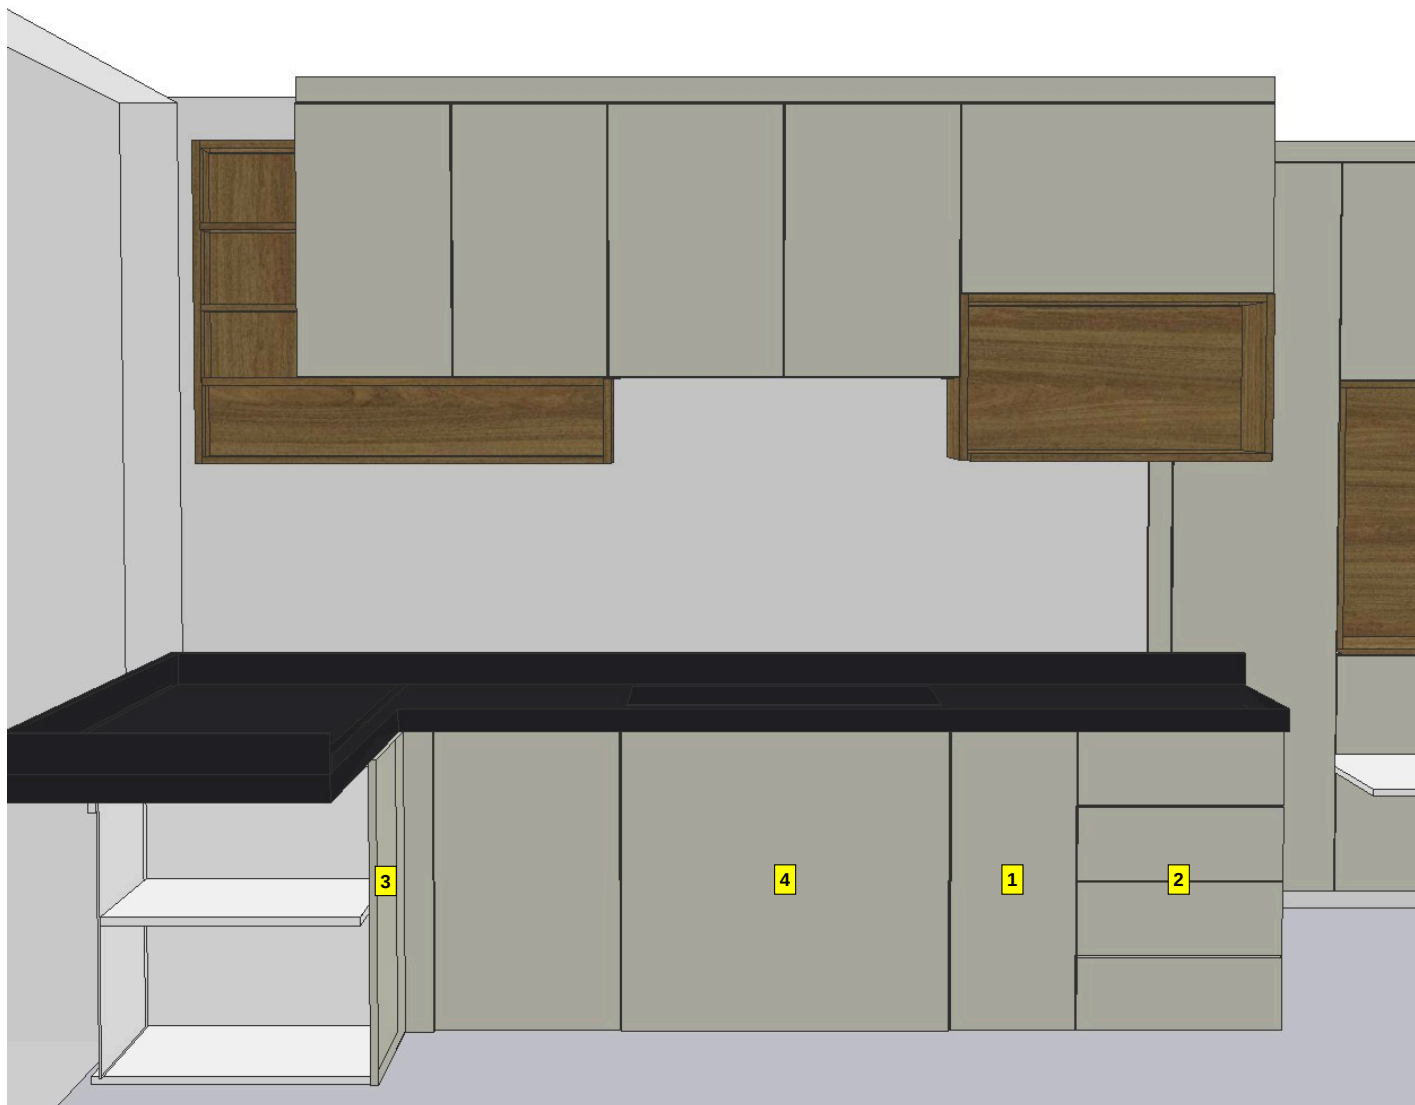



CLIENTE: **RAFAEL CLARET**

AMBIENTE: **Cozinha 2**

PROJETISTA TÉCNICO: **JOÃO FELIPE SANTOS**

ARQUITETA: **FERNANDA**

ATENÇÃO:

DECLARO ESTAR DE ACORDO COM ESTE PROJETO E COM AS MEDIDAS NELE DESCRITAS E CIENTE DE QUE NELE CONSTAM APENAS PEÇAS E MÓDULOS DA EMPRESA, SENDO QUE OS DEMAIS ITENS SÃO MERAMENTE ILUSTRATIVOS (TAIS COMO ELETROS, COLCHÕES, GRANITOS E DECORAÇÕES NO GERAL).


ASS.: _____

**PRANCHA
08**

MÓDULOS E PAINÉIS - VISTA A - INFERIORES - DETALHE 1

Item	Descrição	Dimensão
3	Balcão Canto Reto Esquerdo	1142,5x720x606

COMO FICA MONTADO

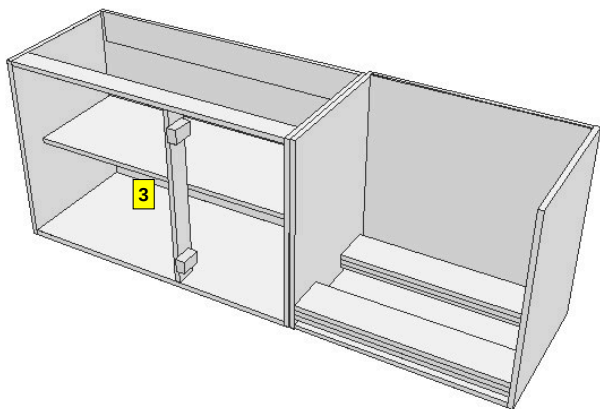



CLIENTE: **RAFAEL CLARET**

AMBIENTE: **Cozinha 2**

PROJETISTA TÉCNICO: **JOÃO FELIPE SANTOS**

ARQUITETA: **FERNANDA**

ATENÇÃO:


DECLARO ESTAR DE ACORDO COM ESTE PROJETO E COM AS MEDIDAS NELE DESCRITAS E CIENTE DE QUE NELE CONSTAM APENAS PEÇAS E MÓDULOS DA EMPRESA, SENDO QUE OS DEMAIS ITENS SÃO MERAMENTE ILUSTRATIVOS (TAIS COMO ELETROS, COLCHÕES, GRANITOS E DECORAÇÕES NO GERAL).

ASS:.. _____

PRANCHA
09

MÓDULOS E PAINÉIS - VISTA B

Item	Descrição	Dimensão
1	Balcão 1 Porta	540x720x613

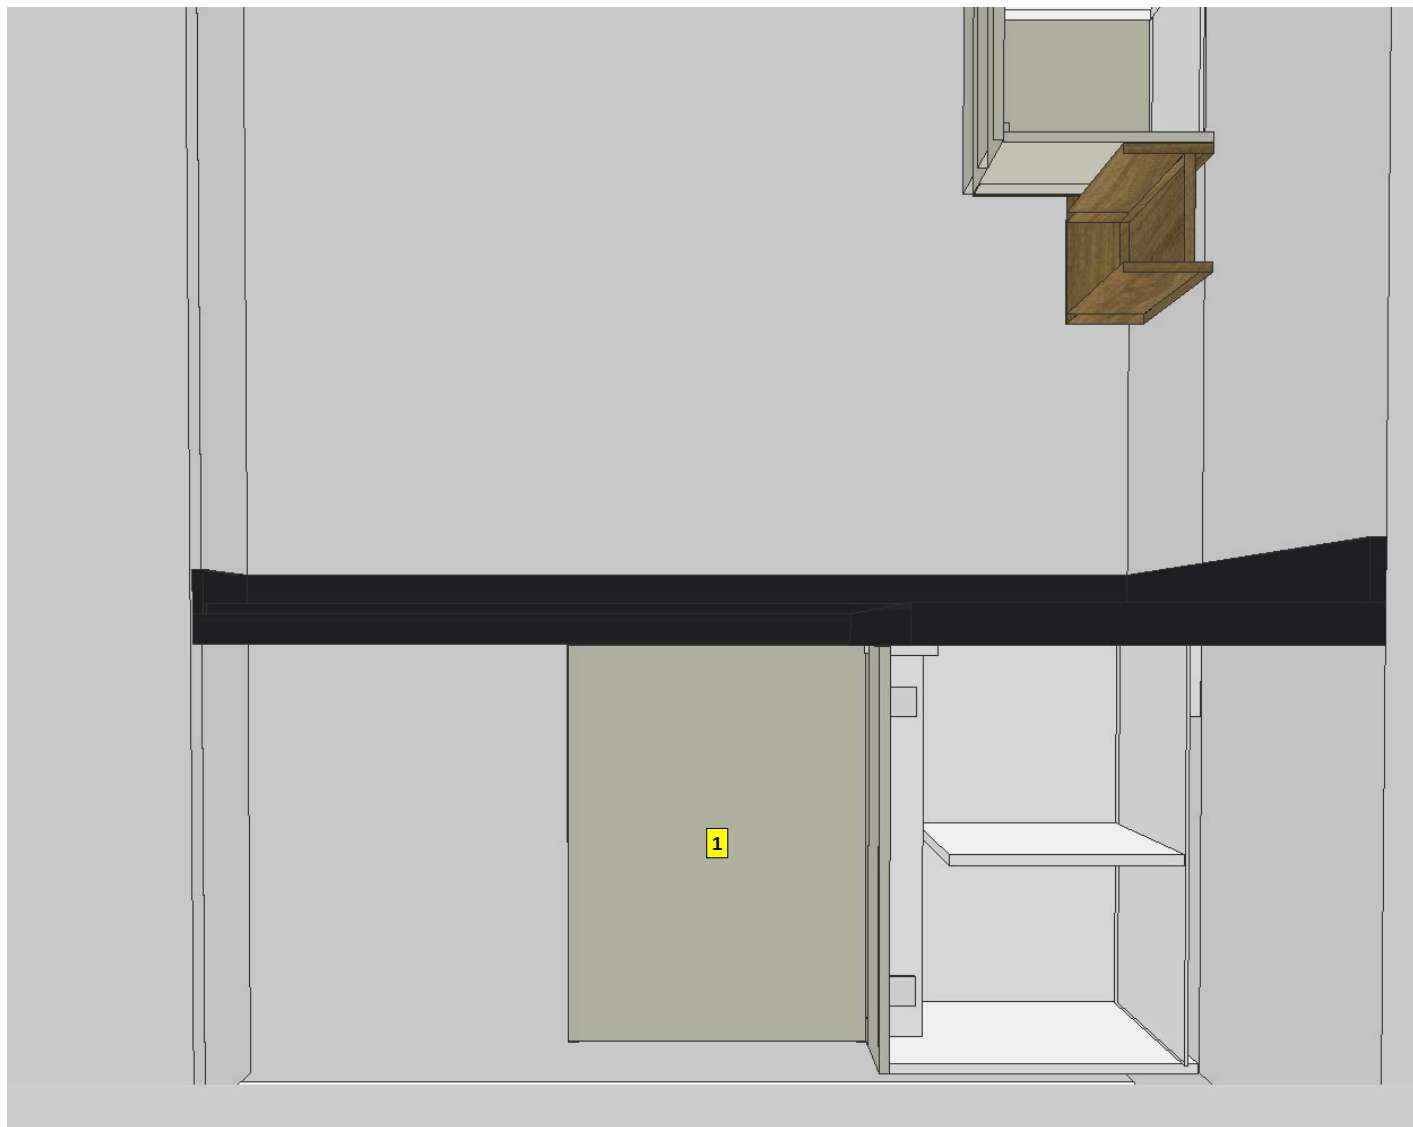



CLIENTE: **RAFAEL CLARET**

AMBIENTE: **Cozinha 2**

PROJETISTA TÉCNICO: **JOÃO FELIPE SANTOS**

ARQUITETA: **FERNANDA**


ATENÇÃO:

DECLARO ESTAR DE ACORDO COM ESTE PROJETO E COM AS MEDIDAS NELE DESCRITAS E CIENTE DE QUE NELE CONSTAM APENAS PEÇAS E MÓDULOS DA EMPRESA, SENDO QUE OS DEMAIS ITENS SÃO MERAMENTE ILUSTRATIVOS (TAIS COMO ELETROS, COLCHÕES, GRANITOS E DECORAÇÕES NO GERAL).


ASS.: _____

PRANCHA 10

MEDIDAS E ALTURAS - VISTAS A E B

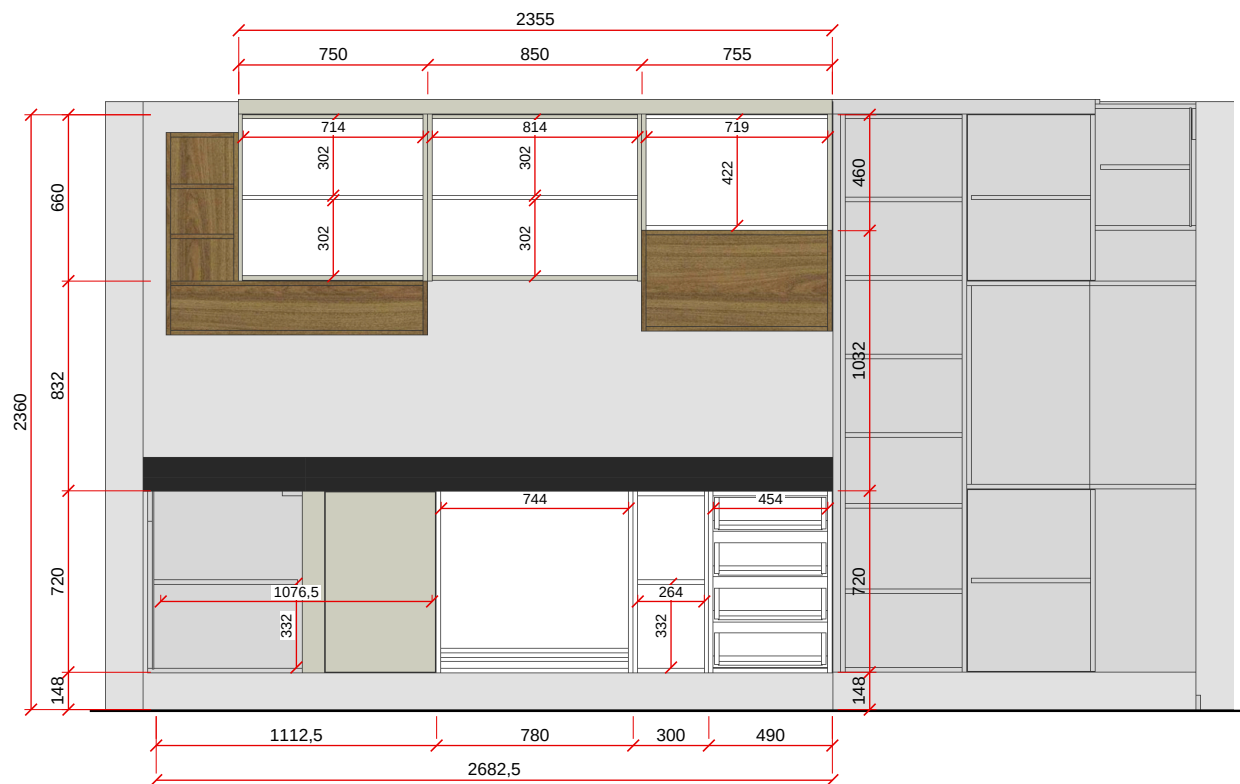

VISTA A - ESC. 1:30

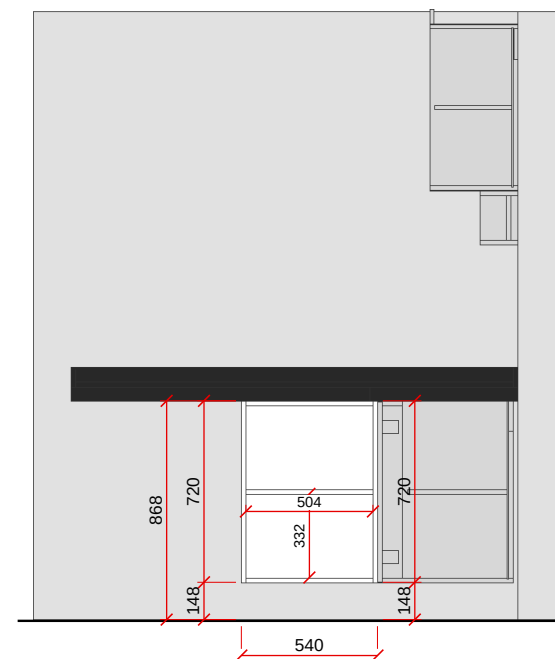

VISTA B - ESC. 1:30



CLIENTE: **RAFAEL CLARET**

AMBIENTE: **Cozinha 2**

PROJETISTA TÉCNICO: **JOÃO FELIPE SANTOS**

ARQUITETA: **FERNANDA**

ATENÇÃO:

DECLARO ESTAR DE ACORDO COM ESTE PROJETO E COM AS MEDIDAS NELE DESCRITAS E CIENTE DE QUE NELE CONSTAM APENAS PEÇAS E MÓDULOS DA EMPRESA, SENDO QUE OS DEMAIS ITENS SÃO MERAMENTE ILUSTRATIVOS (TAIS COMO ELETROS, COLCHÕES, GRANITOS E DECORAÇÕES NO GERAL).



ASS.: _____

PRANCHA 11

MÓDULOS E PAINÉIS - VISTA C

Item	Descrição	Dimensão
1	Armário 2 Portas	942x660x400
2	Armário 2 Portas	970x500x400
3	Armário Canto L Esquerdo	855x660x909
4	Balcão 2 Portas	942x725x400
5	Balcão Canto L Esquerdo	855x725x909
6	Painel Freijo Puro MDF	2319x18x423
7	Painel Freijo Puro MDF	405x18x789
8	Painel Freijo Puro MDF	2301x18x789
9	Tamponamento	382x18x70
10	Tamponamento	500x18x70
11	Tamponamento	789x18x423
12	Tamponamento	2319x18x423
13	Vista	1600x18x60
14	Vista	2357x18x60

DETALHE - NICHOS

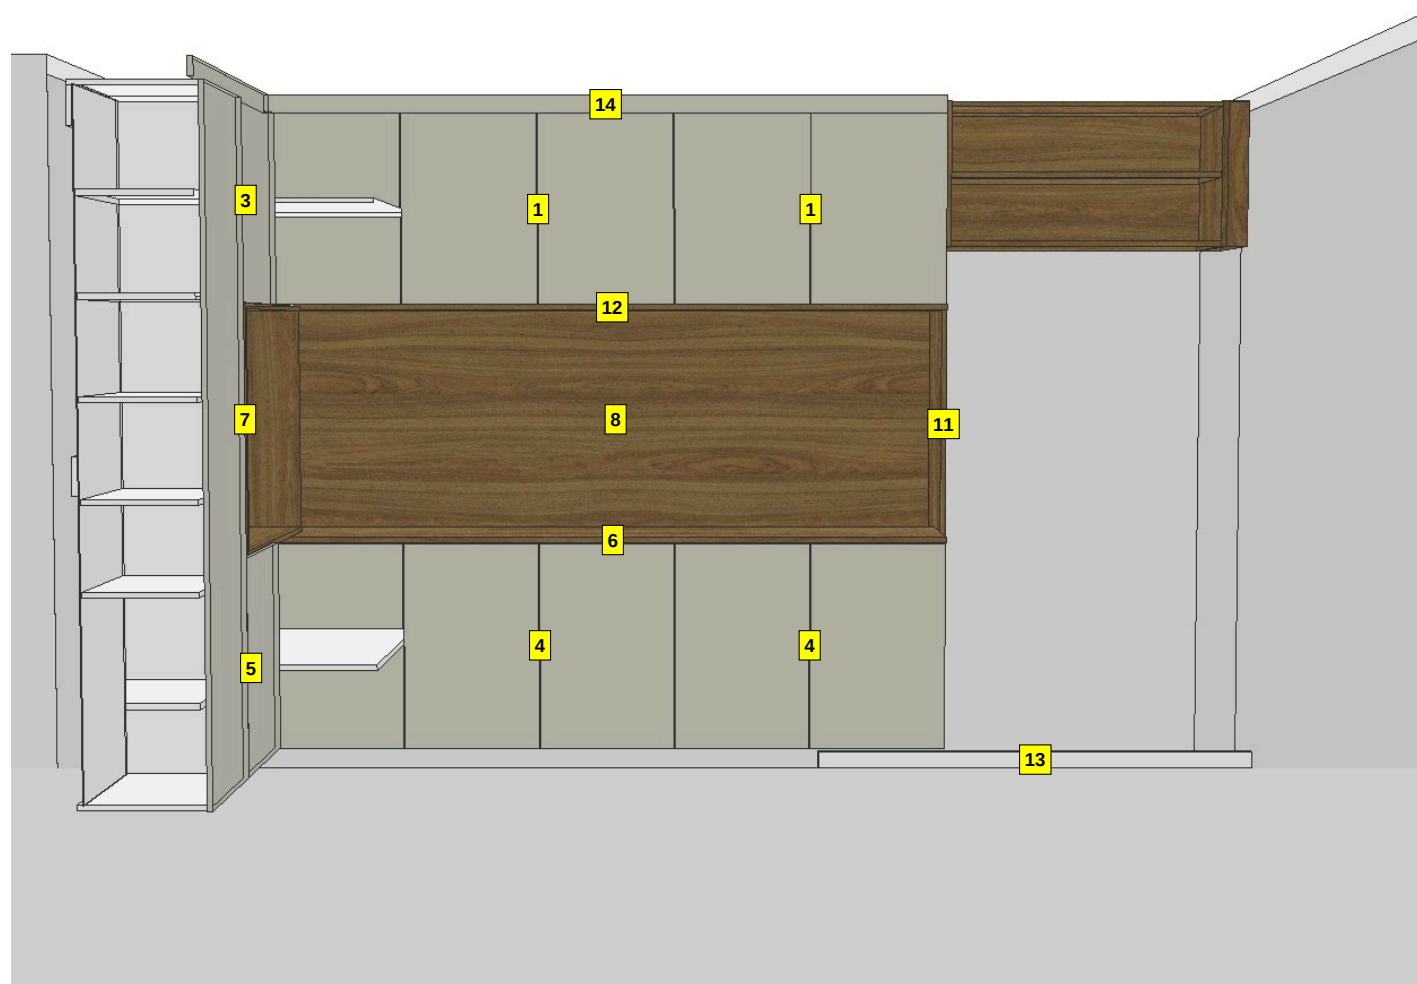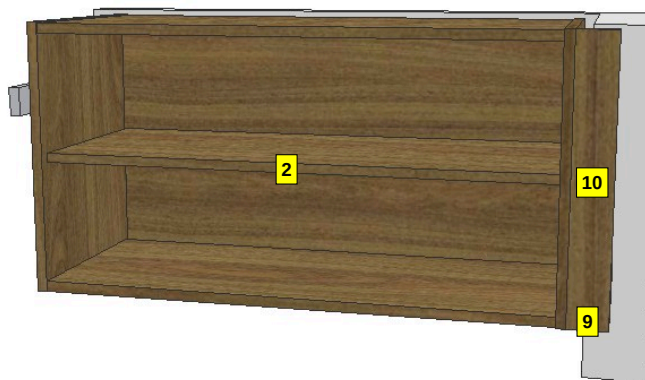



CLIENTE: **RAFAEL CLARET**

AMBIENTE: **Cozinha 2**

PROJETISTA TÉCNICO: **JOÃO FELIPE SANTOS**

ARQUITETA: **FERNANDA**

ATENÇÃO:

DECLARO ESTAR DE ACORDO COM ESTE PROJETO E COM AS MEDIDAS NELE DESCRITAS E CIENTE DE QUE NELE CONSTAM APENAS PEÇAS E MÓDULOS DA EMPRESA, SENDO QUE OS DEMAIS ITENS SÃO MERAMENTE ILUSTRATIVOS (TAIS COMO ELETROS, COLCHÕES, GRANITOS E DECORAÇÕES NO GERAL).



ASS.: _____

PRANCHA 12

MÓDULOS E PAINÉIS - VISTA C - DETALHE 1

Item	Descrição	Dimensão
3	Armário Canto L Esquerdo	855x660x909

COMO FICA MONTADO

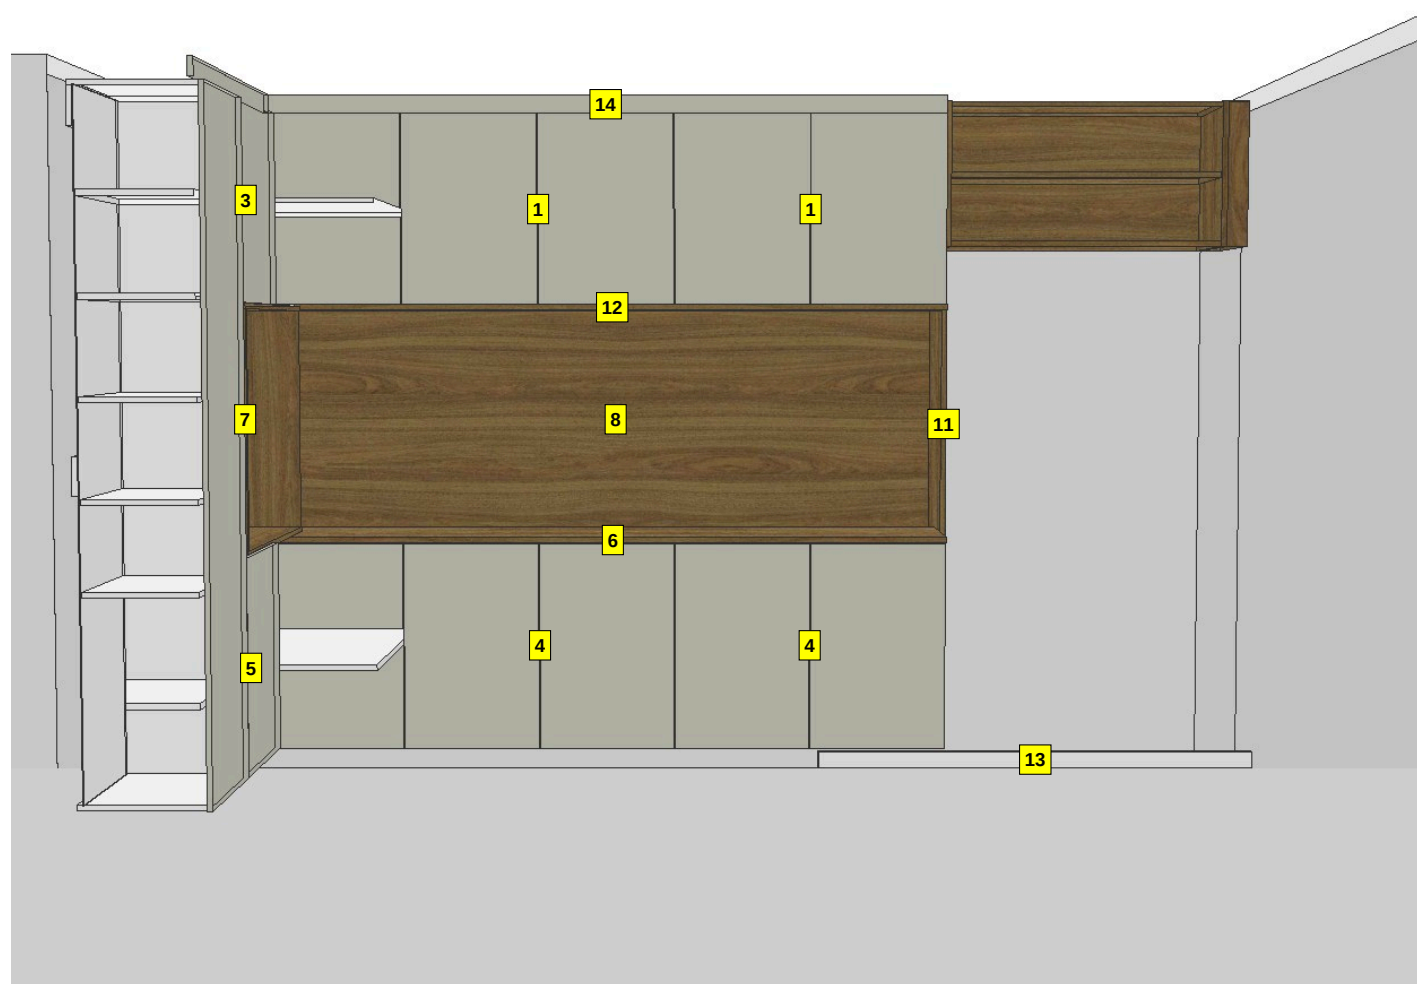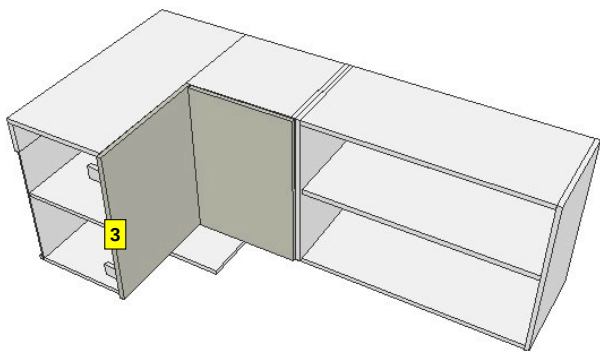



CLIENTE: **RAFAEL CLARET**

AMBIENTE: **Cozinha 2**

PROJETISTA TÉCNICO: **JOÃO FELIPE SANTOS**

ARQUITETA: **FERNANDA**

ATENÇÃO:

DECLARO ESTAR DE ACORDO COM ESTE PROJETO E COM AS MEDIDAS NELE DESCRITAS E CIENTE DE QUE NELE CONSTAM APENAS PEÇAS E MÓDULOS DA EMPRESA, SENDO QUE OS DEMAIS ITENS SÃO MERAMENTE ILUSTRATIVOS (TAIS COMO ELETROS, COLCHÕES, GRANITOS E DECORAÇÕES NO GERAL).



ASS.: _____

PRANCHA 13

MÓDULOS E PAINÉIS - VISTA C - DETALHE 2

Item	Descrição	Dimensão
5	Balcão Canto L Esquerdo	855x725x909

COMO FICA MONTADO

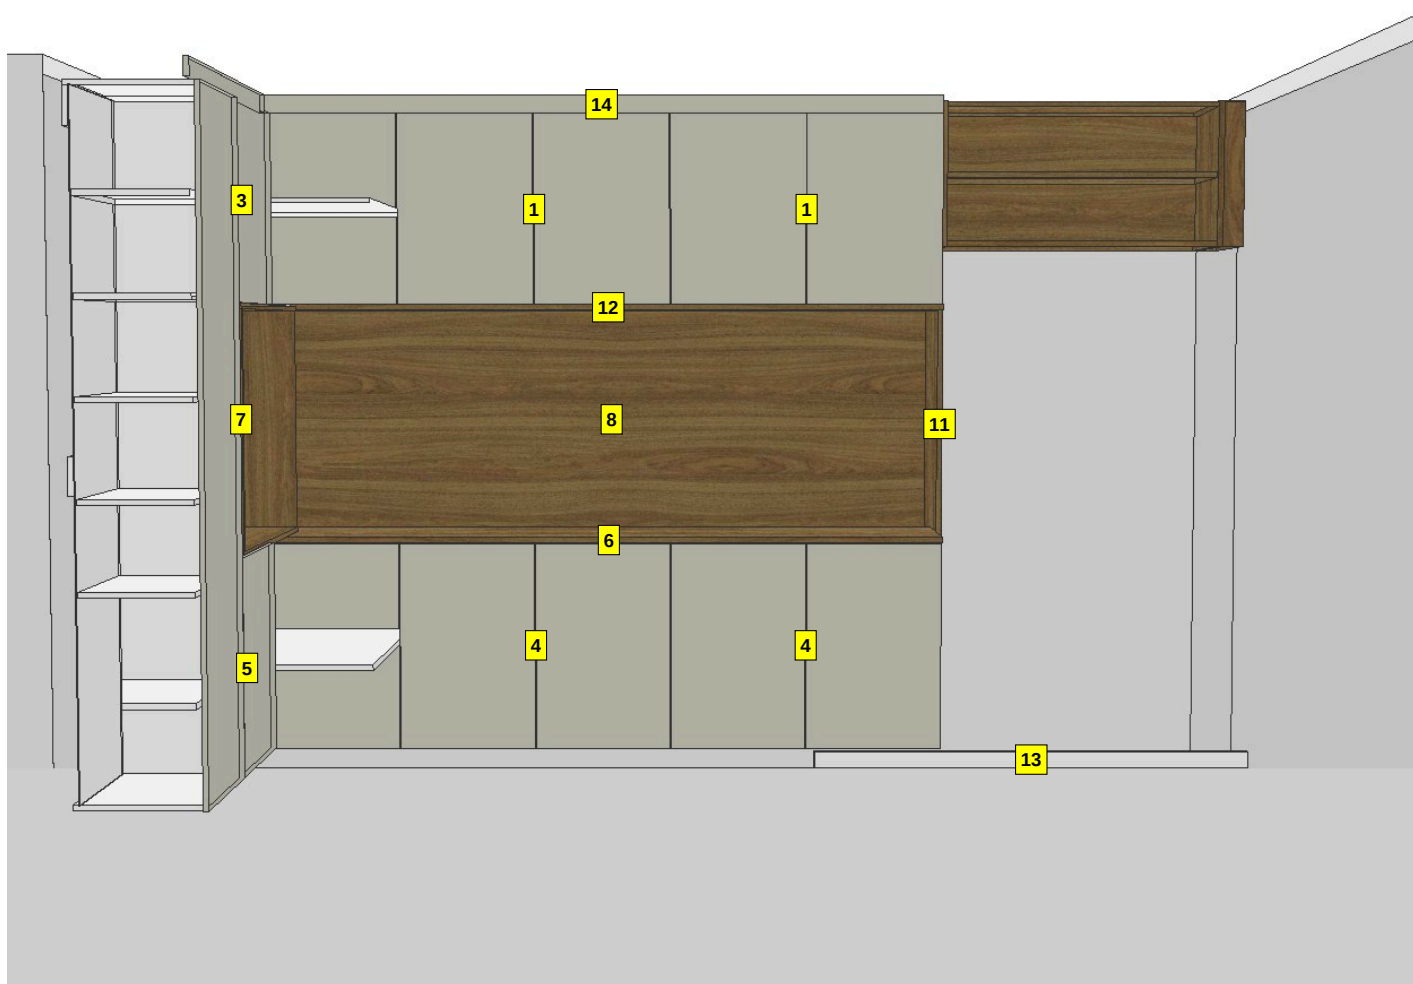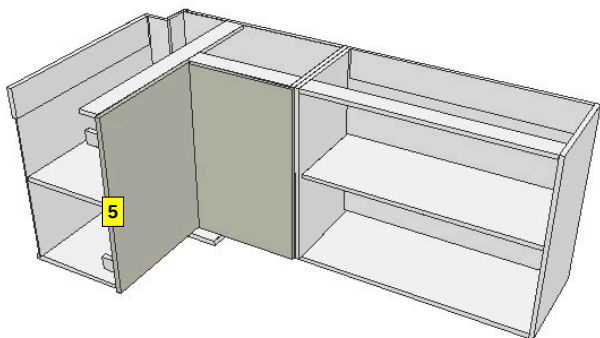



CLIENTE: **RAFAEL CLARET**

AMBIENTE: **Cozinha 2**

PROJETISTA TÉCNICO: **JOÃO FELIPE SANTOS**

ARQUITETA: **FERNANDA**

ATENÇÃO:

DECLARO ESTAR DE ACORDO COM ESTE PROJETO E COM AS MEDIDAS NELE DESCRITAS E CIENTE DE QUE NELE CONSTAM APENAS PEÇAS E MÓDULOS DA EMPRESA, SENDO QUE OS DEMAIS ITENS SÃO MERAMENTE ILUSTRATIVOS (TAIS COMO ELETROS, COLCHÕES, GRANITOS E DECORAÇÕES NO GERAL).


ASS.: _____

**PRANCHA
14**

MÓDULOS E PAINÉIS - VISTA D

Item	Descrição	Dimensão
1	Armário 1 Porta	500x2210x400
2	Painel Freijo Puro MDF	909x18x423
3	Painel Freijo Puro MDF	891x18x789
4	Tamponamento	2210x18x70
5	Tamponamento	789x18x423
6	Tamponamento	909x18x423
7	Vista	1064x18x60

DETALHE - NICHOS

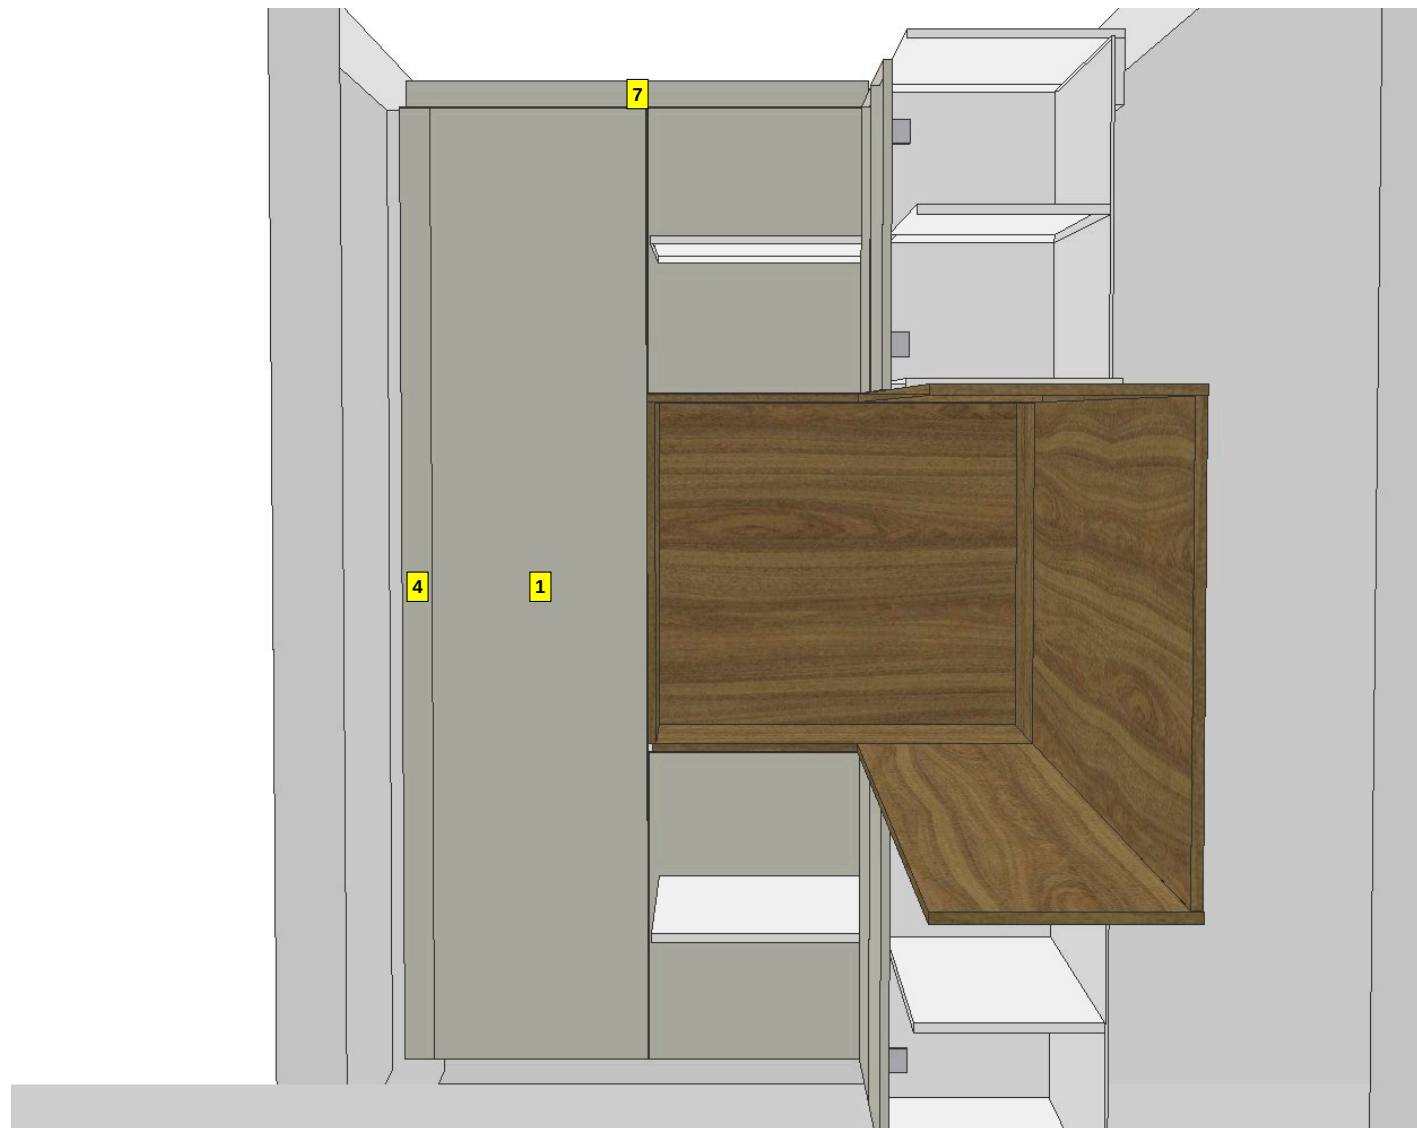



CLIENTE: **RAFAEL CLARET**

AMBIENTE: **Cozinha 2**

PROJETISTA TÉCNICO: **JOÃO FELIPE SANTOS**

ARQUITETA: **FERNANDA**


ATENÇÃO:

DECLARO ESTAR DE ACORDO COM ESTE PROJETO E COM AS MEDIDAS NELE DESCRITAS E CIENTE DE QUE NELE CONSTAM APENAS PEÇAS E MÓDULOS DA EMPRESA, SENDO QUE OS DEMAIS ITENS SÃO MERAMENTE ILUSTRATIVOS (TAIS COMO ELETROS, COLCHÕES, GRANITOS E DECORAÇÕES NO GERAL).


ASS.: _____

**PRANCHA
15**

MEDIDAS E ALTURAS - VISTAS C E D

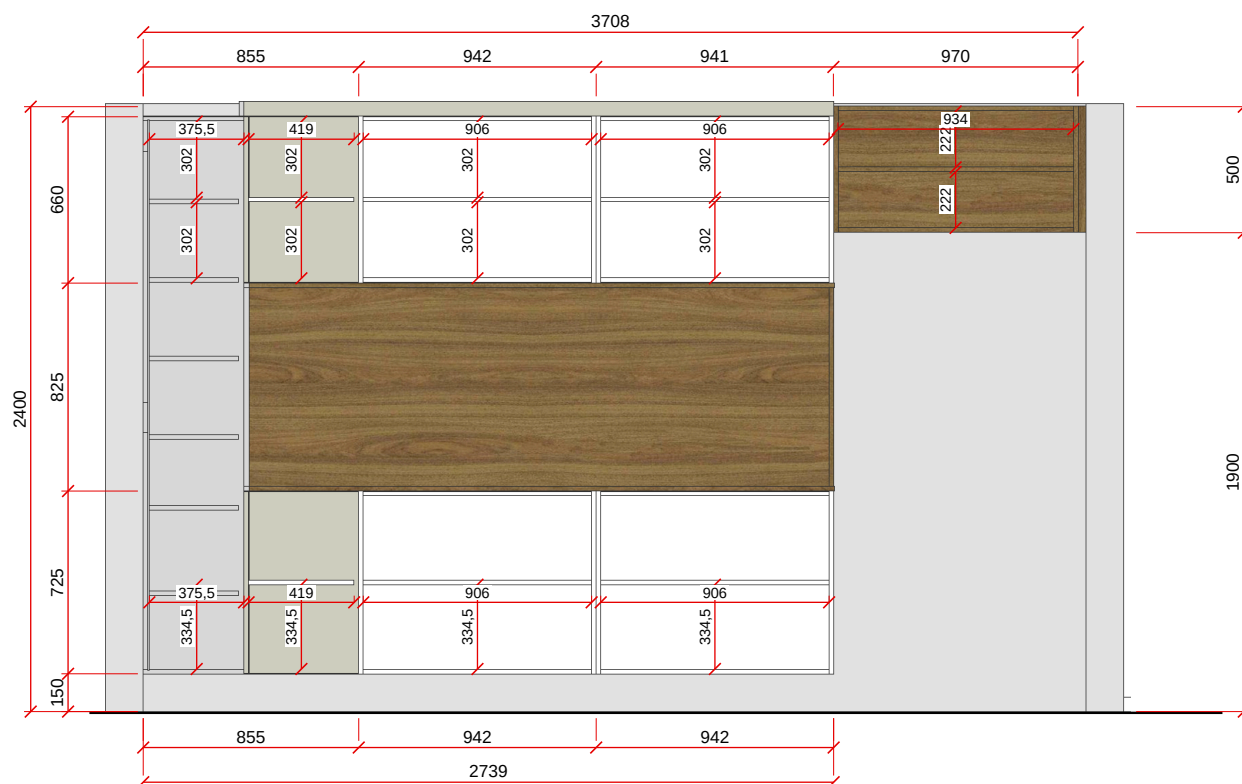

VISTA C - ESC. 1:30

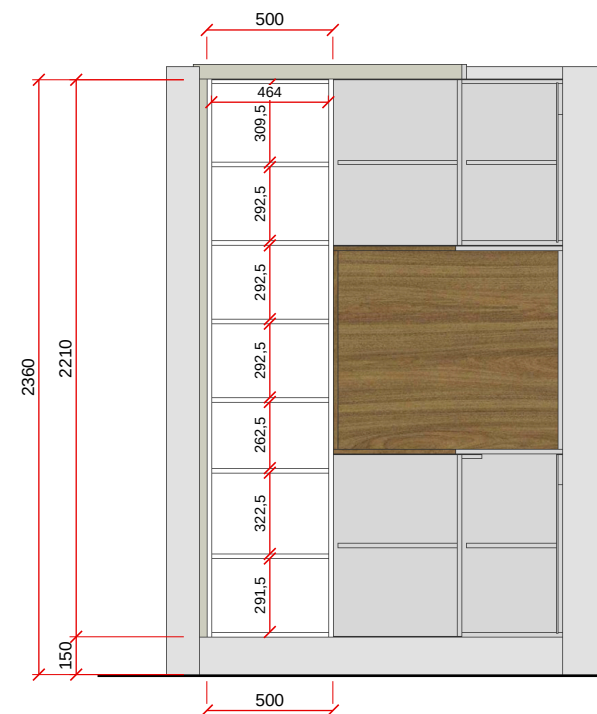

VISTA D - ESC. 1:30