



PRISCILA

EXECUTIVO - SUÍTE CASAL



CLIENTE: **PRISCILA**

AMBIENTE: **Suíte Casal**

PROJETISTA TÉCNICO: **JOÃO FELIPE SANTOS**

ARQUITETA: **FERNANDA**

ATENÇÃO:

DECLARO ESTAR DE ACORDO COM ESTE PROJETO E COM AS MEDIDAS NELE DESCRITAS E CIENTE DE QUE NELE CONSTAM APENAS PEÇAS E MÓDULOS DA EMPRESA, SENDO QUE OS DEMAIS ITENS SÃO MERAMENTE ILUSTRATIVOS (TAIS COMO ELETROS, COLCHÕES, GRANITOS E DECORAÇÕES NO GERAL).

ASS: _____

**PRANCHA
02**

CONTRATO

LEIA COM ATENÇÃO

1- CLIENTE ESTÁ RECEBENDO UMA CÓPIA DOS PROJETOS ADQUIRIDOS E ESTÁ DE ACORDO COM AS INFORMAÇÕES APONTADAS SOBRE MODELO, COR, ACABAMENTO, ESTRUTURAS, ACESSÓRIOS E CONDIÇÕES QUE FAZEM PARTE DESTES PROJETOS EXECUTIVOS.

2- O MESMO FOI ELABORADO CONSIDERANDO AS MEDIDAS REAIS DESTES AMBIENTES, SE HOUVER ALGUMA ALTERAÇÃO NO PÉ DIREITO OU NAS PAREDES, REFERENTE À INSTALAÇÃO DE MOLDURAS DE GESSO, RODAPÉS, MODIFICAÇÃO EM INSTALAÇÃO DA MODULAÇÃO NO DIA DA MONTAGEM, A EMPRESA NÃO SE RESPONSABILIZA QUANTO A FUTUROS CONTRATEMPOS DEVIDOS ÀS ALTERAÇÕES. CABE AO CLIENTE AVISAR O PROJETISTA ANTES DA MEDIÇÃO FINAL PARA ADEQUAÇÃO DA MODULAÇÃO.

3- SE HOUVER GRANITO NOS AMBIENTES, A MEDIÇÃO FINAL SE DARÁ APÓS A CONCLUSÃO DA INSTALAÇÃO DOS MESMOS, OU INSTALAR APÓS A MONTAGEM DOS MÓVEIS.

4- SE HOUVER REDUÇÃO OU RECORTES NOS MÓDULOS, O CLIENTE TOMA CIÊNCIA QUE OS AJUSTES SERÃO EXECUTADOS NO LOCAL, QUE DEVE ESTAR LIVRE DE OBJETOS E PESSOAS QUE POSSAM SOFRER DE ALGUMA MANEIRA COM O PÓ DECORRENTE DESSES AJUSTES E QUALQUER OBJETO QUE NÃO POSSA SER RETIRADO DEVE ESTAR DEVIDAMENTE COBERTO. POR NÃO POSSUIR PROFISSIONÁIS ESPECIALIZADOS EM INSTALAÇÕES DE ELETROS, INSTALAÇÕES HIDRÁULICAS, A EMPRESA NÃO EFETUARÁ ESSE TIPO DE SERVIÇO. É NECESSÁRIO FORNECER AS PLANTAS DE INSTALAÇÃO ELÉTRICA E HIDRÁULICA DOS AMBIENTES NO DIA DA MONTAGEM, É NECESSÁRIO O ACOMPANHAMENTO DO CLIENTE OU UM RESPONSÁVEL PELA OBRA, MAIOR QUE 18 ANOS PARA TIRAR EVENTUAIS DÚVIDAS DOS MONTADORES REFERENTE AOS LOCAIS ONDE É POSSÍVEL FAZER FURAÇÕES. A ASSINATURA DESSE PROJETO SUBSTITUI QUALQUER PROJETO ANTERIOR.

5- O CLIENTE DECLARA ESTAR CIENTE QUE CASO O PROJETO ENVOLVA ELETROS, OS MESMOS DEVERÃO ESTAR NO LOCAL NO DIA DA MONTAGEM PARA ADEQUAÇÃO DOS NICHOS NECESSÁRIOS, E SE NÃO COMPROU OS ELETROS, SE RESPONSABILIZA EM ADQUIRIR OS MESMOS DENTRO DAS MEDIDAS ESPECIFICADAS NESTE PROJETO.

6- DECLARO ESTAR DE ACORDO COM ESTE PROJETO E COM AS MEDIDAS NELE DESCRITAS E CIENTE DE QUE NELE CONSTAM APENAS PEÇAS E MÓDULOS DA EMPRESA DUO PLANEJADOS, SENDO QUE OS DEMAIS ITENS SÃO MERAMENTE ILUSTRATIVOS (TAIS COMO ELETROS, COLCHÕES, GRANITOS E DECORAÇÕES EM GERAL).



CLIENTE: **PRISCILA**

AMBIENTE: **Suíte Casal**

PROJETISTA TÉCNICO: **JOÃO FELIPE SANTOS**

ARQUITETA: **FERNANDA**

ATENÇÃO:

DECLARO ESTAR DE ACORDO COM ESTE PROJETO E COM AS MEDIDAS NELE DESCRITAS E CIENTE DE QUE NELE CONSTAM APENAS PEÇAS E MÓDULOS DA EMPRESA, SENDO QUE OS DEMAIS ITENS SÃO MERAMENTE ILUSTRATIVOS (TAIS COMO ELETROS, COLCHÕES, GRANITOS E DECORAÇÕES NO GERAL).

ASS:.. _____

**PRANCHA
03**

PLANTA - ESPECIFICAÇÕES DO PROJETO

ESPECIFICAÇÕES DO PROJETO

CORES E ACABAMENTOS:

Caixa Módulos (Interno): **Branco, Freijo Puro**

Portas e Frentes: **Nude, Branco, Freijo Puro**

Tamponamentos: **Nude, Freijo Puro, Branco**

Painéis e Tampos: **Freijo Puro, Branco, Nude**

Puxadores: **Champagne**

Portas de Vidro:

FERRAGENS E ACESSÓRIOS:

Dobradiças:

Dobradiça Reta c/ Amortecedor, Dobradiça Curva c/ Amortecedor

Corrediças: **Gaveta Corrediça Telescópica**

Puxadores:

Puxador Linear (15, 18 e 20mm) Pino Champagne - 200mm

Ferragens especiais: **Cabideiro Tubo s/ Reforço**

ESPESSURAS:


Caixa Módulos (Interno): **18mm (fundo 6mm)**

Prateleiras internas: **18mm**

Portas e Frentes: **18mm**

Tamponamentos: **15mm e 18mm e 25mm**

Painéis e Tampos e perfil: **15mm e 18mm e 25mm**

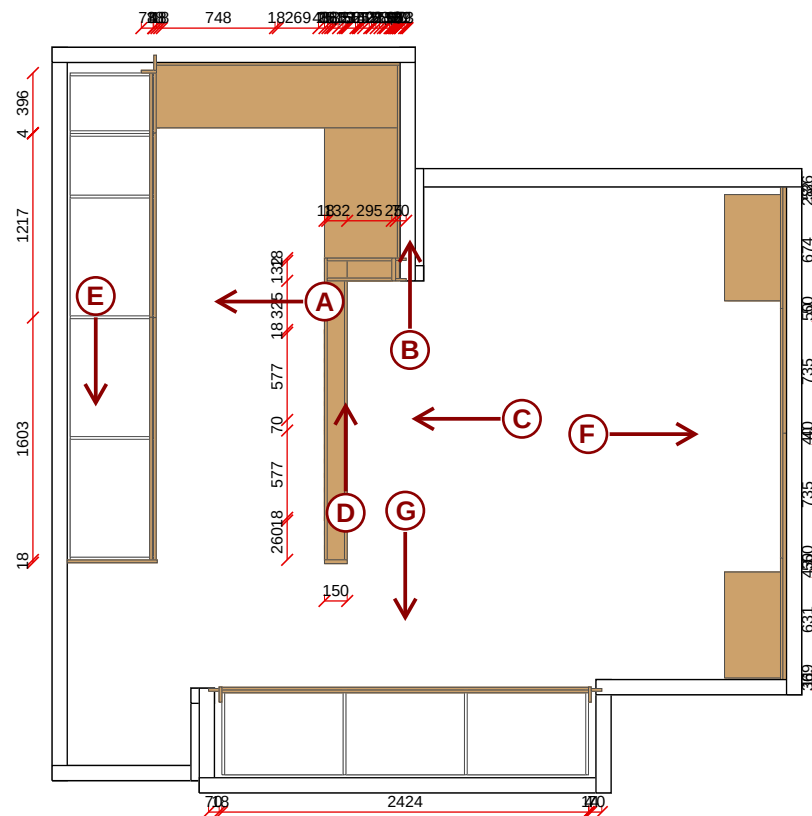

PLANTA BAIXA - ESC. 1:50



CLIENTE: **PRISCILA**

AMBIENTE: **Suíte Casal**

PROJETISTA TÉCNICO: **JOÃO FELIPE SANTOS**

ARQUITETA: **FERNANDA**

ATENÇÃO:


DECLARO ESTAR DE ACORDO COM ESTE PROJETO E COM AS MEDIDAS NELE DESCRITAS E CIENTE DE QUE NELE CONSTAM APENAS PEÇAS E MÓDULOS DA EMPRESA, SENDO QUE OS DEMAIS ITENS SÃO MERAMENTE ILUSTRATIVOS (TAIS COMO ELETROS, COLCHÕES, GRANITOS E DECORAÇÕES NO GERAL).

ASS.: _____


PRANCHA 04

VISÃO GERAL DOS MÓVEIS

VISTA A

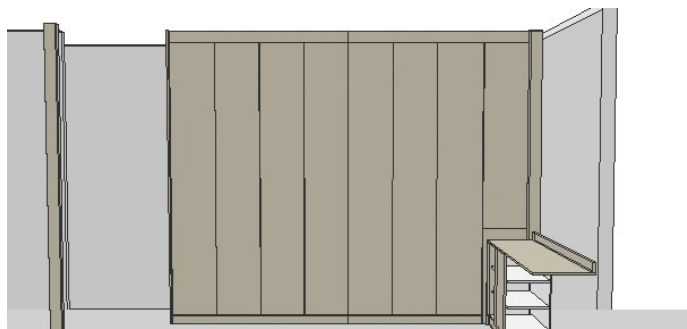


VISTA B

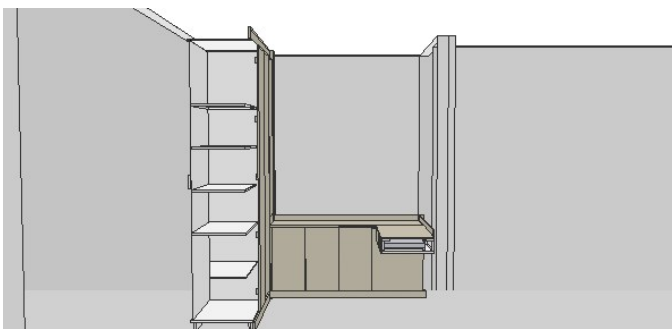


VISTA C



VISTA D

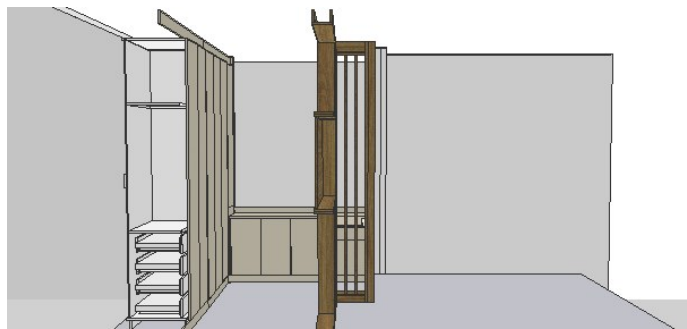


VISTA E

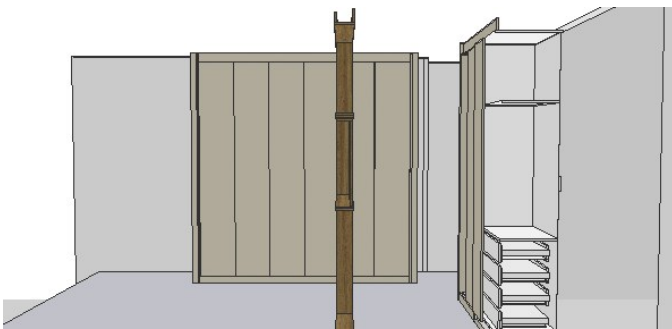

VISTA F



VISTA G

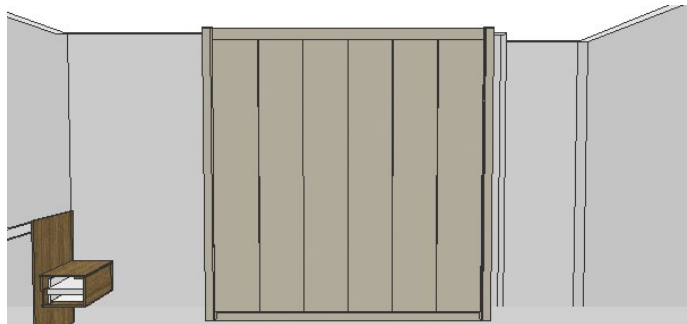



CLIENTE: **PRISCILA**

AMBIENTE: **Suíte Casal**

PROJETISTA TÉCNICO: **JOÃO FELIPE SANTOS**

ARQUITETA: **FERNANDA**

ATENÇÃO:

DECLARO ESTAR DE ACORDO COM ESTE PROJETO E COM AS MEDIDAS NELE DESCRITAS E CIENTE DE QUE NELE CONSTAM APENAS PEÇAS E MÓDULOS DA EMPRESA, SENDO QUE OS DEMAIS ITENS SÃO MERAMENTE ILUSTRATIVOS (TAIS COMO ELETROS, COLCHÕES, GRANITOS E DECORAÇÕES NO GERAL).


ASS: _____

**PRANCHA
05**

MÓDULOS E PAINÉIS - VISTA A

Item	Descrição	Dimensão
1	Armário c/ Portas de Giro c/ Rodapé	2820x2540x550
2	Armário c/ Portas de Giro c/ Rodapé	400x2540x550
3	Painel Nude MDP	868x18x396
4	Tamponamento Inferior	1217x18x80
5	Tamponamento Inferior	1603x18x80
6	Tamponamento Inferior	2645x18x595
7	Tamponamento Inferior	1605x18x100
8	Tamponamento Inferior	1615x18x100
9*	Gaveta Corrediça Telescópica	354x90x400
10*	Frete de Gaveta Reta	406x130x18

* não localizado no DXF - conferir

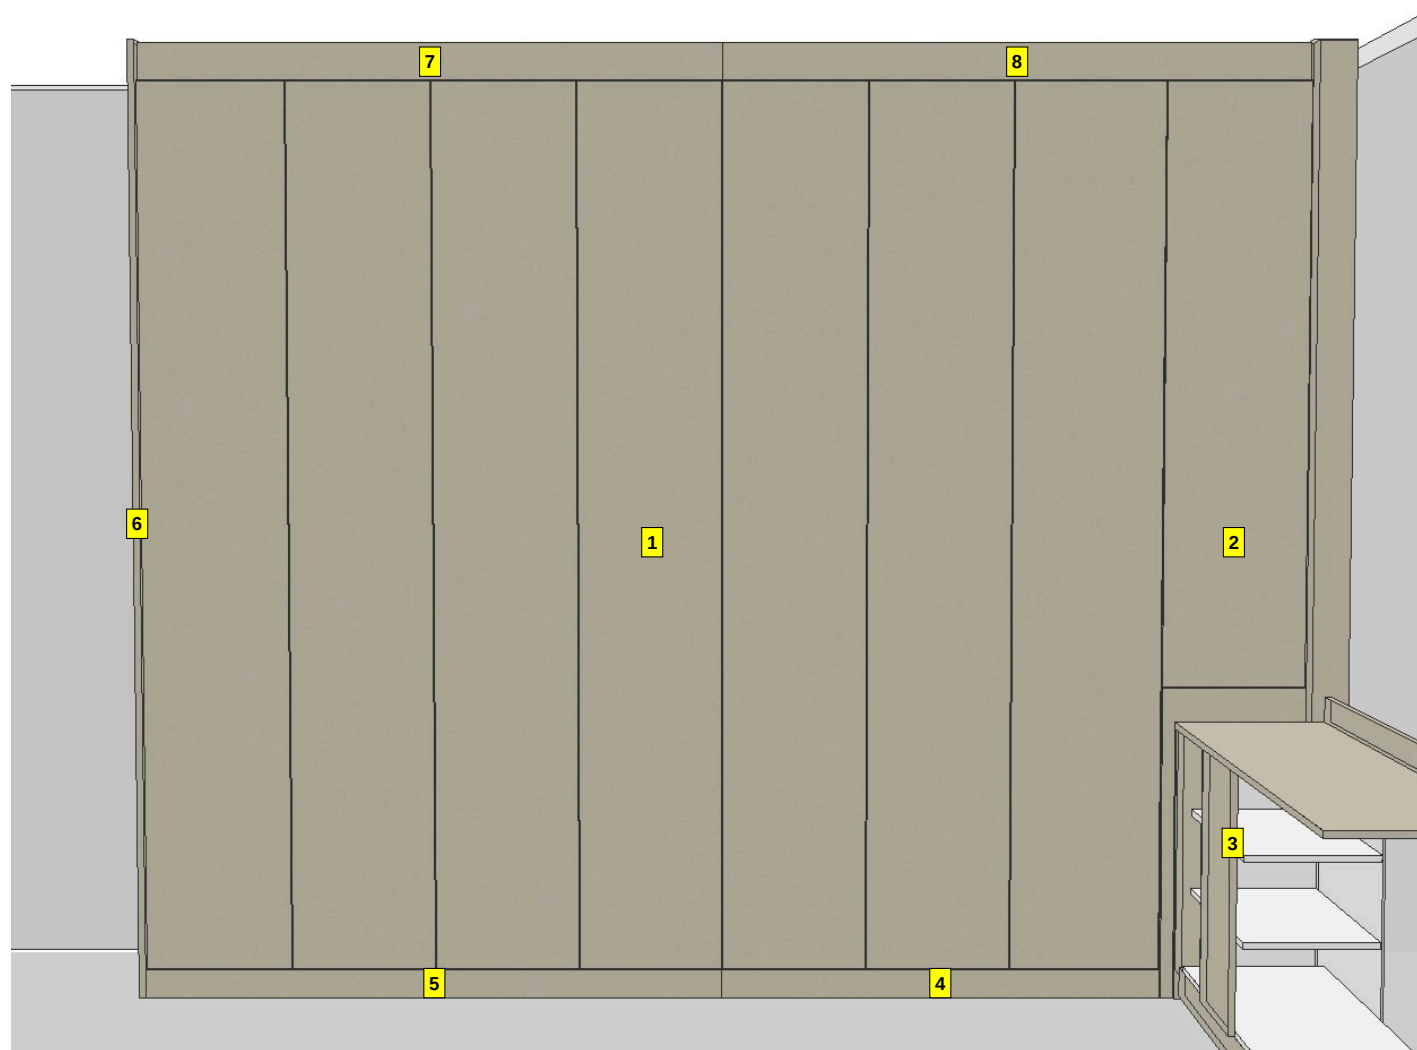



CLIENTE: **PRISCILA**

AMBIENTE: **Suíte Casal**

PROJETISTA TÉCNICO: **JOÃO FELIPE SANTOS**

ARQUITETA: **FERNANDA**

ATENÇÃO:


DECLARO ESTAR DE ACORDO COM ESTE PROJETO E COM AS MEDIDAS NELE DESCRITAS E CIENTE DE QUE NELE CONSTAM APENAS PEÇAS E MÓDULOS DA EMPRESA, SENDO QUE OS DEMAIS ITENS SÃO MERAMENTE ILUSTRATIVOS (TAIS COMO ELETROS, COLCHÕES, GRANITOS E DECORAÇÕES NO GERAL).

ASS.: _____

**PRANCHA
06**

MÓDULOS E PAINÉIS - VISTA B

Item	Descrição	Dimensão
1	Balcão Inferior	1560x675x390
2	Painel Branco MDP	784x18x480
3	Painel Branco MDP	790x15x99
4	Painel Branco MDP	465x18x99
5	Painel Branco MDP	784x18x70
6	Painel Branco MDP	135x18x480
7	Painel Freijo Puro MDF	2444x25x150
8	Painel Freijo Puro MDF	2645x25x150
9	Painel Freijo Puro MDF	287x15x70
10	Painel Freijo Puro MDF	333x15x70
11	Painel Freijo Puro MDF	363x15x70
12	Painel Freijo Puro MDF	136x15x70
13	Painel Nude MDP	135x18x70
14	Painel Nude MDP	670x18x540
15	Painel Nude MDP	1660x18x70
16	Painel Nude MDP	1660x18x432
17	Painel Nude MDP	1276x18x70
18	Painel Nude MDP	862x18x500
19	Tamponamento Inferior	2645x15x70
20	Tamponamento Inferior	2480x25x120
21	Tamponamento Inferior	2645x18x100
22	Tamponamento Inferior	1660x18x80
23	Tamponamento Inferior	755x18x100
24	Tamponamento Inferior	341x18x80
25	Tamponamento Inferior	1550x18x80
26	Tamponamento Inferior	135x18x500

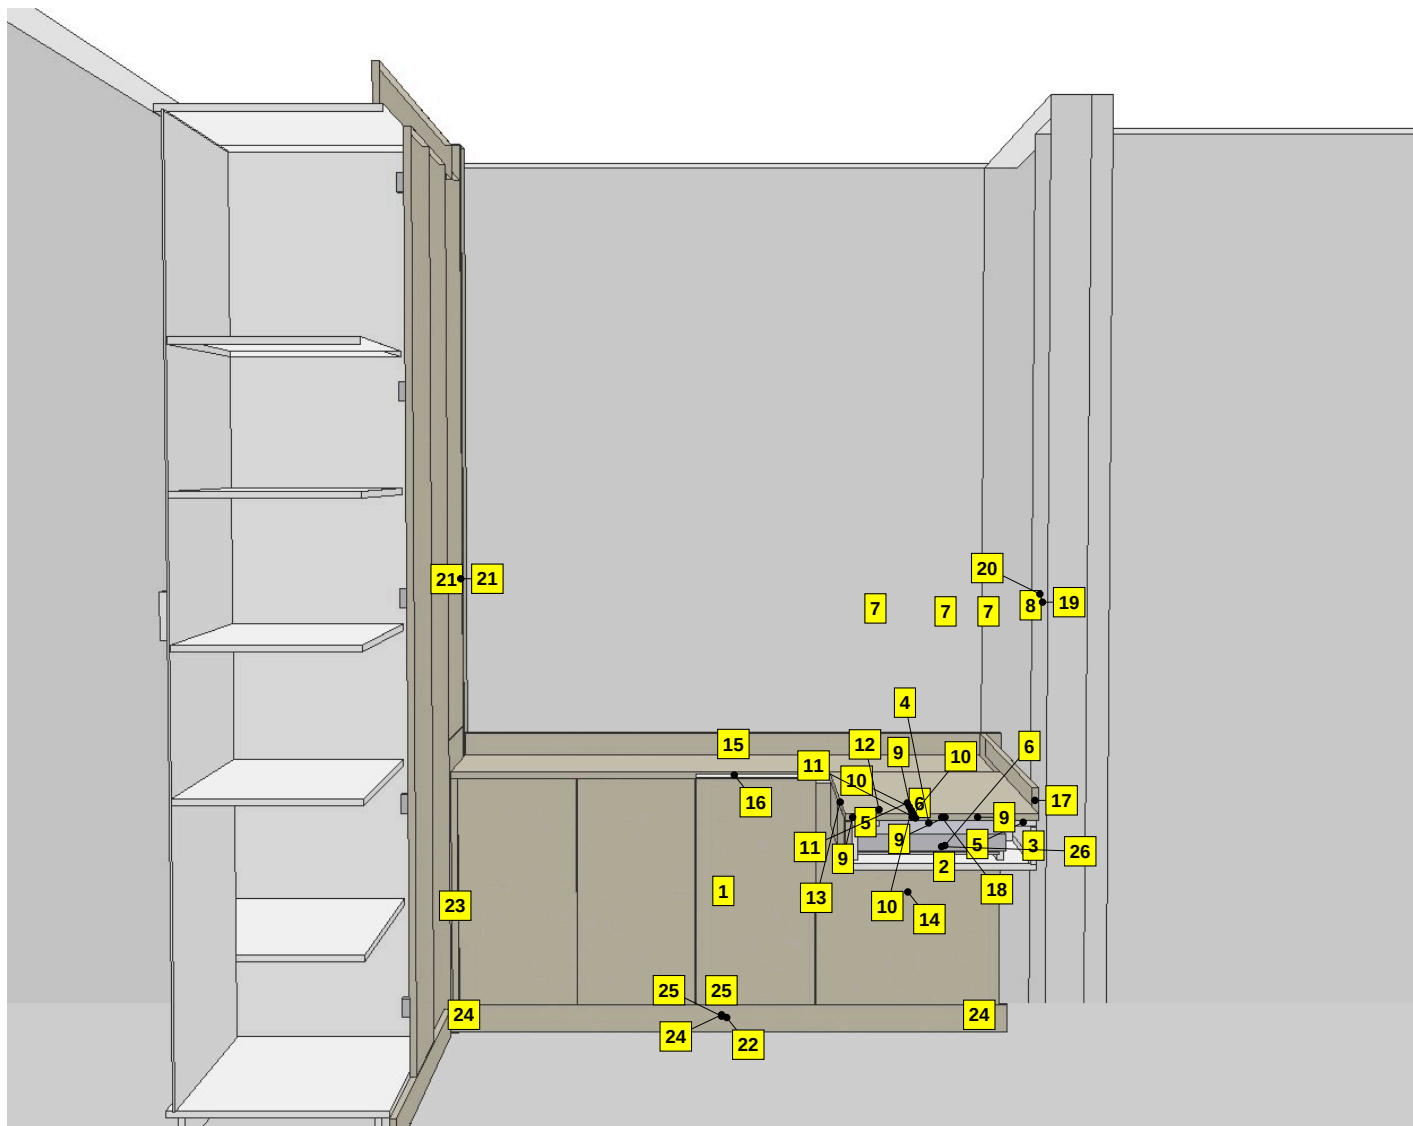



CLIENTE: **PRISCILA**

AMBIENTE: **Suíte Casal**

PROJETISTA TÉCNICO: **JOÃO FELIPE SANTOS**

ARQUITETA: **FERNANDA**


ATENÇÃO:

DECLARO ESTAR DE ACORDO COM ESTE PROJETO E COM AS MEDIDAS NELE DESCRITAS E CIENTE DE QUE NELE CONSTAM APENAS PEÇAS E MÓDULOS DA EMPRESA, SENDO QUE OS DEMAIS ITENS SÃO MERAMENTE ILUSTRATIVOS (TAIS COMO ELETROS, COLCHÕES, GRANITOS E DECORAÇÕES NO GERAL).


ASS.: _____

**PRANCHA
07**

MEDIDAS E ALTURAS - VISTAS A E B

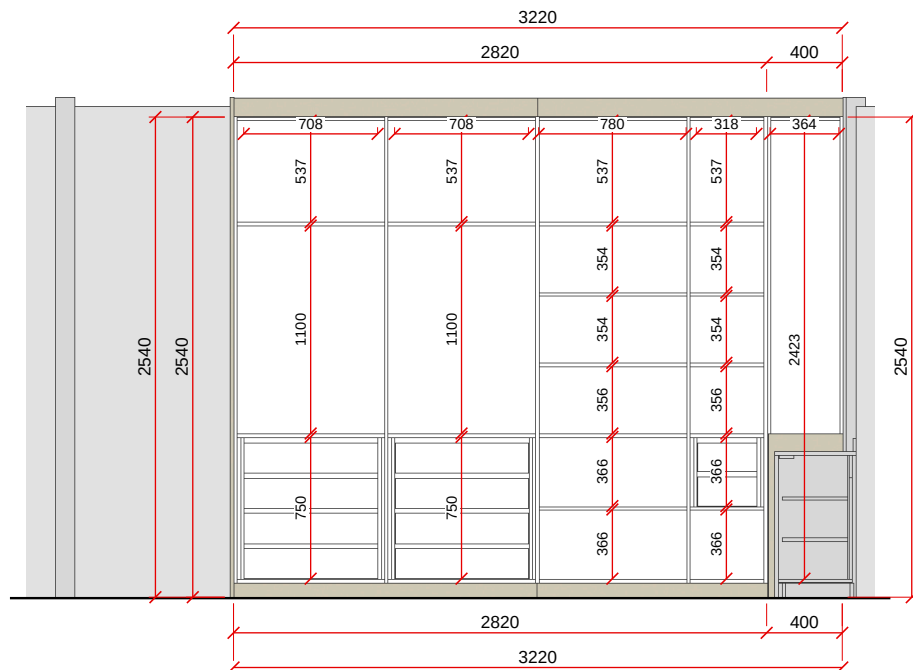

VISTA A - ESC. 1:40

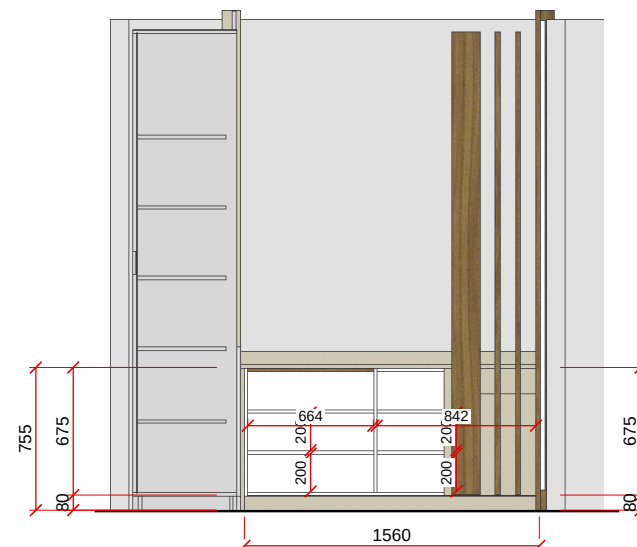

VISTA B - ESC. 1:40



CLIENTE: **PRISCILA**

AMBIENTE: **Suíte Casal**

PROJETISTA TÉCNICO: **JOÃO FELIPE SANTOS**

ARQUITETA: **FERNANDA**

ATENÇÃO:


DECLARO ESTAR DE ACORDO COM ESTE PROJETO E COM AS MEDIDAS NELE DESCRITAS E CIENTE DE QUE NELE CONSTAM APENAS PEÇAS E MÓDULOS DA EMPRESA, SENDO QUE OS DEMAIS ITENS SÃO MERAMENTE ILUSTRATIVOS (TAIS COMO ELETROS, COLCHÕES, GRANITOS E DECORAÇÕES NO GERAL).

ASS.: _____

**PRANCHA
08**

MÓDULOS E PAINÉIS - VISTA C

Item	Descrição	Dimensão
1	Painel Freijo Puro MDF	1260x18x150
2	Painel Freijo Puro MDF	1995x15x150
3	Painel Freijo Puro MDF	734x15x1224
4	Tamponamento Inferior	659x18x70
5	Tamponamento Inferior	1977x18x70
6	Tamponamento Inferior	641x18x70
7	Tamponamento Inferior	1845x18x100
8	Tamponamento Inferior	1995x18x100

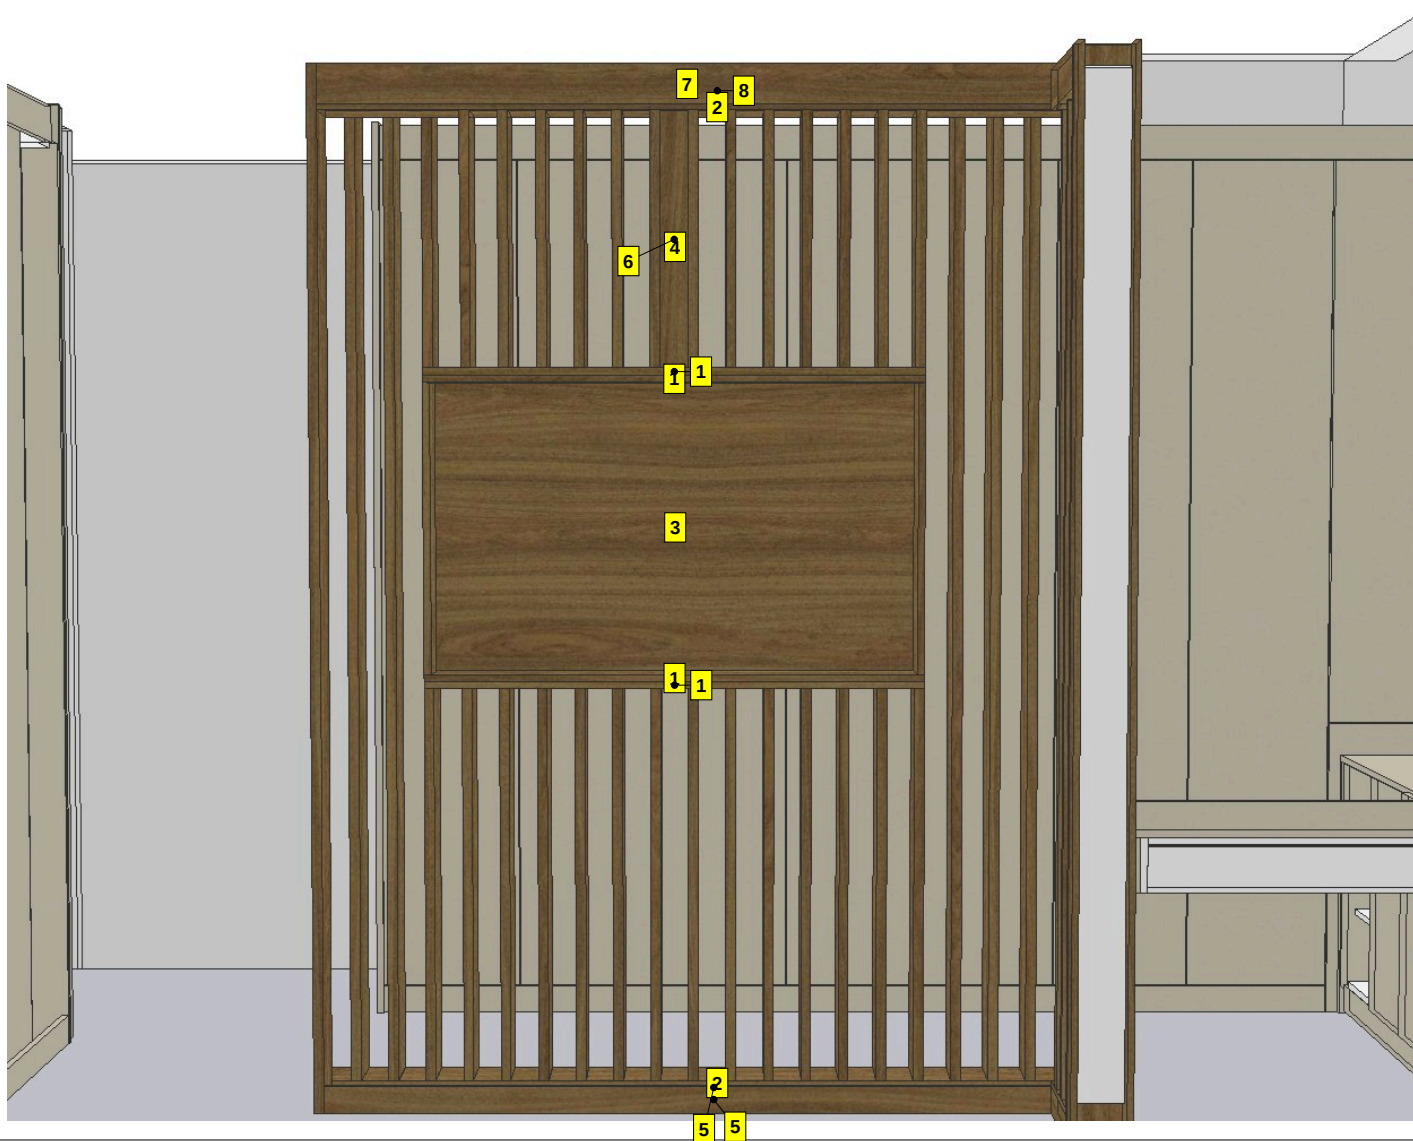



CLIENTE: **PRISCILA**

AMBIENTE: **Suíte Casal**

PROJETISTA TÉCNICO: **JOÃO FELIPE SANTOS**

ARQUITETA: **FERNANDA**

ATENÇÃO:


DECLARO ESTAR DE ACORDO COM ESTE PROJETO E COM AS MEDIDAS NELE DESCRITAS E CIENTE DE QUE NELE CONSTAM APENAS PEÇAS E MÓDULOS DA EMPRESA, SENDO QUE OS DEMAIS ITENS SÃO MERAMENTE ILUSTRATIVOS (TAIS COMO ELETROS, COLCHÕES, GRANITOS E DECORAÇÕES NO GERAL).

ASS.: _____

PRANCHA
09

MÓDULOS E PAINÉIS - VISTA D

Item	Descrição	Dimensão
1	Painel Freijo Puro MDF	997x25x150
2	Painel Freijo Puro MDF	641x25x150
3	Painel Freijo Puro MDF	295x15x150
4	Painel Freijo Puro MDF	2444x25x150
5	Painel Freijo Puro MDF	734x18x150
6	Tamponamento Inferior	427x18x100
7	Tamponamento Inferior	445x18x70
8	Tamponamento Inferior	295x18x70
9	Tamponamento Inferior	2645x15x70

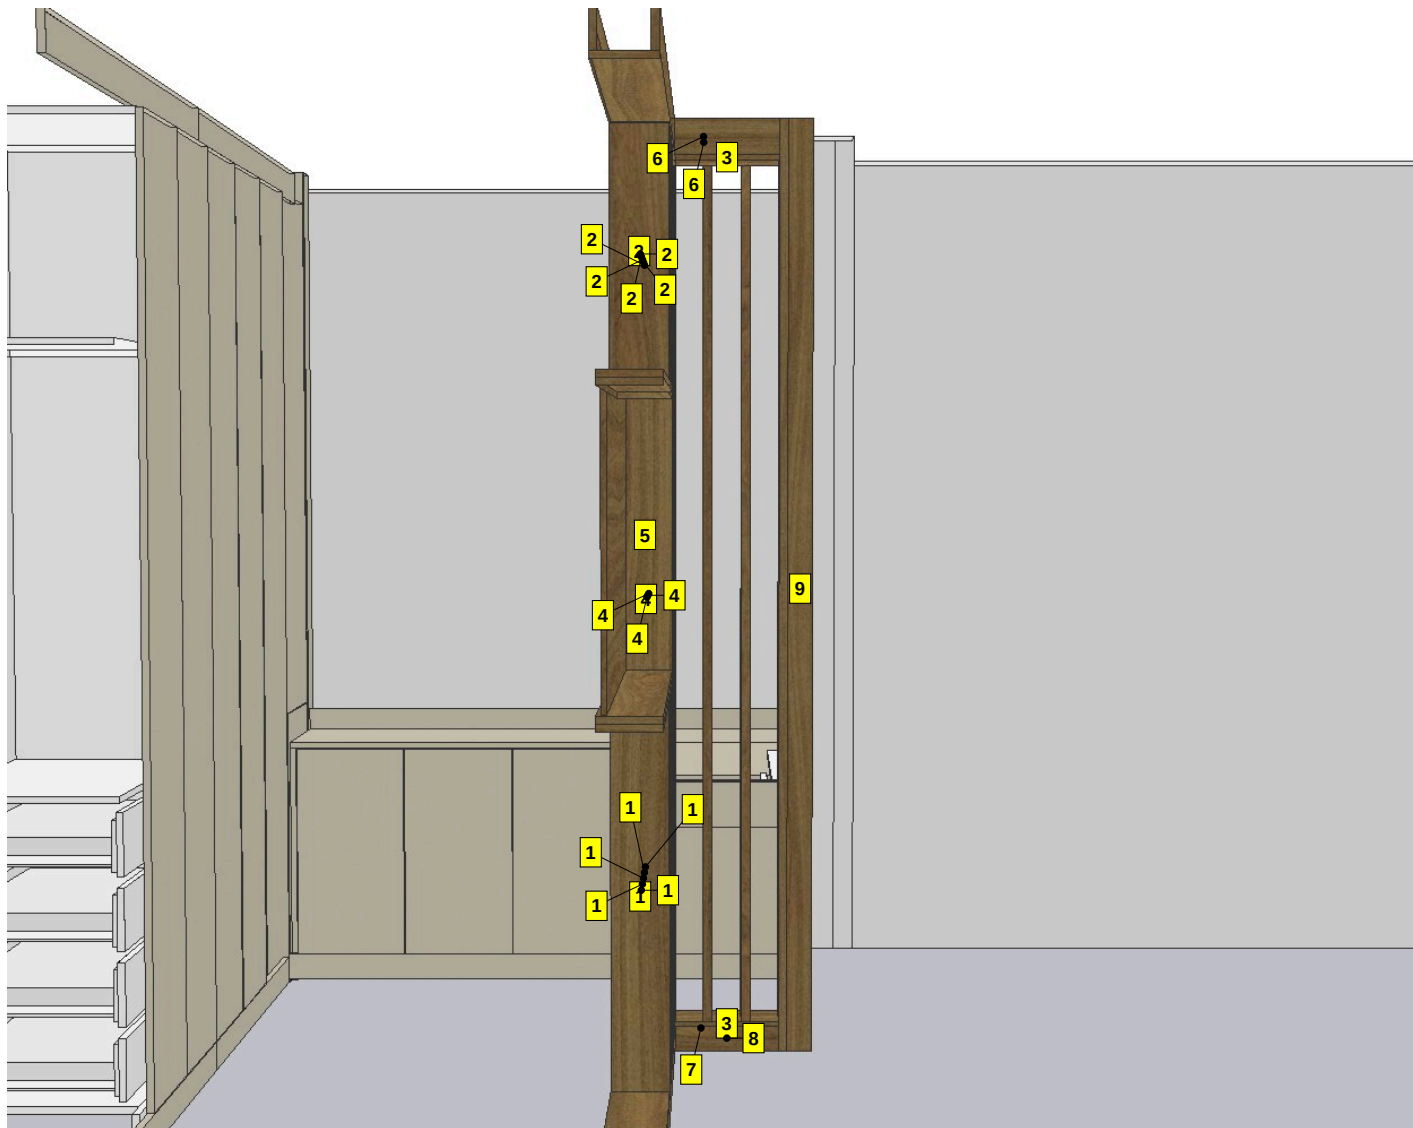



CLIENTE: **PRISCILA**

AMBIENTE: **Suíte Casal**

PROJETISTA TÉCNICO: **JOÃO FELIPE SANTOS**

ARQUITETA: **FERNANDA**


ATENÇÃO:

DECLARO ESTAR DE ACORDO COM ESTE PROJETO E COM AS MEDIDAS NELE DESCRITAS E CIENTE DE QUE NELE CONSTAM APENAS PEÇAS E MÓDULOS DA EMPRESA, SENDO QUE OS DEMAIS ITENS SÃO MERAMENTE ILUSTRATIVOS (TAIS COMO ELETROS, COLCHÕES, GRANITOS E DECORAÇÕES NO GERAL).


ASS.: _____

PRANCHA 10

MEDIDAS E ALTURAS - VISTAS C E D

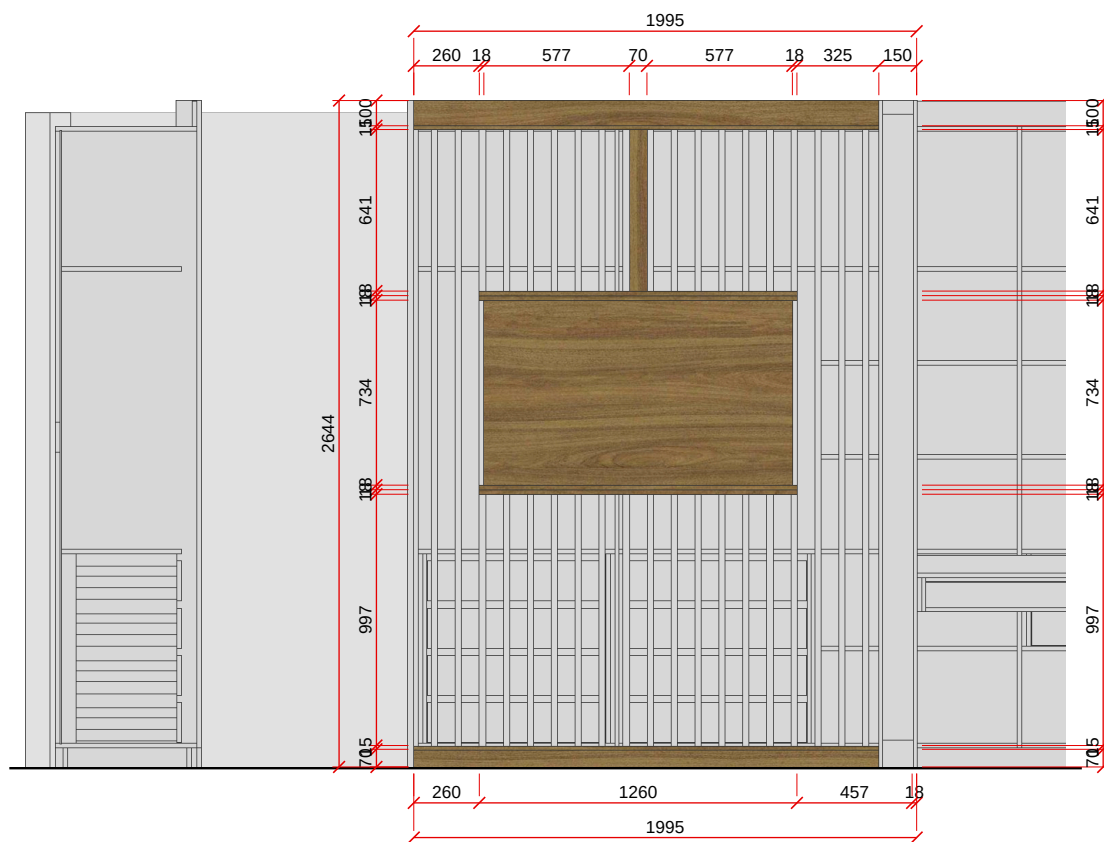

VISTA C - ESC. 1:30

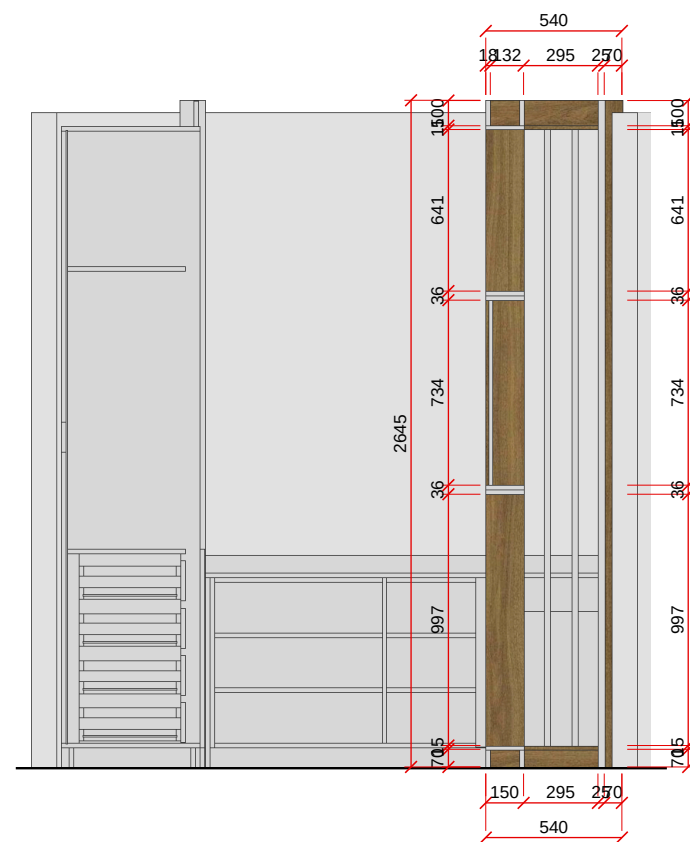

VISTA D - ESC. 1:30



CLIENTE: **PRISCILA**

AMBIENTE: **Suíte Casal**

PROJETISTA TÉCNICO: **JOÃO FELIPE SANTOS**

ARQUITETA: **FERNANDA**

ATENÇÃO:


DECLARO ESTAR DE ACORDO COM ESTE PROJETO E COM AS MEDIDAS NELE DESCRITAS E CIENTE DE QUE NELE CONSTAM APENAS PEÇAS E MÓDULOS DA EMPRESA, SENDO QUE OS DEMAIS ITENS SÃO MERAMENTE ILUSTRATIVOS (TAIS COMO ELETROS, COLCHÕES, GRANITOS E DECORAÇÕES NO GERAL).

ASS.: _____

PRANCHA 11

MÓDULOS E PAINÉIS - VISTA E

Item	Descrição	Dimensão
1	Painel Freijo Puro MDF	997x25x150
2	Painel Freijo Puro MDF	641x25x150
3	Painel Freijo Puro MDF	2444x25x150
4	Painel Freijo Puro MDF	734x18x150
5	Painel Freijo Puro MDF	2645x25x150

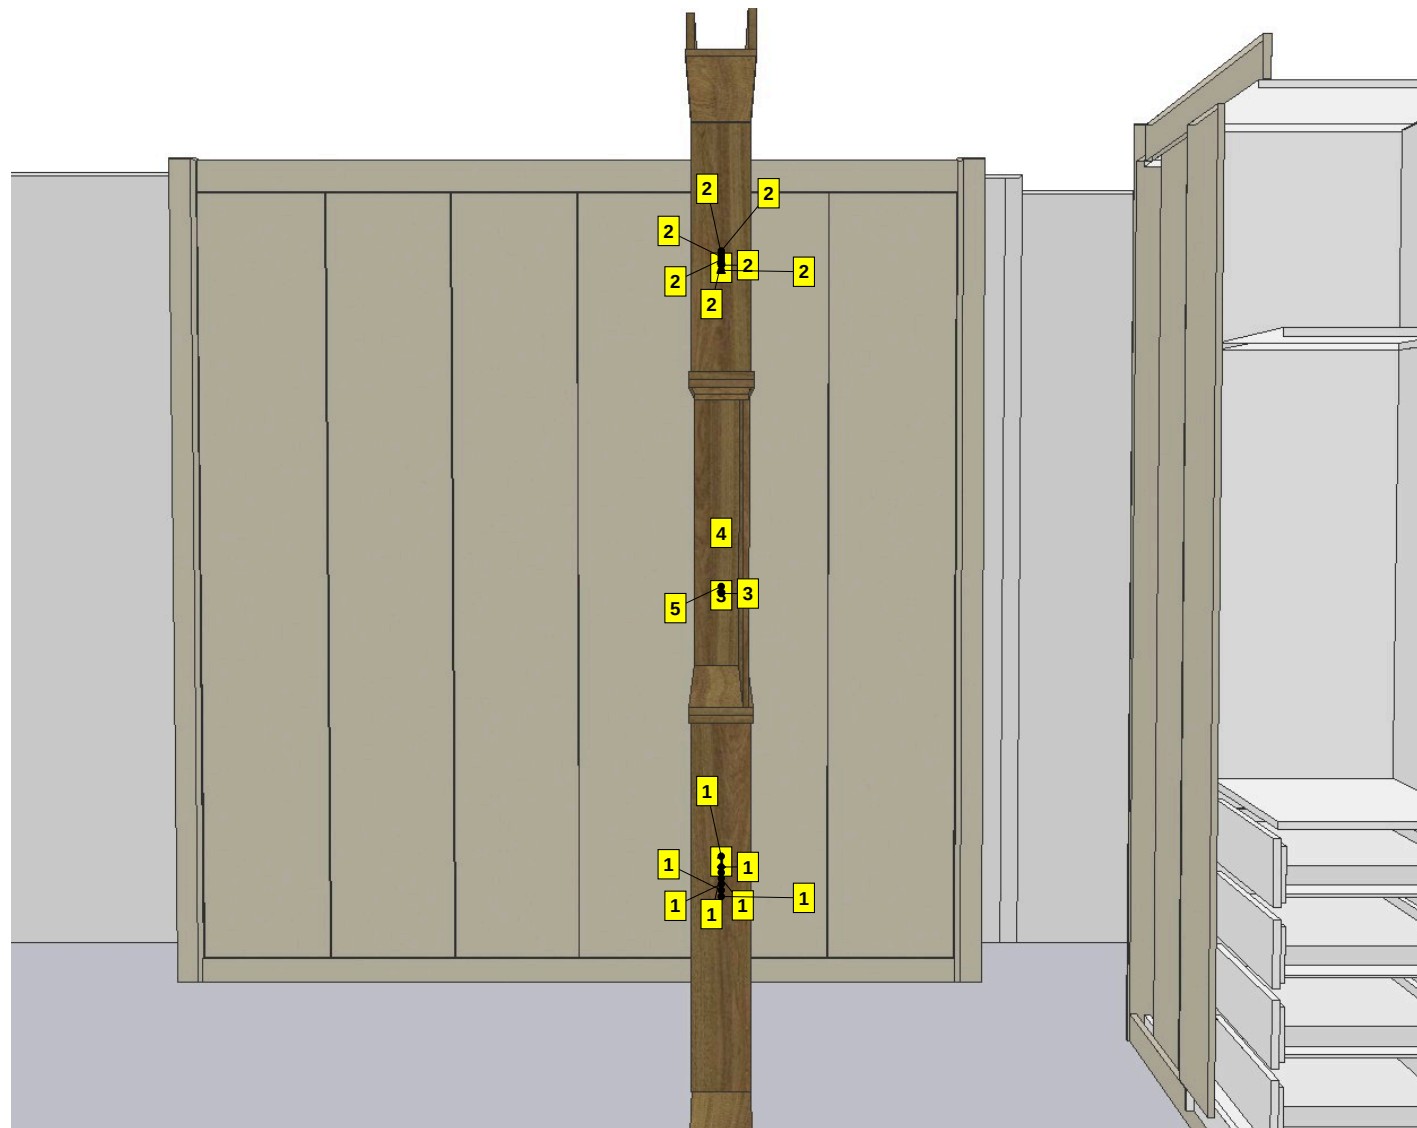



CLIENTE: **PRISCILA**

AMBIENTE: **Suíte Casal**

PROJETISTA TÉCNICO: **JOÃO FELIPE SANTOS**

ARQUITETA: **FERNANDA**


ATENÇÃO:

DECLARO ESTAR DE ACORDO COM ESTE PROJETO E COM AS MEDIDAS NELE DESCRITAS E CIENTE DE QUE NELE CONSTAM APENAS PEÇAS E MÓDULOS DA EMPRESA, SENDO QUE OS DEMAIS ITENS SÃO MERAMENTE ILUSTRATIVOS (TAIS COMO ELETROS, COLCHÕES, GRANITOS E DECORAÇÕES NO GERAL).


ASS.: _____

PRANCHA 12

MEDIDAS E ALTURAS - VISTA E

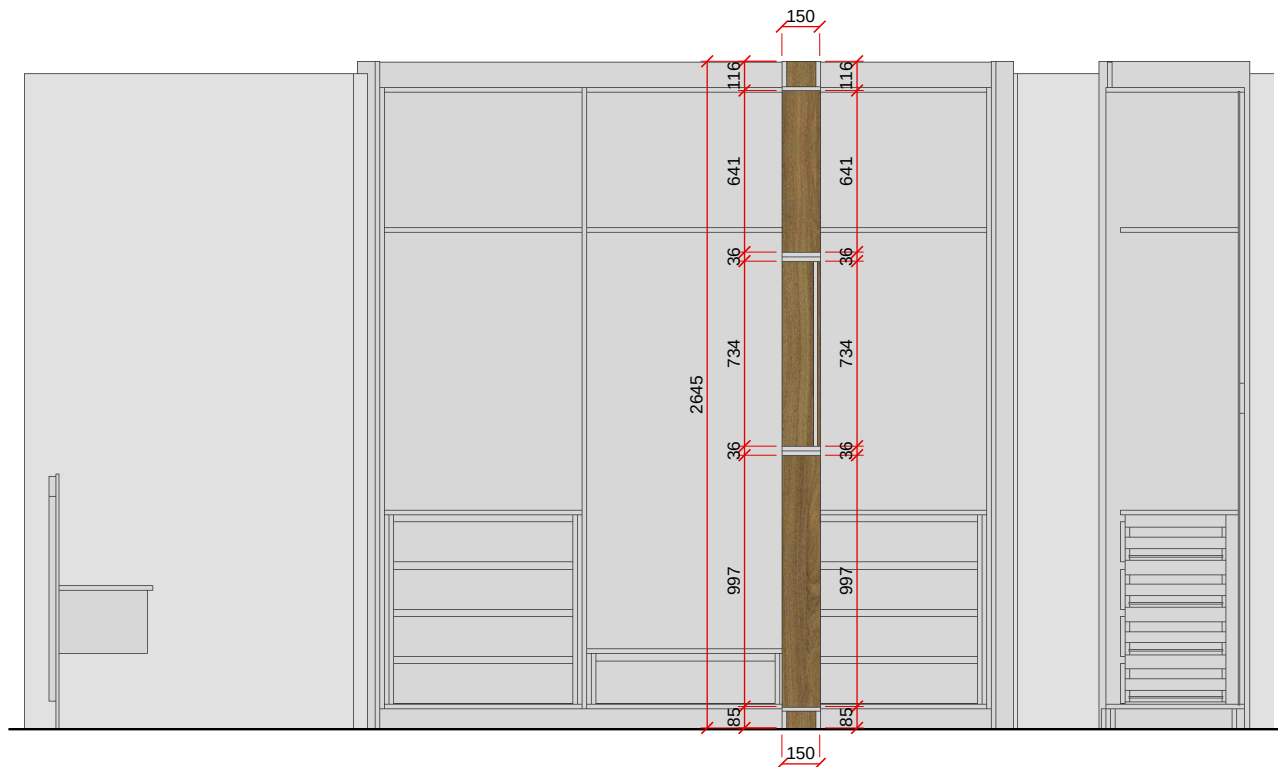

VISTA E - ESC. 1:30

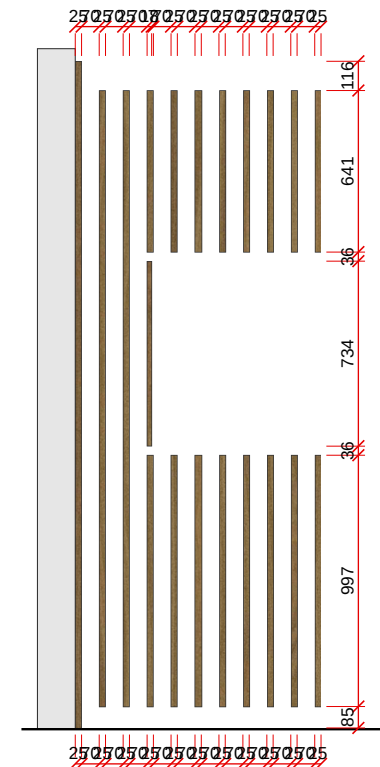

VISTA E - LATERAL - ESC. 1:30



CLIENTE: **PRISCILA**

AMBIENTE: **Suíte Casal**

PROJETISTA TÉCNICO: **JOÃO FELIPE SANTOS**

ARQUITETA: **FERNANDA**

ATENÇÃO:


DECLARO ESTAR DE ACORDO COM ESTE PROJETO E COM AS MEDIDAS NELE DESCRITAS E CIENTE DE QUE NELE CONSTAM APENAS PEÇAS E MÓDULOS DA EMPRESA, SENDO QUE OS DEMAIS ITENS SÃO MERAMENTE ILUSTRATIVOS (TAIS COMO ELETROS, COLCHÕES, GRANITOS E DECORAÇÕES NO GERAL).

ASS.: _____

PRANCHA 13

MÓDULOS E PAINÉIS - VISTA F

Item	Descrição	Dimensão
1	Balcão 1 Gaveta	700x250x350
2	Painel Branco MDF	810x25x80
3	Painel Branco MDF	810x25x100
4	Painel Branco MDF	1629x25x80
5	Painel Freijo Puro MDF	1010x15x840
6	Painel Freijo Puro MDF	1010x15x1650
7	Tamponamento Inferior	700x18x370
8	Tamponamento Inferior	702x18x370

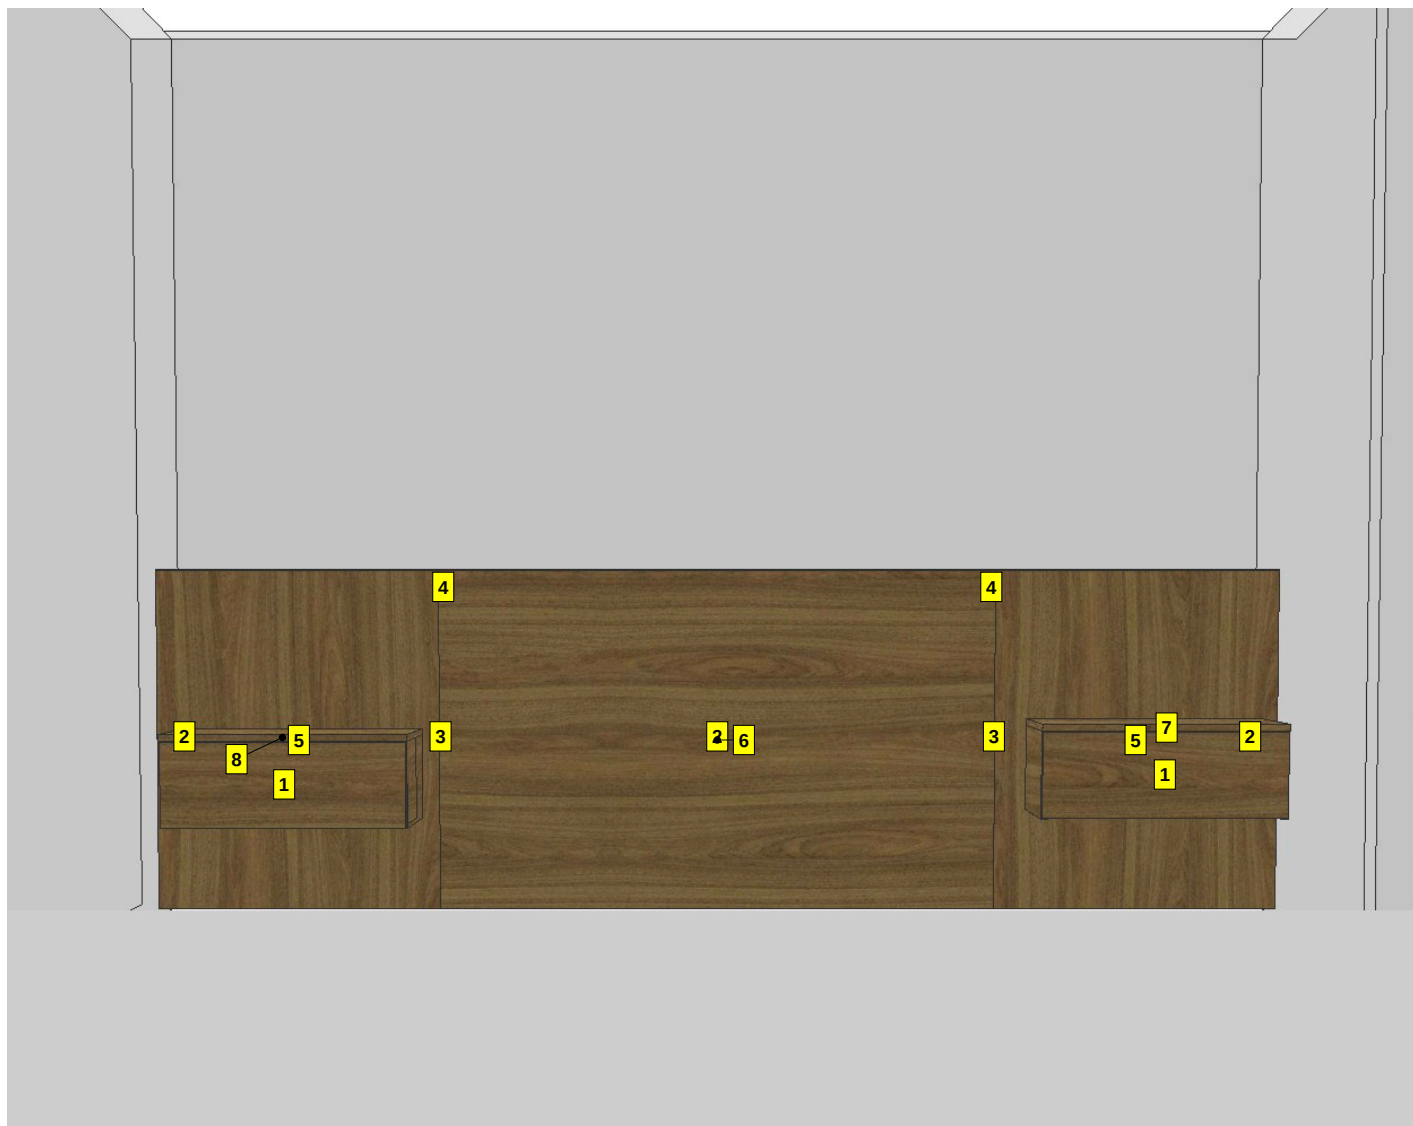



CLIENTE: **PRISCILA**

AMBIENTE: **Suíte Casal**

PROJETISTA TÉCNICO: **JOÃO FELIPE SANTOS**

ARQUITETA: **FERNANDA**

ATENÇÃO:

DECLARO ESTAR DE ACORDO COM ESTE PROJETO E COM AS MEDIDAS NELE DESCRITAS E CIENTE DE QUE NELE CONSTAM APENAS PEÇAS E MÓDULOS DA EMPRESA, SENDO QUE OS DEMAIS ITENS SÃO MERAMENTE ILUSTRATIVOS (TAIS COMO ELETROS, COLCHÕES, GRANITOS E DECORAÇÕES NO GERAL).


ASS.: _____

PRANCHA 14

MEDIDAS E ALTURAS - VISTA F



VISTA F - ESC. 1:25

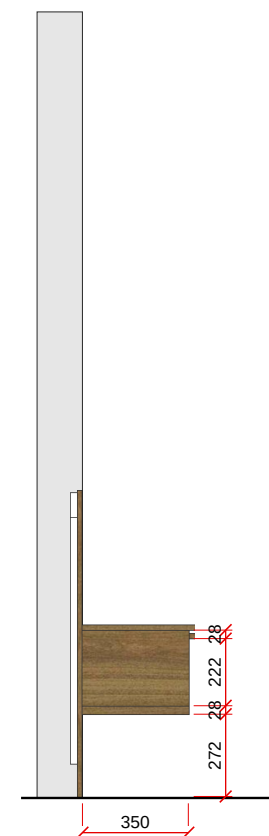

VISTA F - LATERAL - ESC. 1:25



CLIENTE: **PRISCILA**

AMBIENTE: **Suíte Casal**

PROJETISTA TÉCNICO: **JOÃO FELIPE SANTOS**

ARQUITETA: **FERNANDA**

ATENÇÃO:


DECLARO ESTAR DE ACORDO COM ESTE PROJETO E COM AS MEDIDAS NELE DESCRITAS E CIENTE DE QUE NELE CONSTAM APENAS PEÇAS E MÓDULOS DA EMPRESA, SENDO QUE OS DEMAIS ITENS SÃO MERAMENTE ILUSTRATIVOS (TAIS COMO ELETROS, COLCHÕES, GRANITOS E DECORAÇÕES NO GERAL).

ASS.: _____

**PRANCHA
15**

MÓDULOS E PAINÉIS - VISTA G

Item	Descrição	Dimensão
1	Armário c/ Portas de Giro c/ Rodapé	2424x2540x560
2	Tamponamento Inferior	2428x18x80
3	Tamponamento Inferior	2645x18x70
4	Tamponamento Inferior	2645x18x100
5	Tamponamento Inferior	2424x18x100

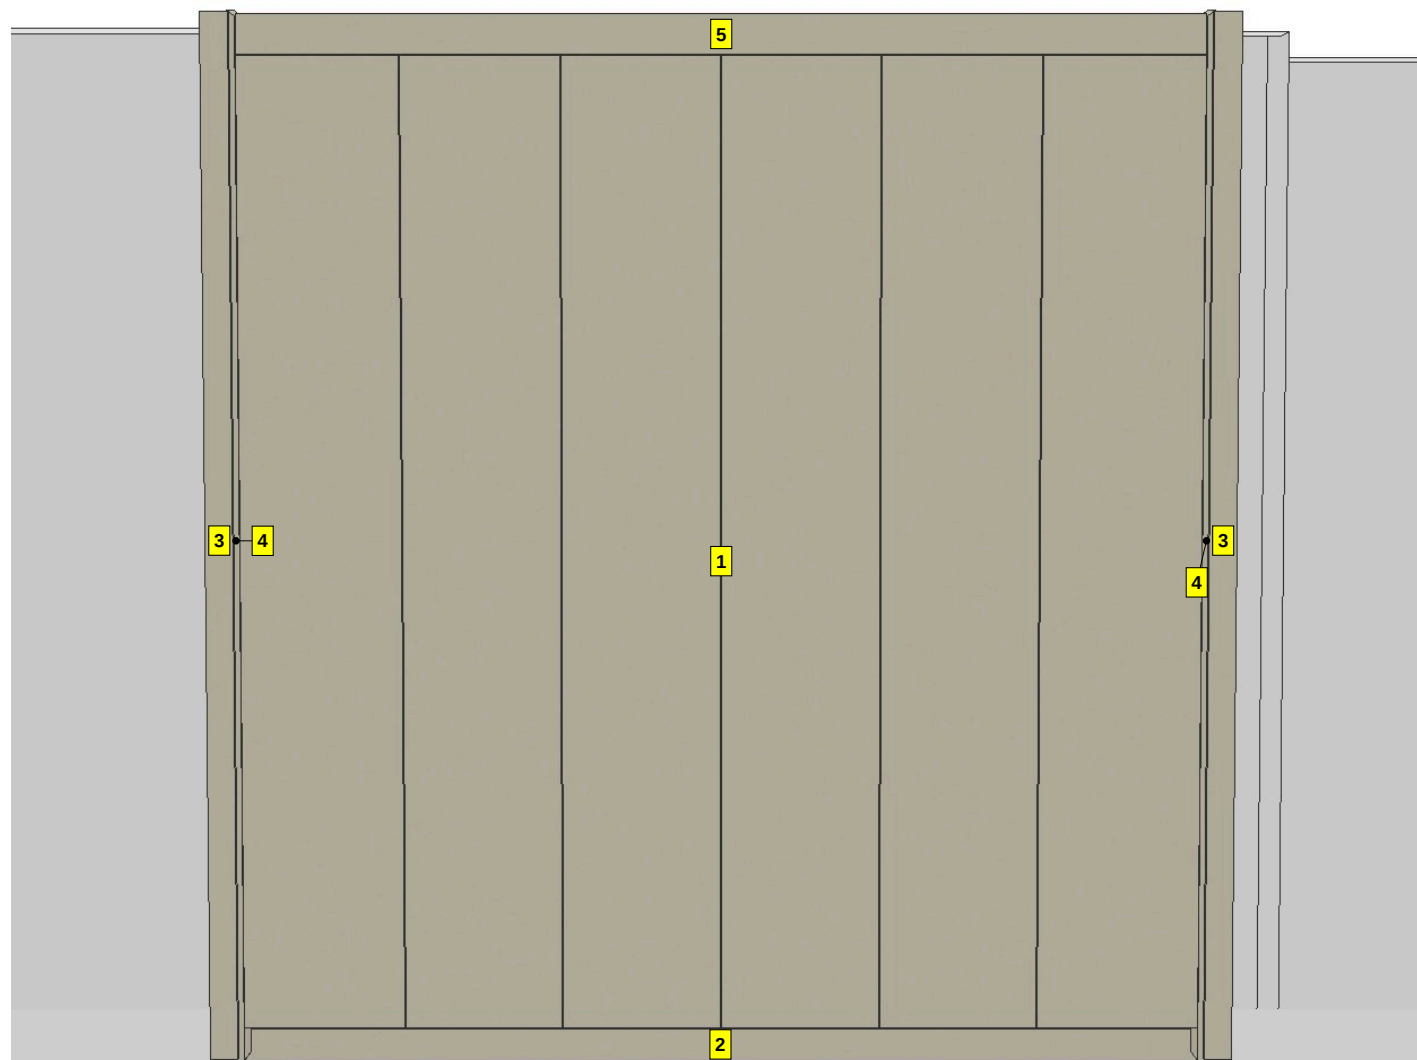



CLIENTE: **PRISCILA**

AMBIENTE: **Suíte Casal**

PROJETISTA TÉCNICO: **JOÃO FELIPE SANTOS**

ARQUITETA: **FERNANDA**


ATENÇÃO:

DECLARO ESTAR DE ACORDO COM ESTE PROJETO E COM AS MEDIDAS NELE DESCRITAS E CIENTE DE QUE NELE CONSTAM APENAS PEÇAS E MÓDULOS DA EMPRESA, SENDO QUE OS DEMAIS ITENS SÃO MERAMENTE ILUSTRATIVOS (TAIS COMO ELETROS, COLCHÕES, GRANITOS E DECORAÇÕES NO GERAL).


ASS:.. _____

PRANCHA 16

MEDIDAS E ALTURAS - VISTA G

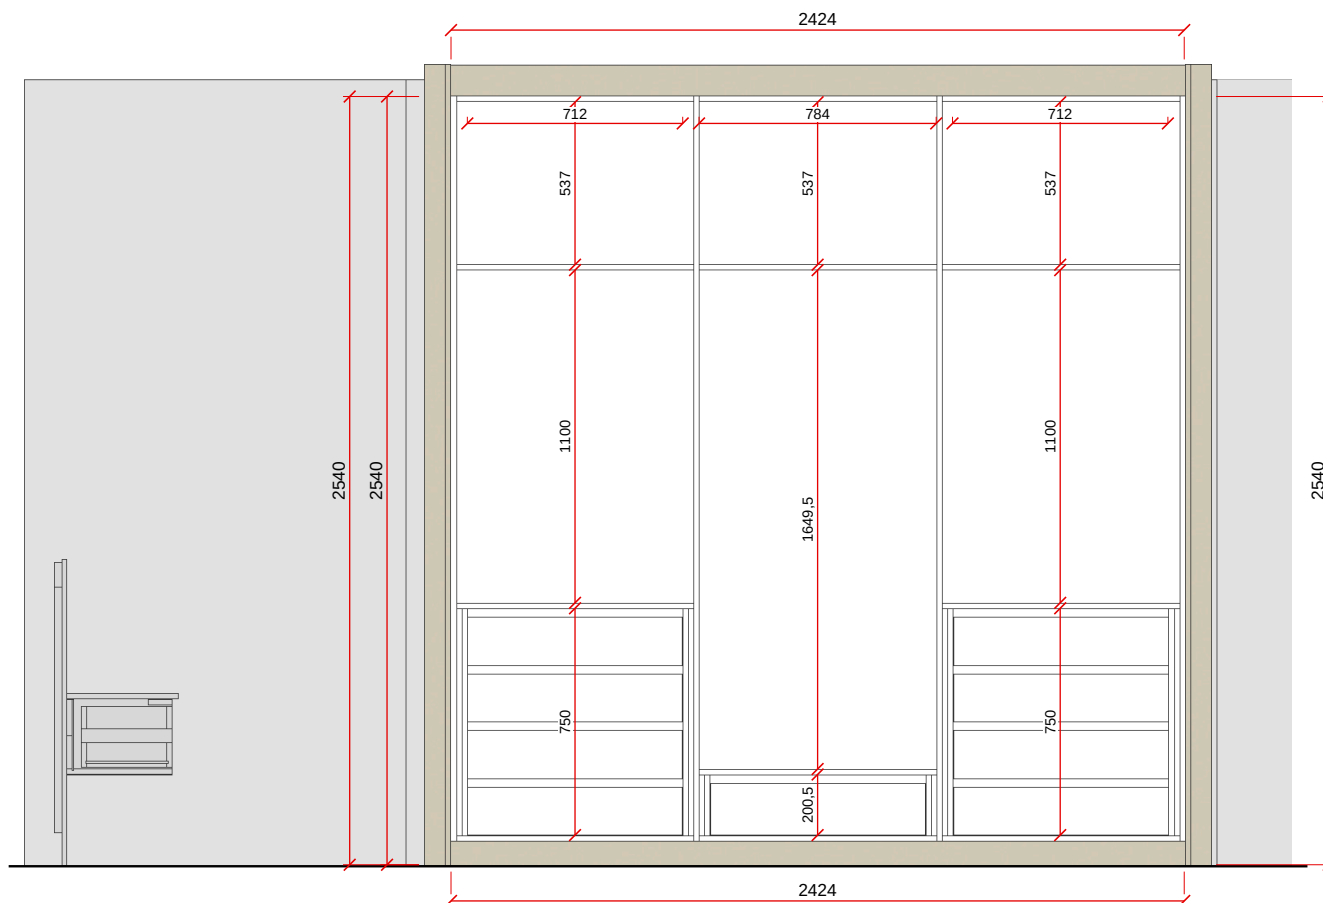

VISTA G - ESC. 1:25

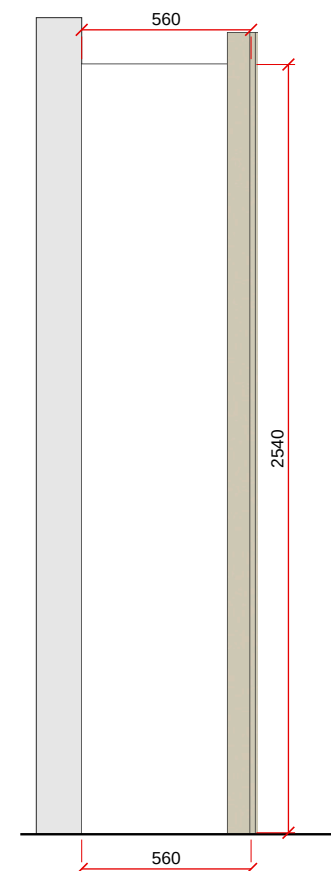

VISTA G - LATERAL - ESC. 1:25